


POZZETTO DI CALMA
scala 1:50

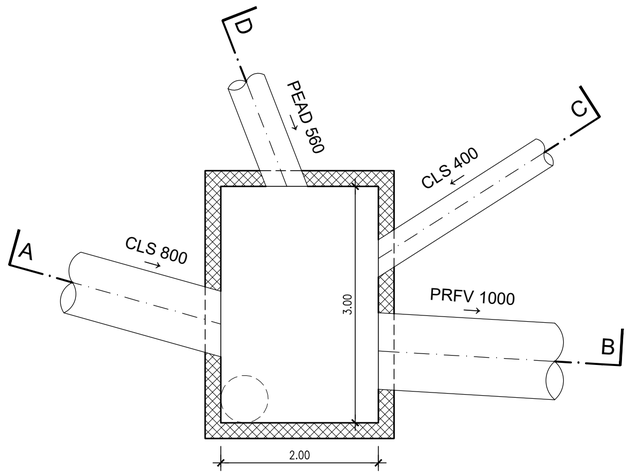


SEZIONE A-B
scala 1:50

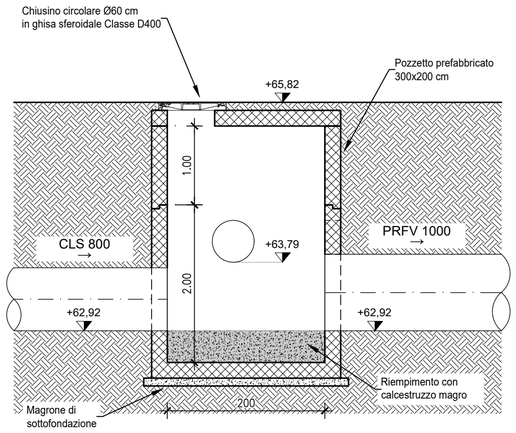


SEZIONE A-C
scala 1:50

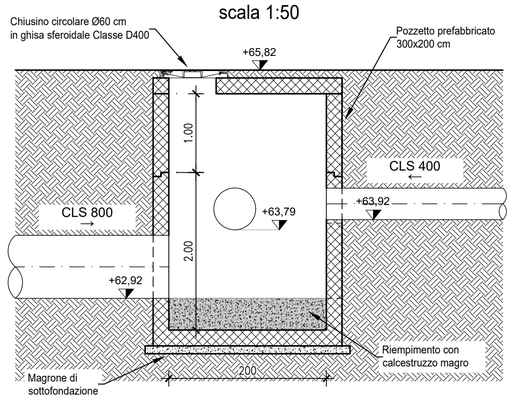


SEZIONE D-B
scala 1:50

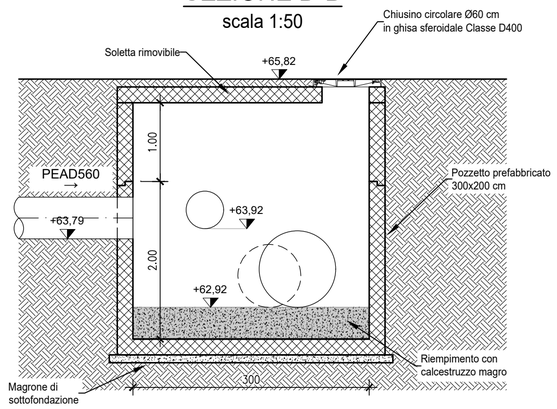


POZZETTO DI ISPEZIONE LINEA A GRAVITA' PEAD DE560
PIANTA
scala 1:50

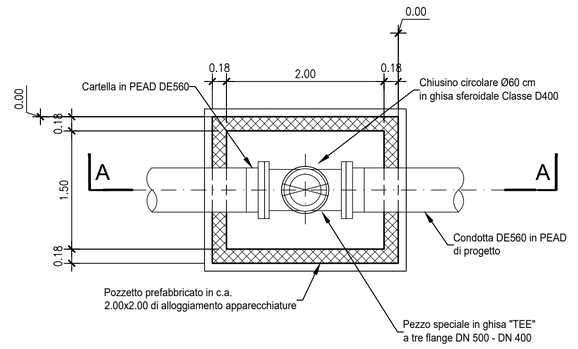


SEZIONE A-A
scala 1:50

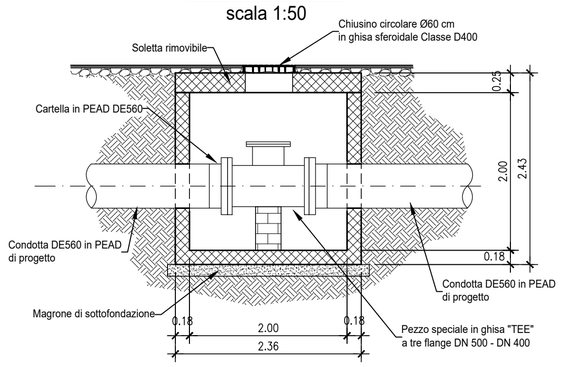


POZZETTO DI ISPEZIONE CIRCOLARE IN PRFV DN1200 PER INGRESSO CONDOTTE DN1000 (CON ANGOLAZIONE A RICHIESTA)

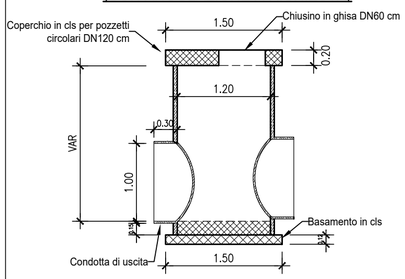


POZZETTO DI ISPEZIONE CIRCOLARE IN PRFV DN1200 PER INGRESSO CONDOTTE DN700 / 800 (CON ANGOLAZIONE A RICHIESTA)

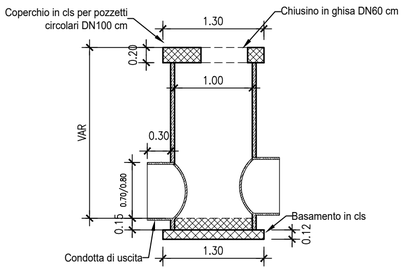

PEZZI SPECIALI A TEE PER ISPEZIONE SU LINEA DN800 (800x800) MASCHIO - MANICOTTO - MANICOTTO

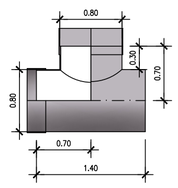

PEZZI SPECIALI A TEE PER ISPEZIONE SU LINEA DN1000 (1000 x 800) MASCHIO - MANICOTTO - MANICOTTO

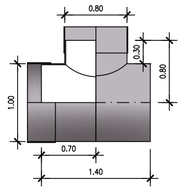

TUBO HOBAS DN700

		Unità	Tubo	Manicotto
Diametro nominale	DN	mm	700	700
Pressione nominale	PN	bar	1	1
Rigidezza nominale	SN	N/m²	16000	
Diametro esterno	d_e / $d_{e,Co}$	mm	718 +1/-2,2	739
Diametro interno, minimo	$d_{i,min}$ / $d_{i,Co}$	mm	673,8	719,2
Spessore, minimo	e	mm	17,32	4,4
Densità del materiale PRFV	ρ	kg/dm³	1,69	2
Tubo Peso al metro	m	kg/m	83,77	
Lunghezza nominale	LN	mm	6000 +60/-60	
Manicotto Peso per pezzo	m	kg/pcs		10,2
Manicotto Lunghezza	L_{Co}	mm		230

EN ISO 23856: Sistemi di tubazioni in PRFV per l'approvvigionamento idrico in pressione e non in pressione, il drenaggio o la fognatura
Conforme a DIN19523, pressione massima di getto d'acqua = 120 bar.

TUBO HOBAS DN800

		Unità	Tubo	Manicotto
Diametro nominale	DN	mm	800	800
Pressione nominale	PN	bar	1	1
Rigidezza nominale	SN	N/m²	16000	
Diametro esterno	d_e / $d_{e,Co}$	mm	820 +1/-2,4	843
Diametro interno, minimo	$d_{i,min}$ / $d_{i,Co}$	mm	768,9	821,5
Spessore, minimo	e	mm	19,24	5,5
Densità del materiale PRFV	ρ	kg/dm³	1,7	2
Tubo Peso al metro	m	kg/m	108,77	
Lunghezza nominale	LN	mm	6000 +60/-60	
Manicotto Peso per pezzo	m	kg/pcs		12,9
Manicotto Lunghezza	L_{Co}	mm		230


EN ISO 23856: Sistemi di tubazioni in PRFV per l'approvvigionamento idrico in pressione e non in pressione, il drenaggio o la fognatura
Conforme a DIN19523, pressione massima di getto d'acqua = 120 bar.

TUBO HOBAS DN1000

		Unità	Tubo	Manicotto
Diametro nominale	DN	mm	1000	1000
Pressione nominale	PN	bar	1	1
Rigidezza nominale	SN	N/m²	16000	
Diametro esterno	d_e / $d_{e,Co}$	mm	1026 +2/-2,6	1050
Diametro interno, minimo	$d_{i,min}$ / $d_{i,Co}$	mm	963,8	1027,4
Spessore, minimo	e	mm	24,41	6,1
Densità del materiale PRFV	ρ	kg/dm³	1,7	2
Tubo Peso al metro	m	kg/m	170,64	
Lunghezza nominale	LN	mm	6000 +60/-60	
Manicotto Peso per pezzo	m	kg/pcs		17
Manicotto Lunghezza	L_{Co}	mm		230

EN ISO 23856: Sistemi di tubazioni in PRFV per l'approvvigionamento idrico in pressione e non in pressione, il drenaggio o la fognatura
Conforme a DIN19523, pressione massima di getto d'acqua = 120 bar.

TUBO HOBAS SERIE DI DIAMETRI: DN700, DN800, DN1000

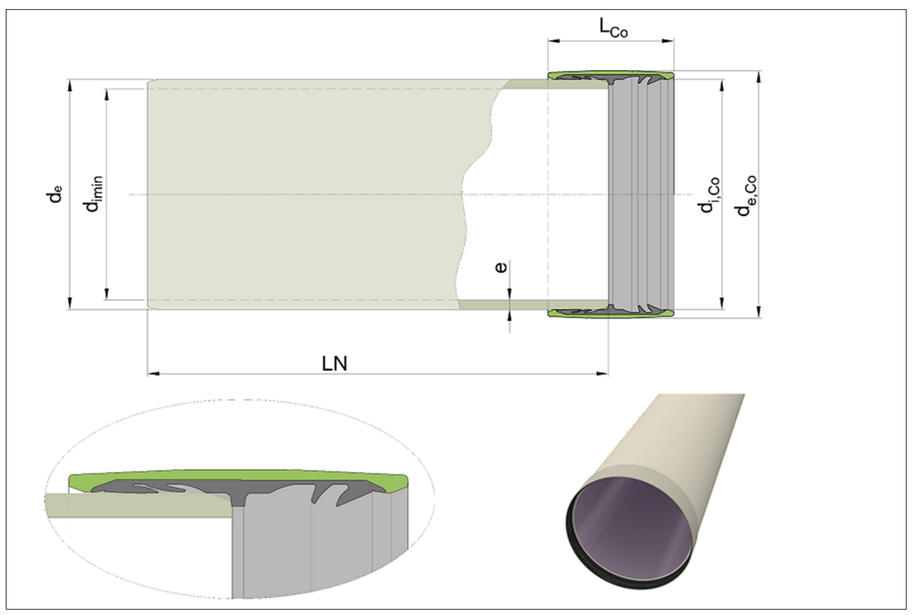


SCALA GRAFICA 1:50
0m 0,50 1,00 1,50 2,00 2,50m

AZIENDA GARDESANA SERVIZI

ags azienda gardesana servizi

"INTERVENTI DI RIQUALIFICAZIONE DEL SISTEMA DI RACCOLTA DEI REFLUI NEL BACINO DEL LAGO DI GARDA - SPONDA VERONESE"
Lotto 1 - Tratto 4 - 2°Stralcio
"OPERE COLLETTORE IN PRESSIONE ED OPERE COMPLEMENTARI TRATTO PERGOLANA - ROCCA VELA - COMUNE BARDOLINO"
Lotto 8 - Tratto 4_OC
CIG: B7E3B750B2 - CUP: J33F17000010002

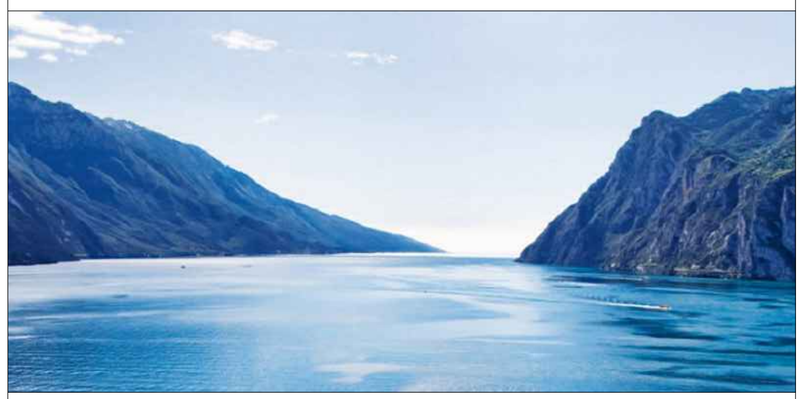

PROGETTO ESECUTIVO

PROGETTISTA E COORDINATORE SICUREZZA IN FASE DI PROGETTO:
Ing. Giovanni Battista Matteotti

COLLABORAZIONE:
Ing. Luca Petracin
Ing. Andrea Martinello
Ing. Emanuele Anderlini
Ing. Filiberto Boscolo Lisetto
Geom. Elisa Zatti

mass INGEGNERIA E ARCHITETTURA SRL.
Via Sorio 33/a, 35141 PADOVA
Tel: 049-7233320 - Mail: info@matteotti.com

RESPONSABILE UNICO DEL PROGETTO:
Dott. Ing. Carlo Alberto Voi

TITOLO	SCALA	CODICE ELABORATO
PARTICOLARI COSTRUTTIVI COLLETTORE FOGNARIO A GRAVITA' PRFV700-800-1000 E BY-PASS A GRAVITA' PEAD DE560	1:50	B-64-001

N° REV	DATA	DESCRIZIONE	ESEGUITO	VERIFICATO	APPROVATO
00	Marzo 2026	PRIMA EMISSIONE	Ing. E. Anderlini	Ing. L. Petracin	Ing. G. B. Matteotti
01	Luglio 2026	AGGIORNAMENTO POST-VERIFICA AGS	Ing. E. Anderlini	Ing. L. Petracin	Ing. G. B. Matteotti
02					
03					
04					