

PIANTA OPERE INTERRATE

SCALA 1:50

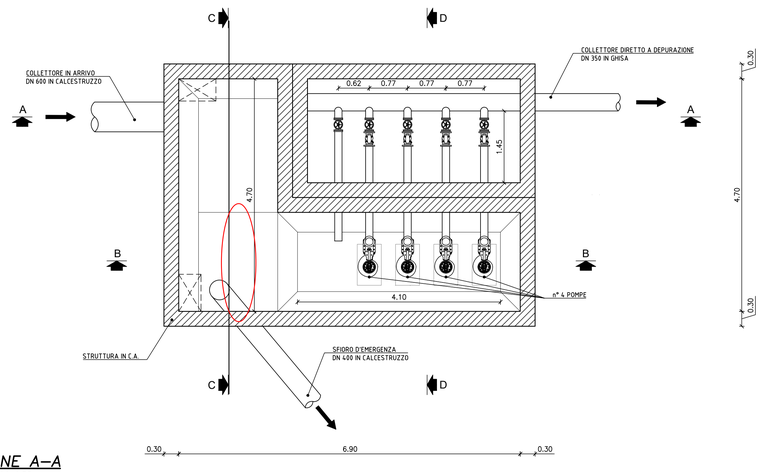


PIANTA COPERTURA

SCALA 1:50

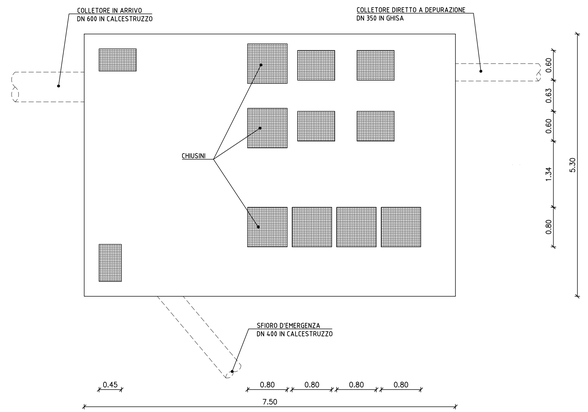


SEZIONE A–A

SCALA 1:50

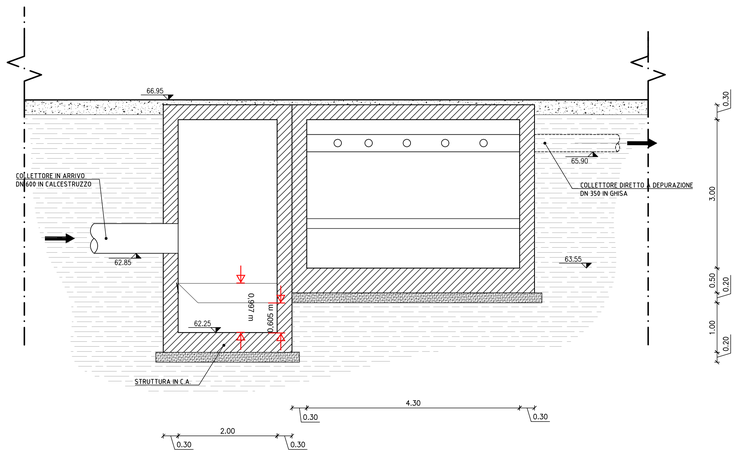


SEZIONE C–C

SCALA 1:50

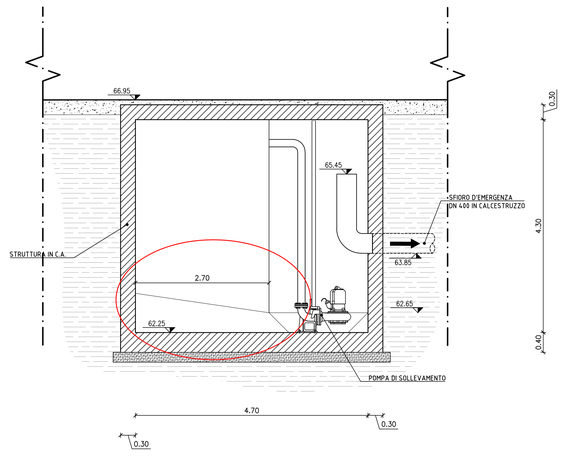


SEZIONE B–B

SCALA 1:50

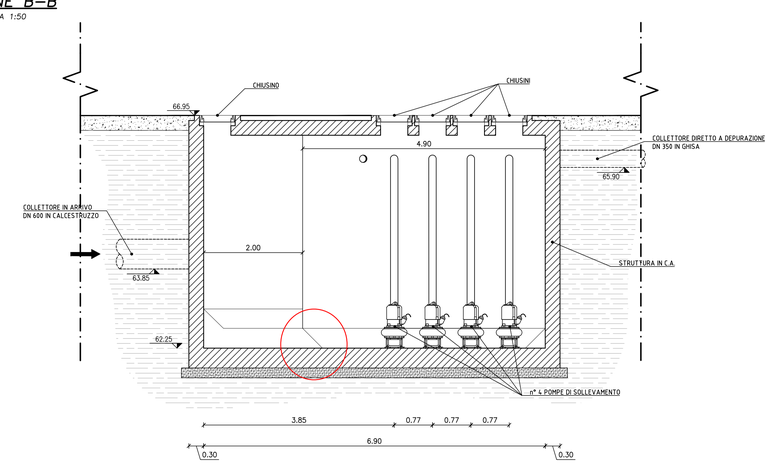


SEZIONE D–D

SCALA 1:50

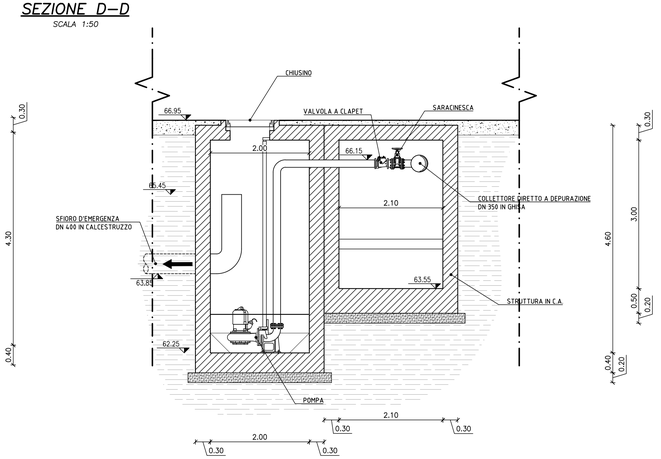


STRALCIO PLANIMETRICO

SCALA 1:500

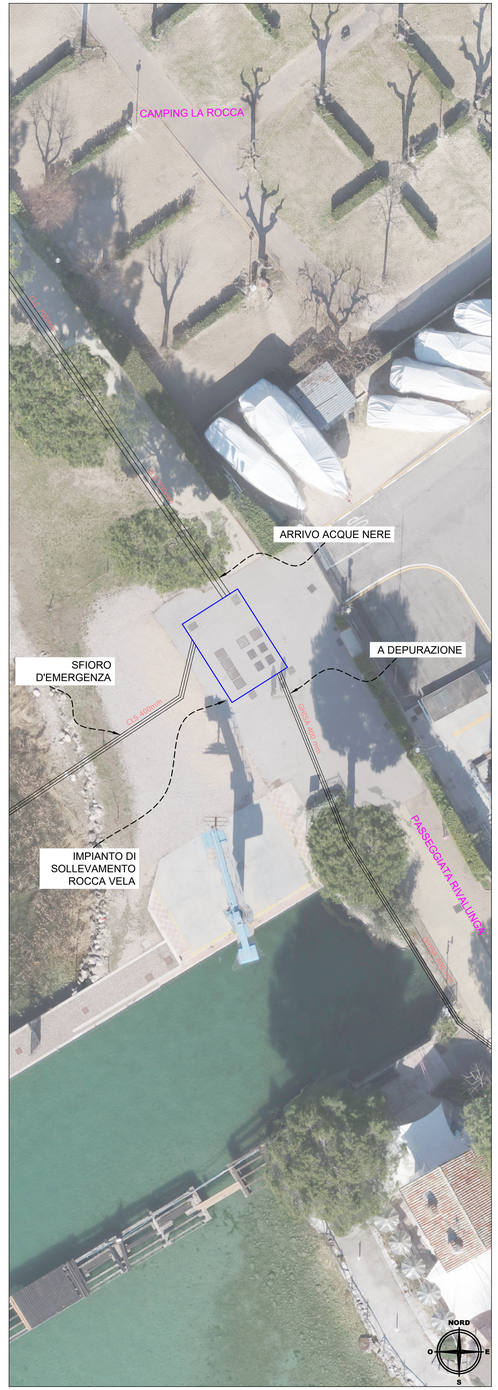

INQUADRAMENTO CATASTALE

SCALA 1:1'000

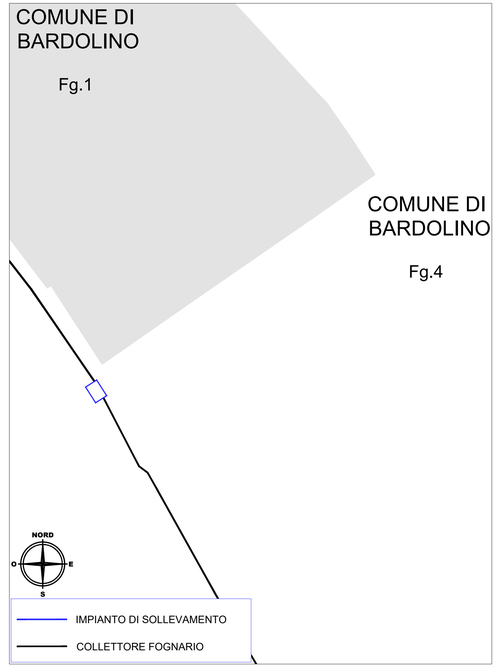

AZIENDA GARDESANA SERVIZI

ags | azienda gardesana servizi

"INTERVENTI DI RIQUALIFICAZIONE DEL SISTEMA DI RACCOLTA DEI REFLUI NEL BACINO DEL LAGO DI GARDA - SPONDA VERONESE"
Lotto 1 - Tratto 4 - 2°Stralcio
"OPERE COLLETTORE IN PRESSIONE ED OPERE COMPLEMENTARI TRATTO PERGOLANA - ROCCA VELA - COMUNE BARDOLINO"
Lotto 8 - Tratto 4_OC

CIG: B7E3B750B2 - CUP: J33F17000010002



PROGETTO ESECUTIVO

PROGETTISTA E COORDINATORE SICUREZZA IN FASE DI PROGETTO:
Ing. Giovanni Battista Matteotti

COLLABORAZIONE:
Ing. Luca Petracin
Ing. Andrea Martinello
Ing. Emanuele Anderlini
Ing. Filiberto Boscolo Lisetto
Geom. Elisa Zatti

mass INGEGNERIA E ARCHITETTURA SRL
Via Boito 30/a, 35141 PADOVA
Tel. 049-723320 - Mail: info@matteotti.com

RESPONSABILE UNICO DEL PROGETTO:
Dott. Ing. Carlo Alberto Voi

TITOLO			SCALA	CODICE ELABORATO
IMPIANTO DI SOLLEVAMENTO ESISTENTE DI ROCCA VELA PIANTA E SEZIONI			1:50	B-67-000
N° REV	DATA	DESCRIZIONE	ESEGUITO	VERIFICATO	APPROVATO
00	Marzo 2026	PRIMA EMISSIONE	Ing. E. Anderlini	Ing. L. Petracin	Ing. G. B. Matteotti
01					
02					
03					
04					