PIANTA OPERE INTERRATE

SCALA 1:50

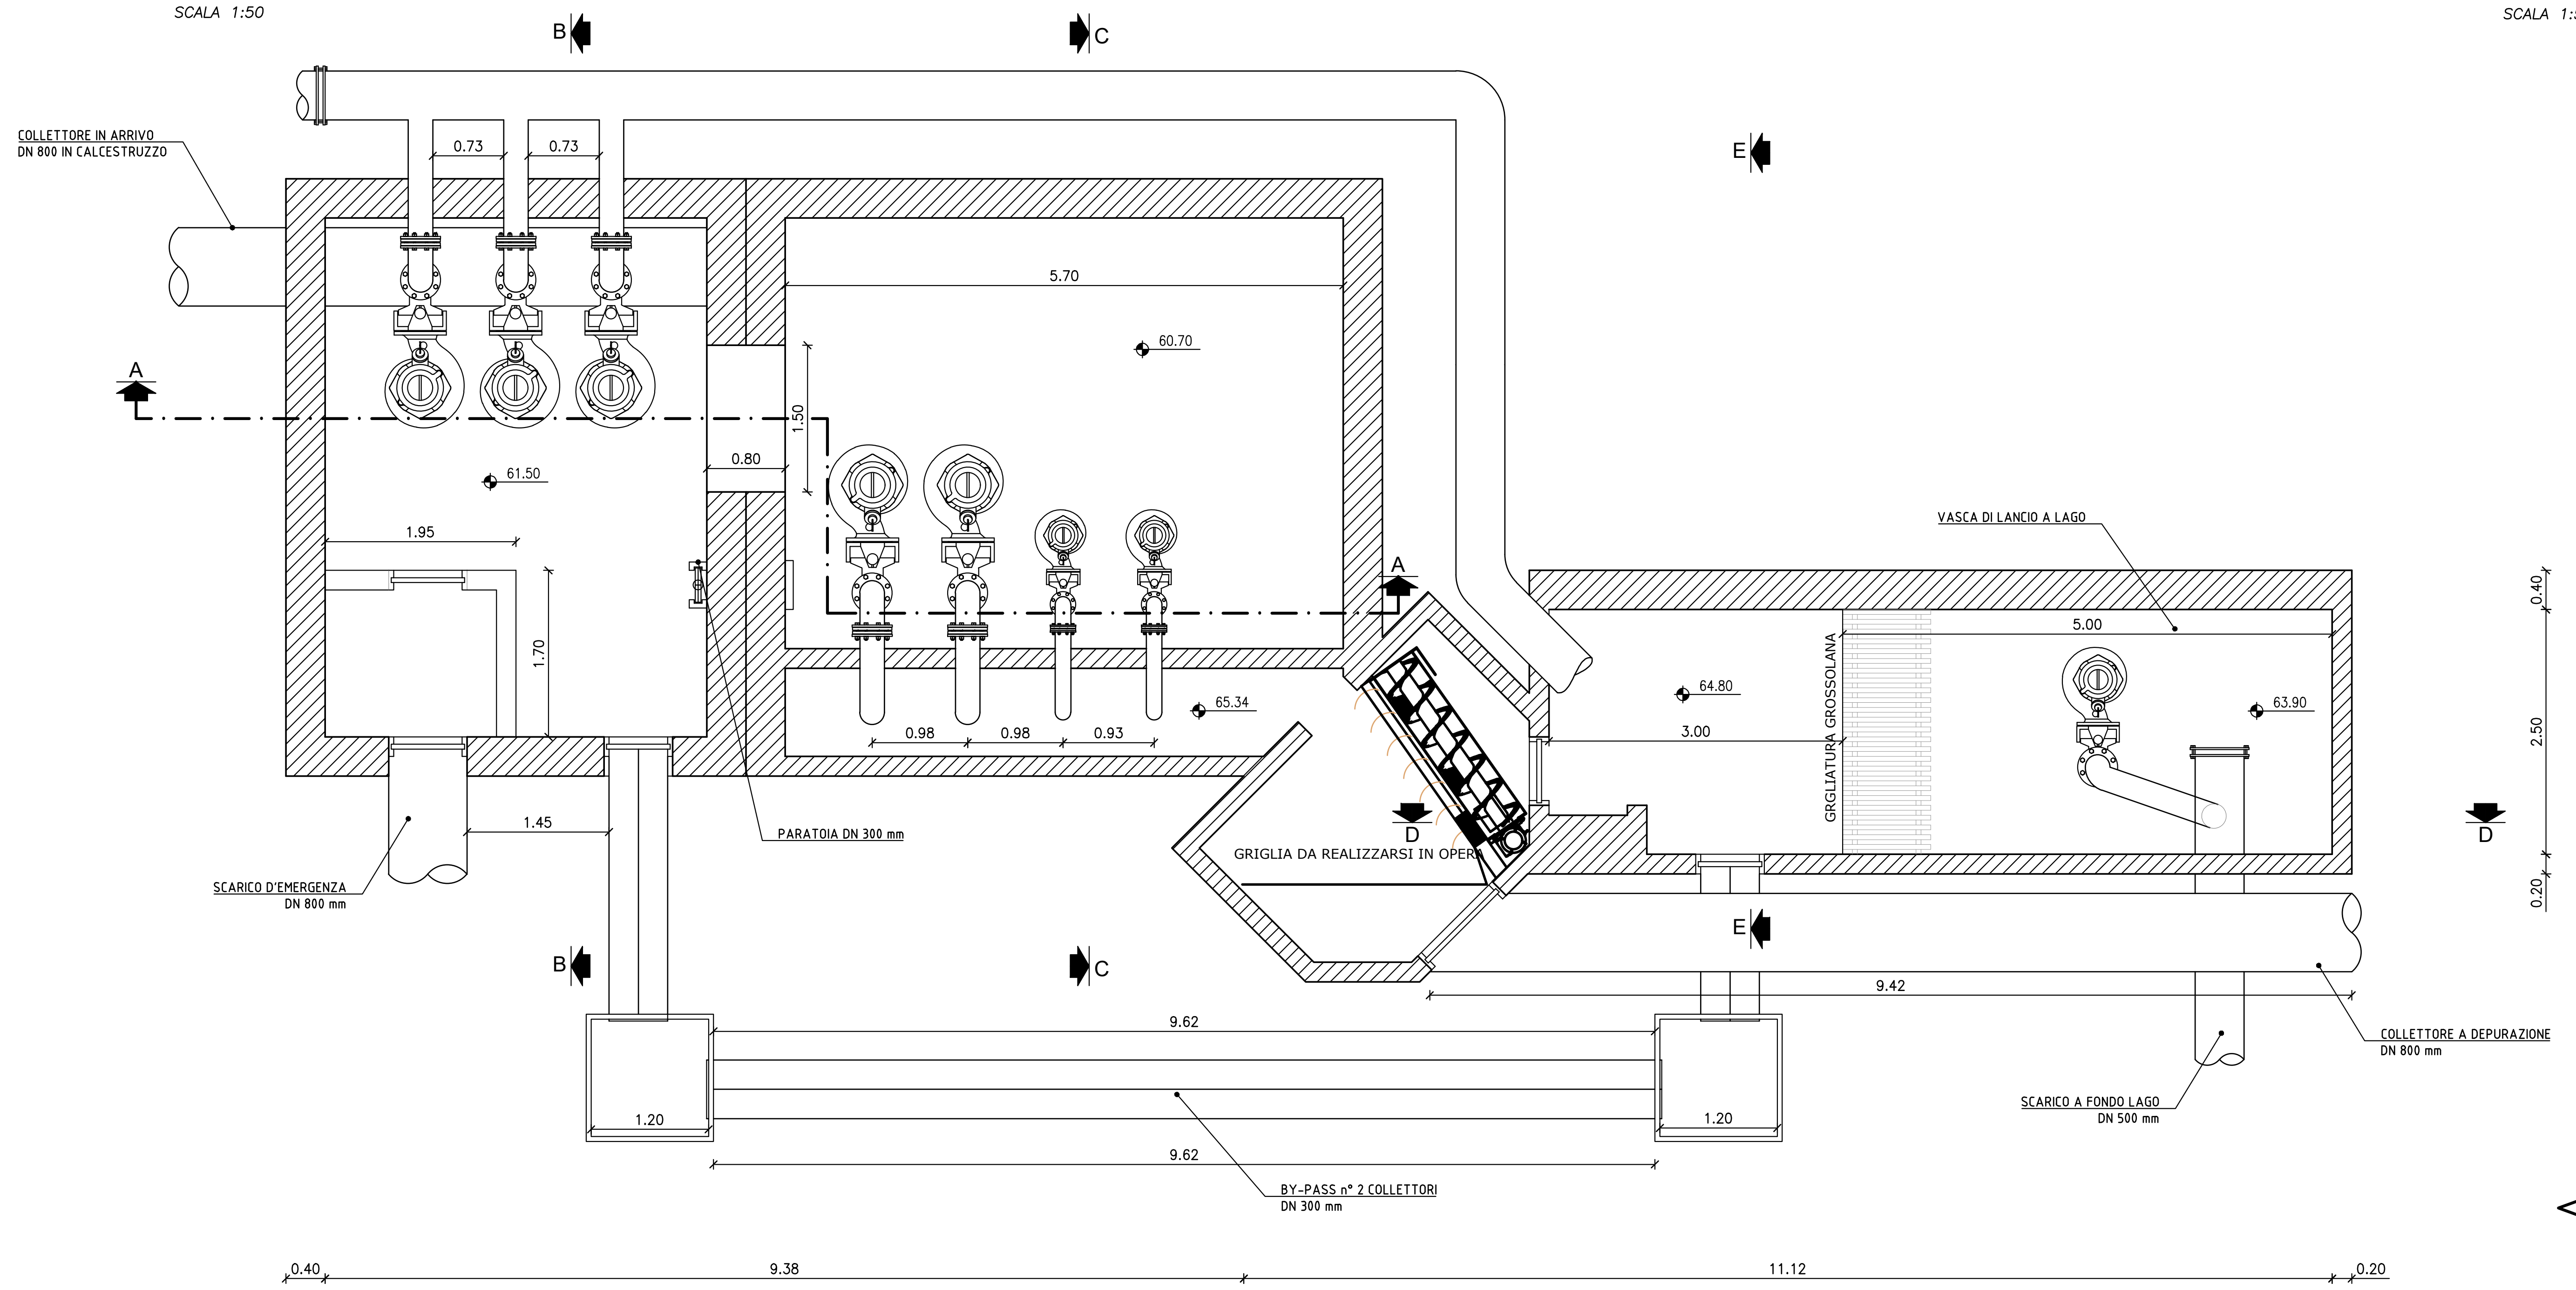
B
C
E
A
D
COLLETTORE IN ARRIVO
DN 800 IN CALCESTRUZZO
0.73
0.73
5.70
60.70
1.50
0.80
61.50
1.95
1.70
65.34
0.98
0.98
0.93
PARATOIA DN 300 mm
SCARICO D'EMERGENZA
DN 800 mm
1.45
GRIGLIA DA REALIZZARSI IN OPERA
VASCA DI LANCIO A LAGO
5.00
64.80
3.00
GRGLIATURA GROSSOLANA
63.90
0.40
2.50
0.20
9.42
COLLETTORE A DEPURAZIONE
DN 800 mm
SCARICO A FONDO LAGO
DN 500 mm
9.62
1.20
9.62
1.20
BY-PASS n° 2 COLLETTORI
DN 300 mm
0.40
9.38
11.12
0.20

SEZIONE A–A

SCALA 1:50

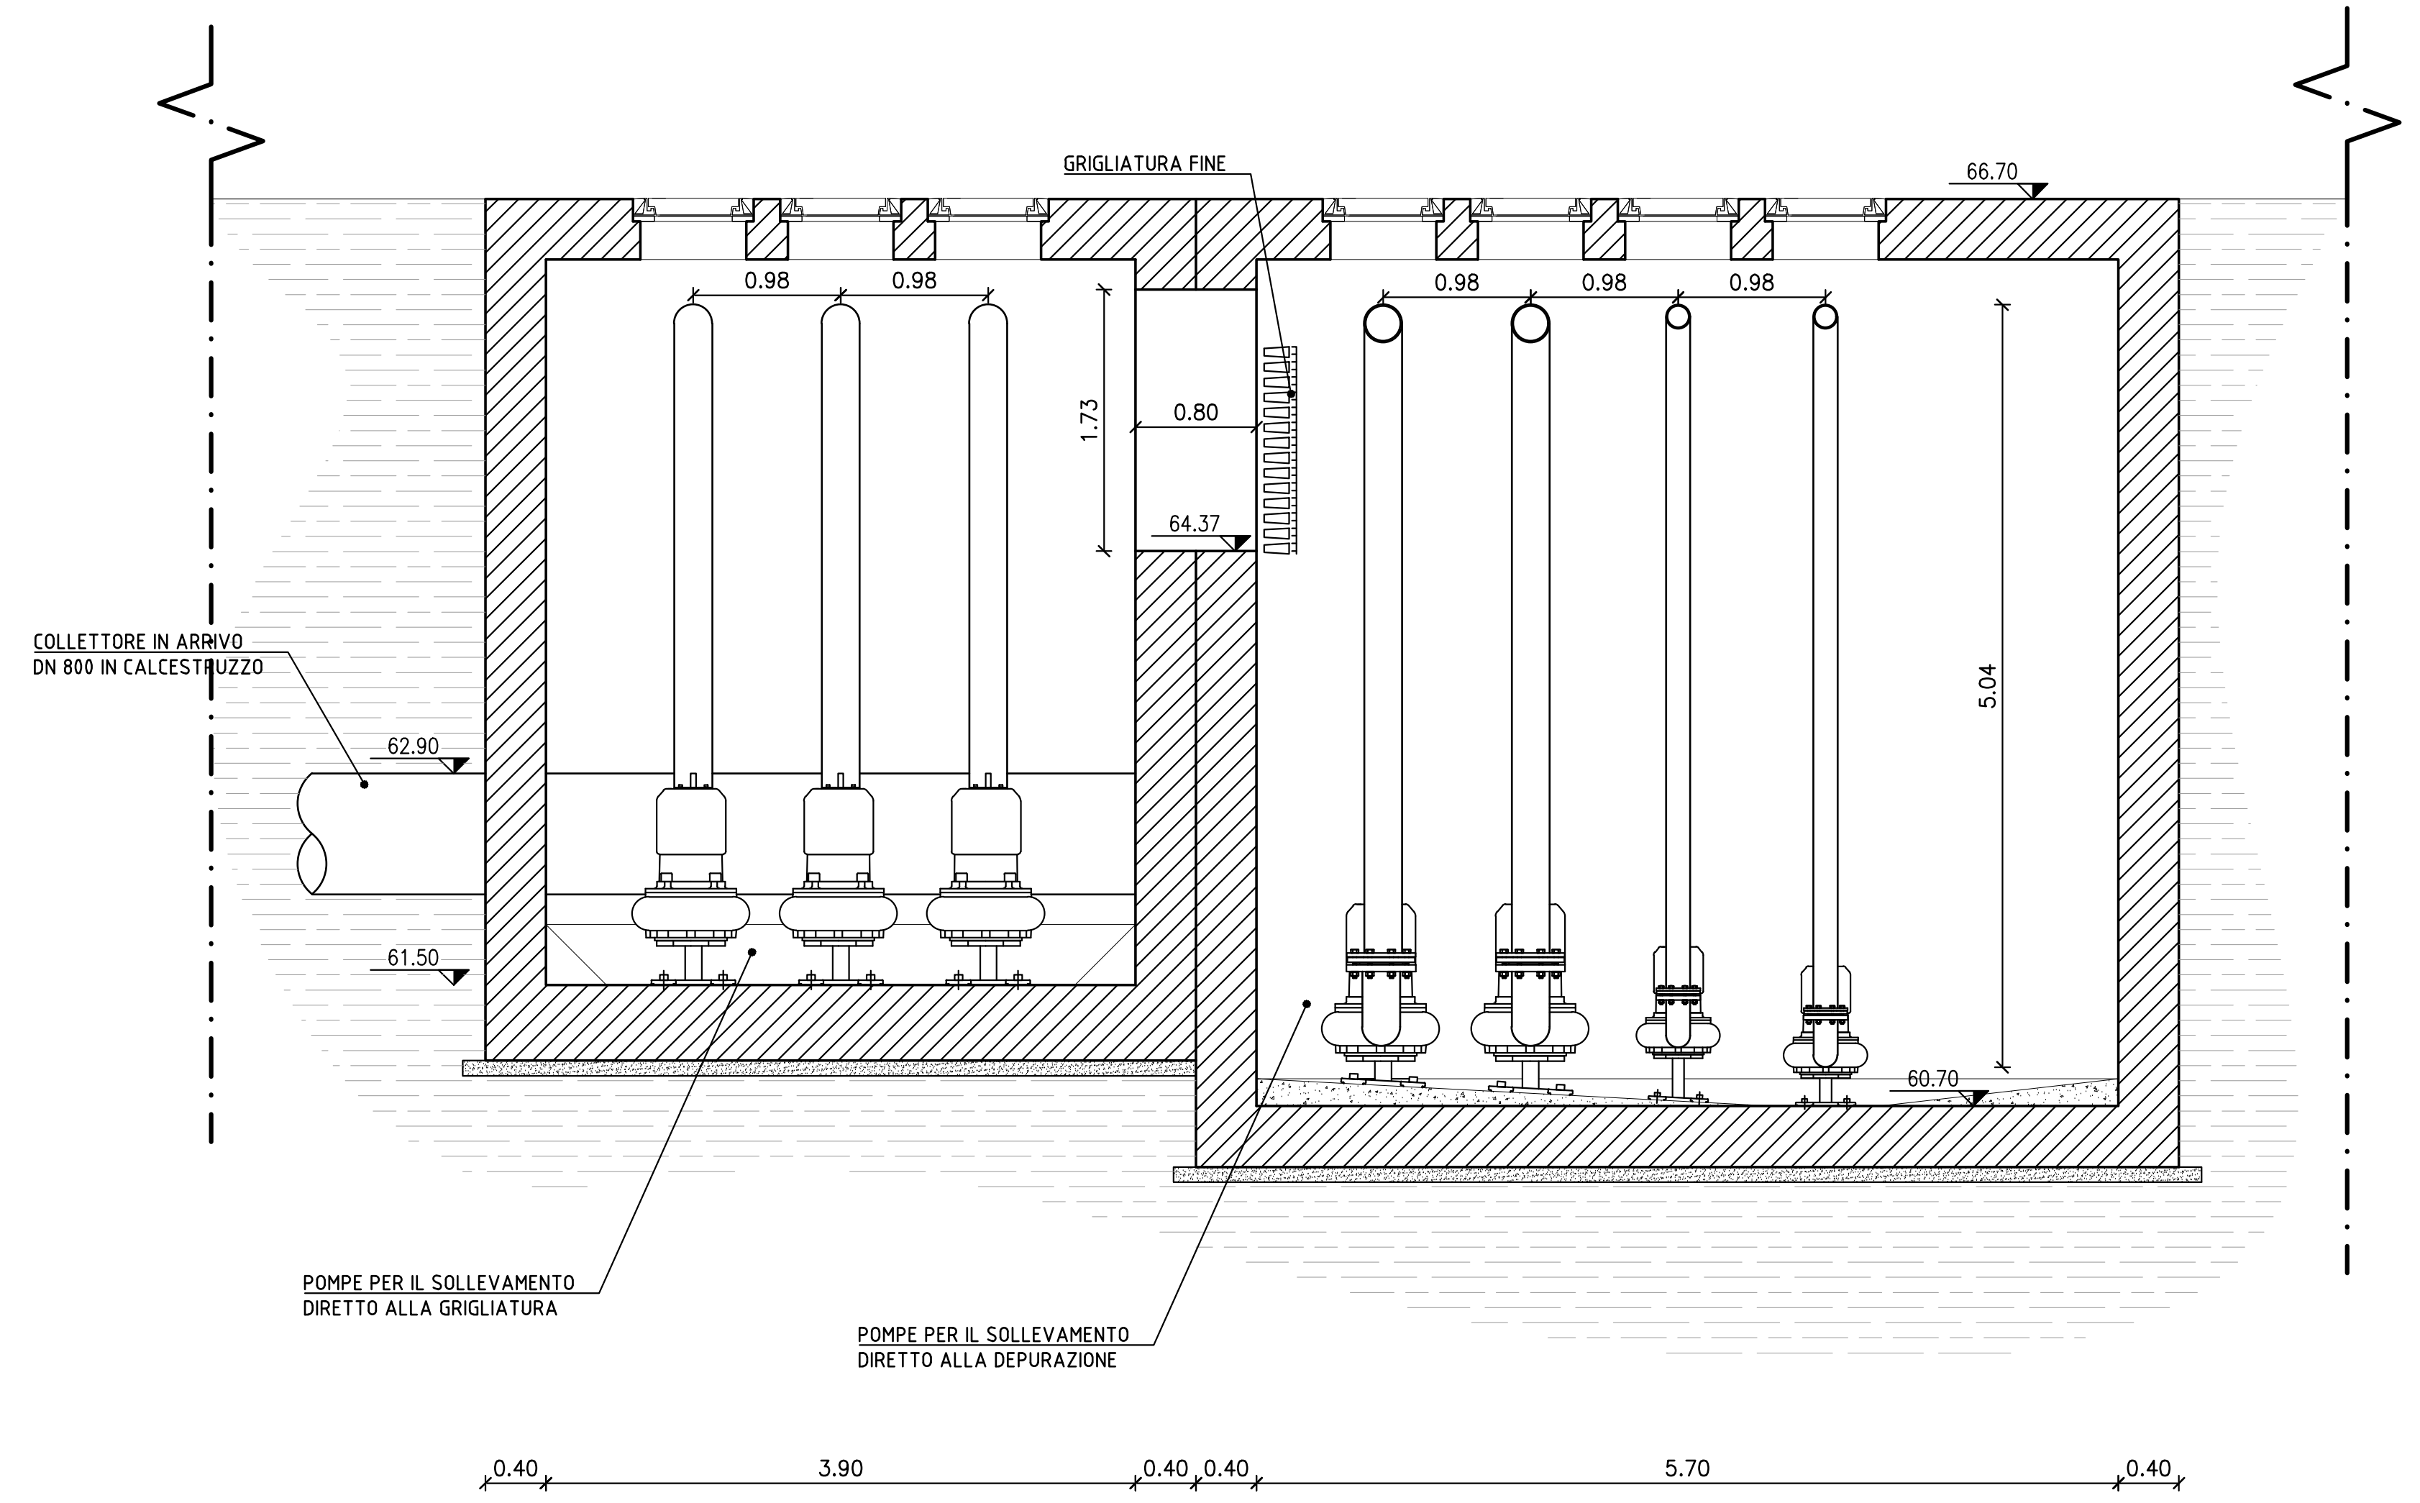
GRIGLIATURA FINE
66.70
0.98
0.98
0.98
0.98
0.98
1.73
0.80
64.37
5.04
0.40
5.60
0.40
COLLETTORE IN ARRIVO
DN 800 IN CALCESTRUZZO
62.90
61.50
60.70
POMPE PER IL SOLLEVAMENTO
DIRETTO ALLA GRIGLIATURA
POMPE PER IL SOLLEVAMENTO
DIRETTO ALLA DEPURAZIONE
0.40
3.90
0.40
0.40
5.70
0.40

SEZIONE E–E

SCALA 1:50

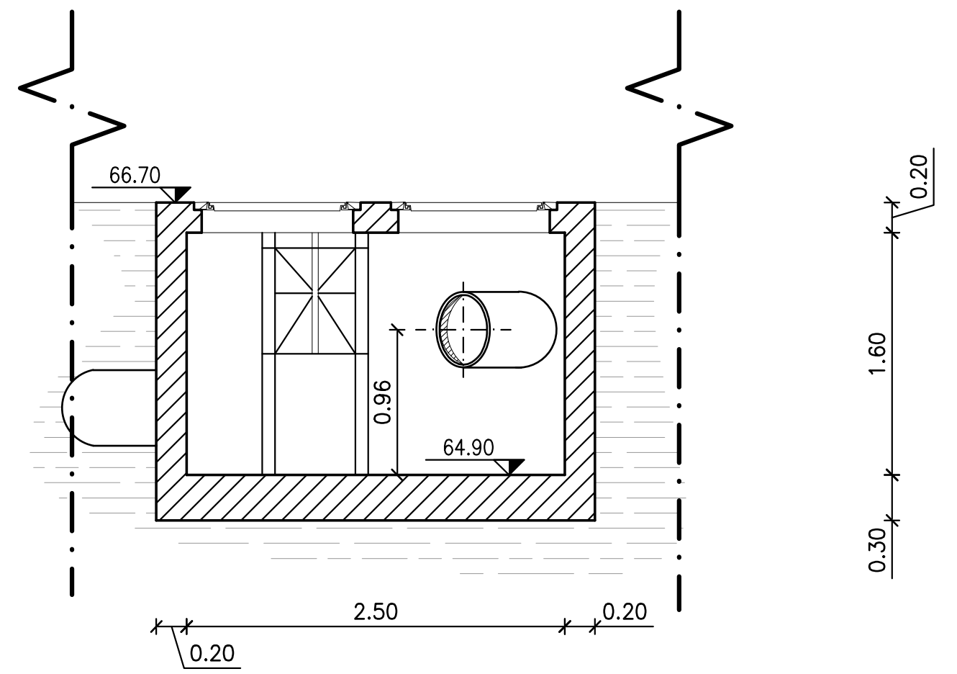
66.70
0.20
1.60
0.96
64.90
0.30
0.20
2.50
0.20

SEZIONE B–B

SCALA 1:50

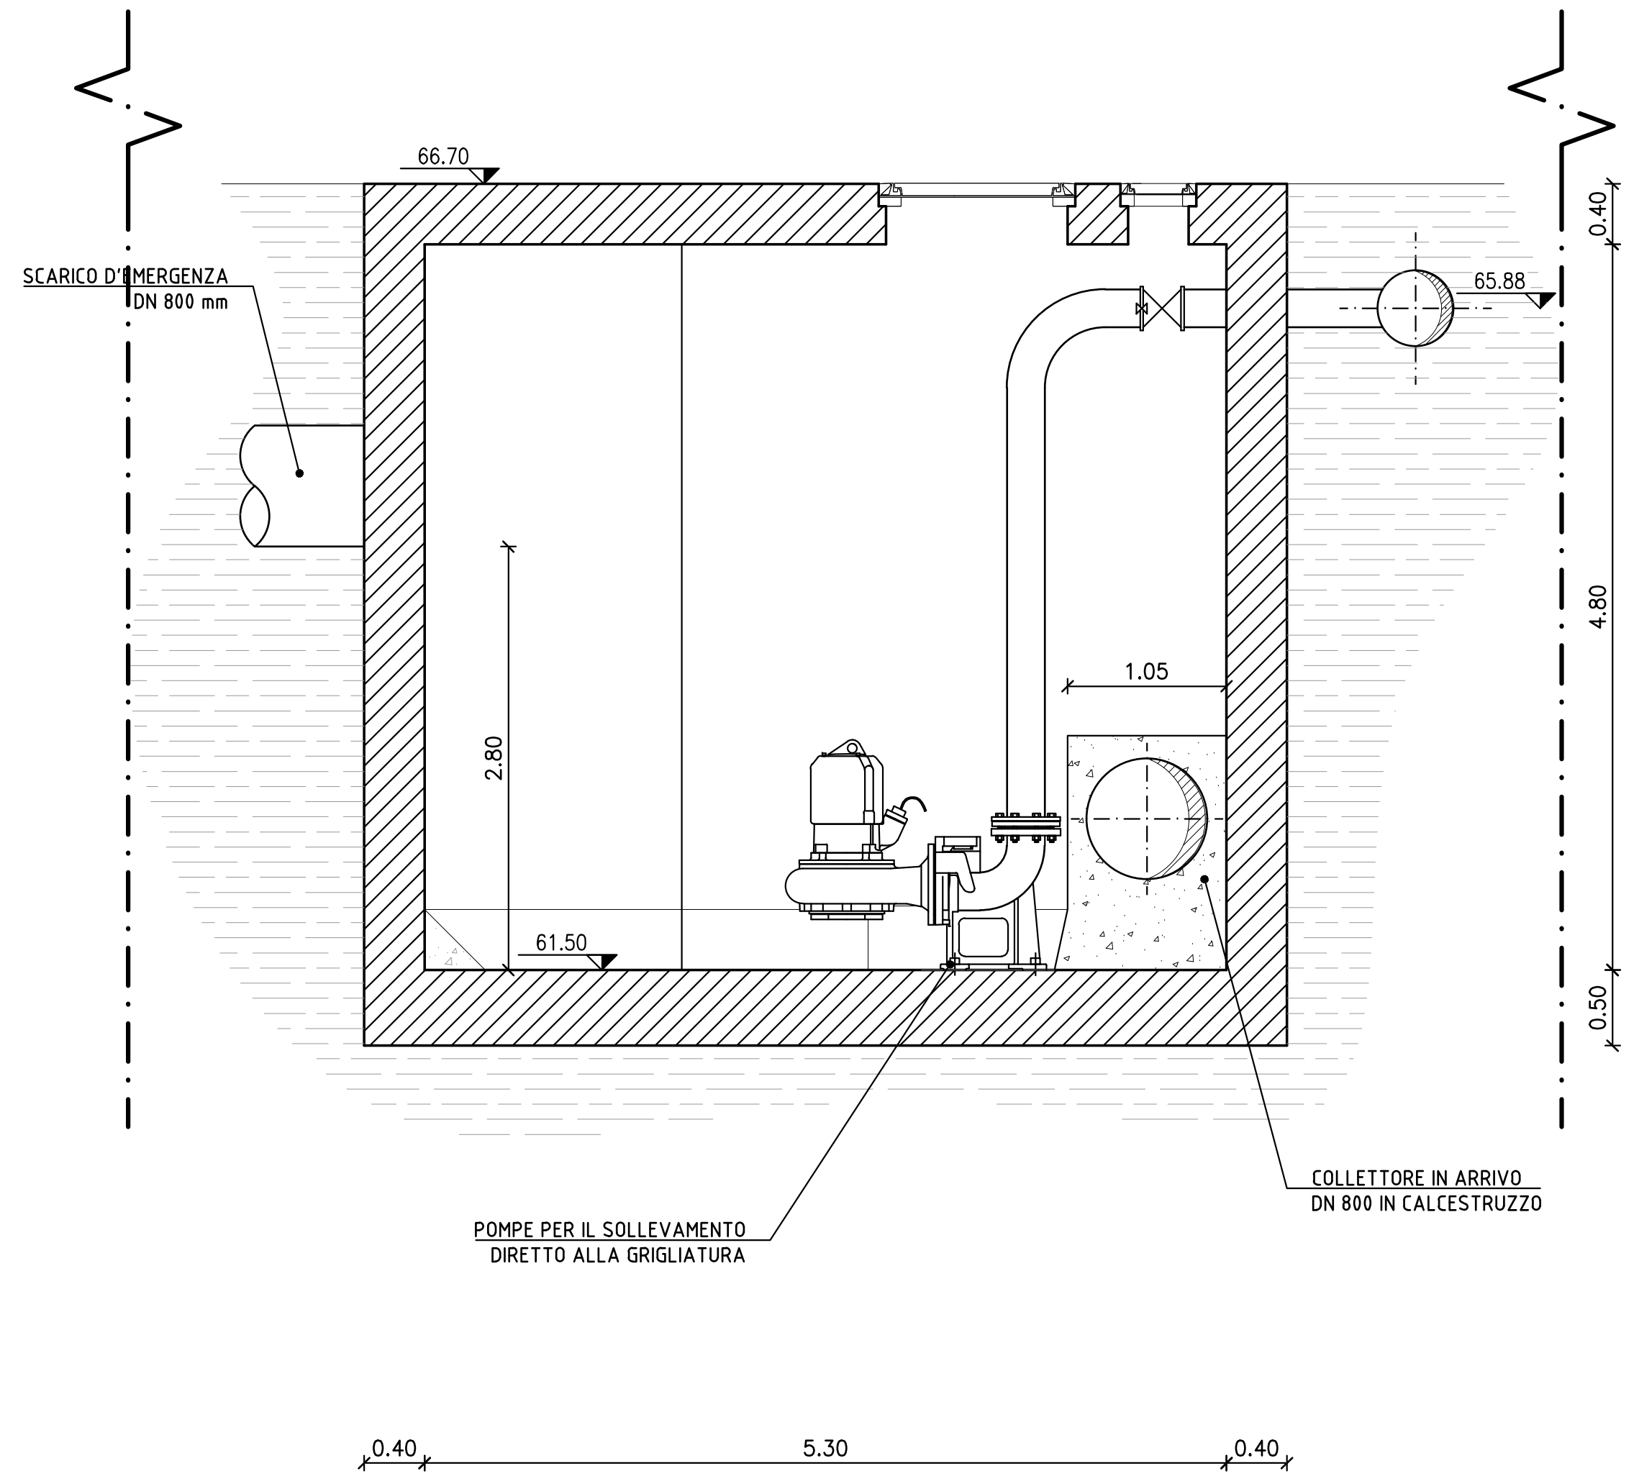
66.70
SCARICO D'EMERGENZA
DN 800 mm
65.88
0.40
4.80
0.50
1.05
2.80
61.50
POMPE PER IL SOLLEVAMENTO
DIRETTO ALLA GRIGLIATURA
COLLETTORE IN ARRIVO
DN 800 IN CALCESTRUZZO
0.40
5.30
0.40

SEZIONE C–C

SCALA 1:50

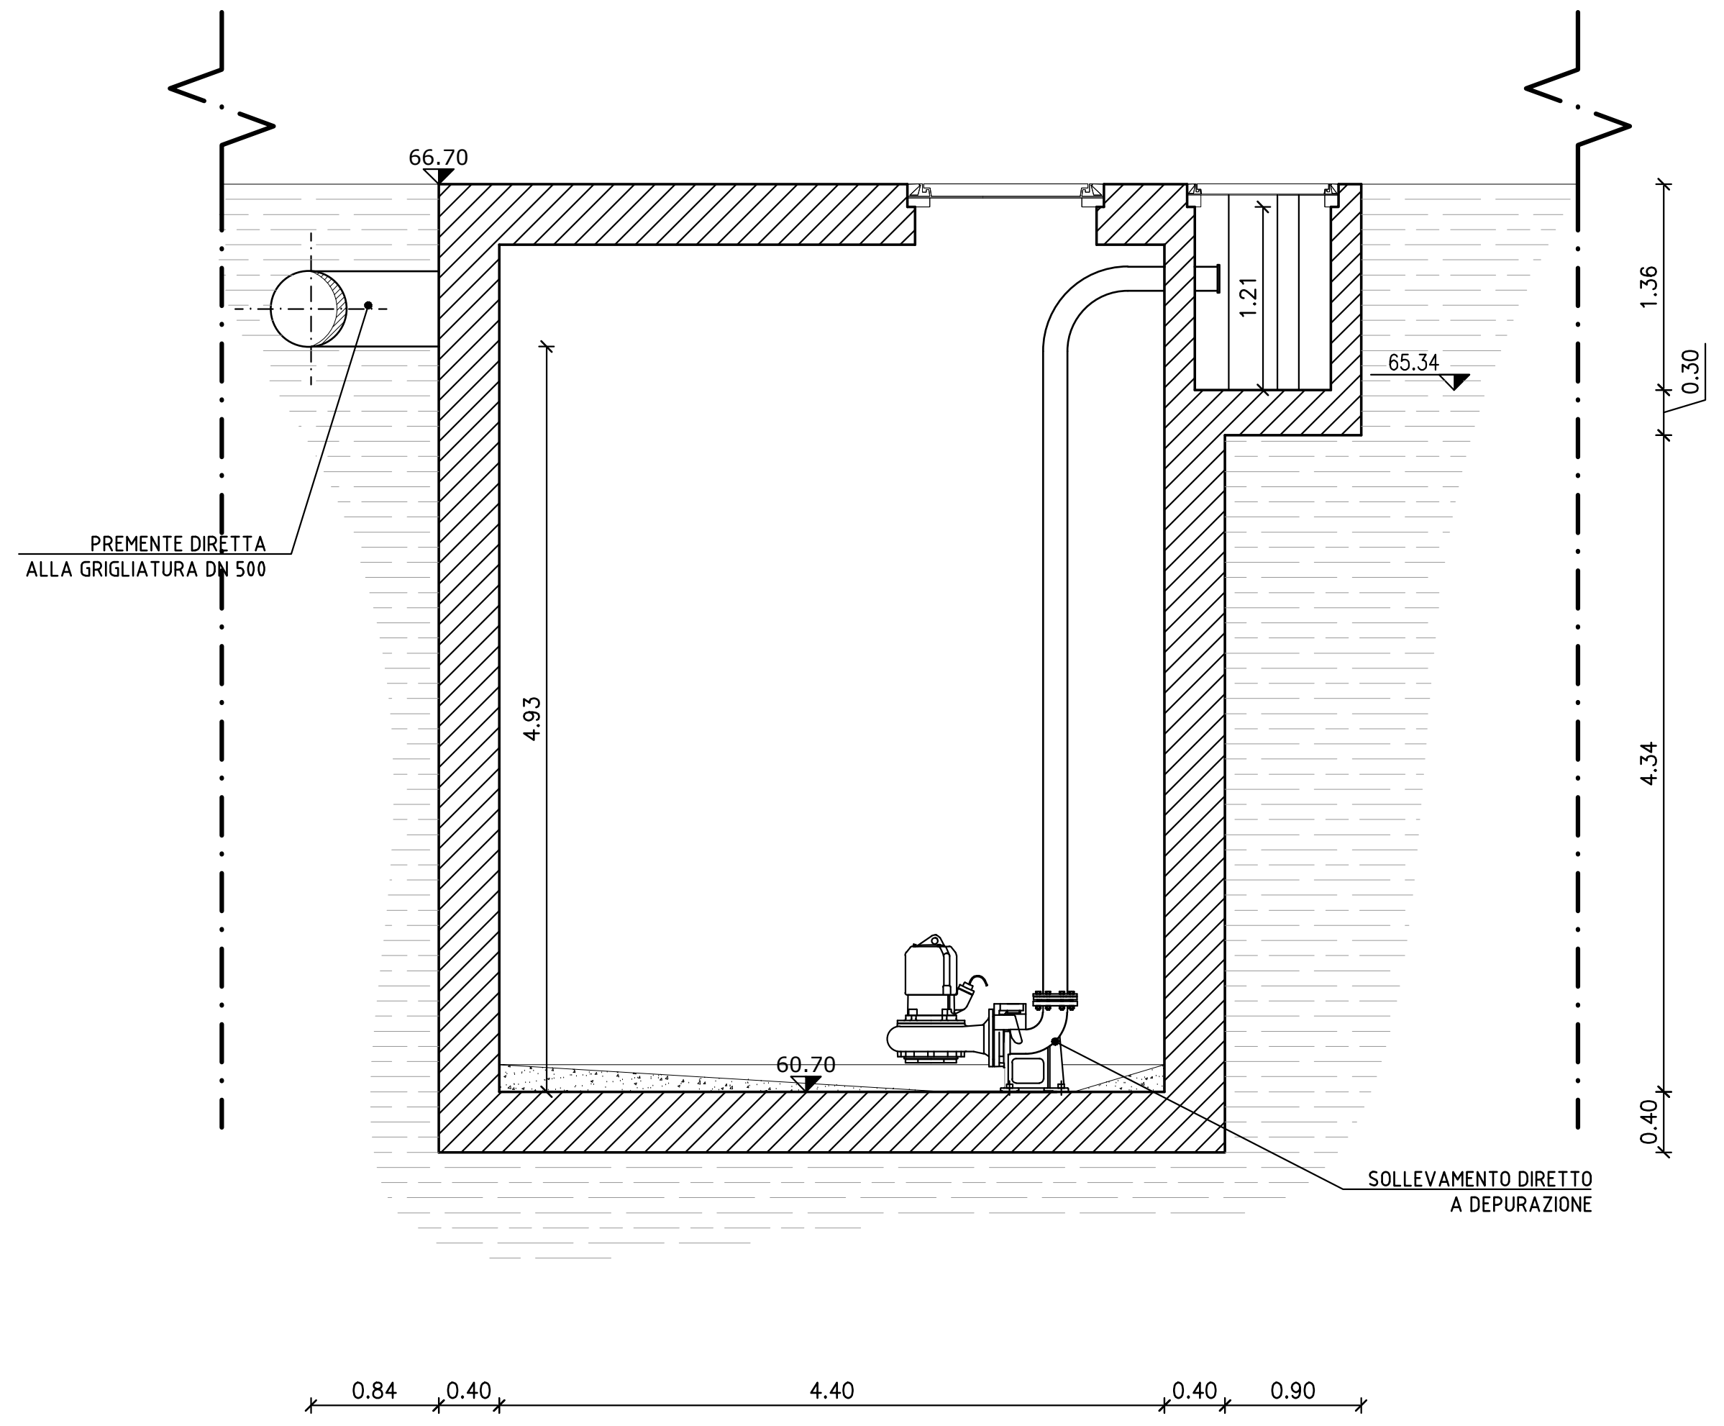
66.70
1.21
65.34
1.36
0.30
PREMENTE DIRETTA
ALLA GRIGLIATURA DN 500
4.93
4.34
60.70
0.40
SOLLEVAMENTO DIRETTO
A DEPURAZIONE
0.84
0.40
4.40
0.40
0.90

SEZIONE D–D

SCALA 1:50

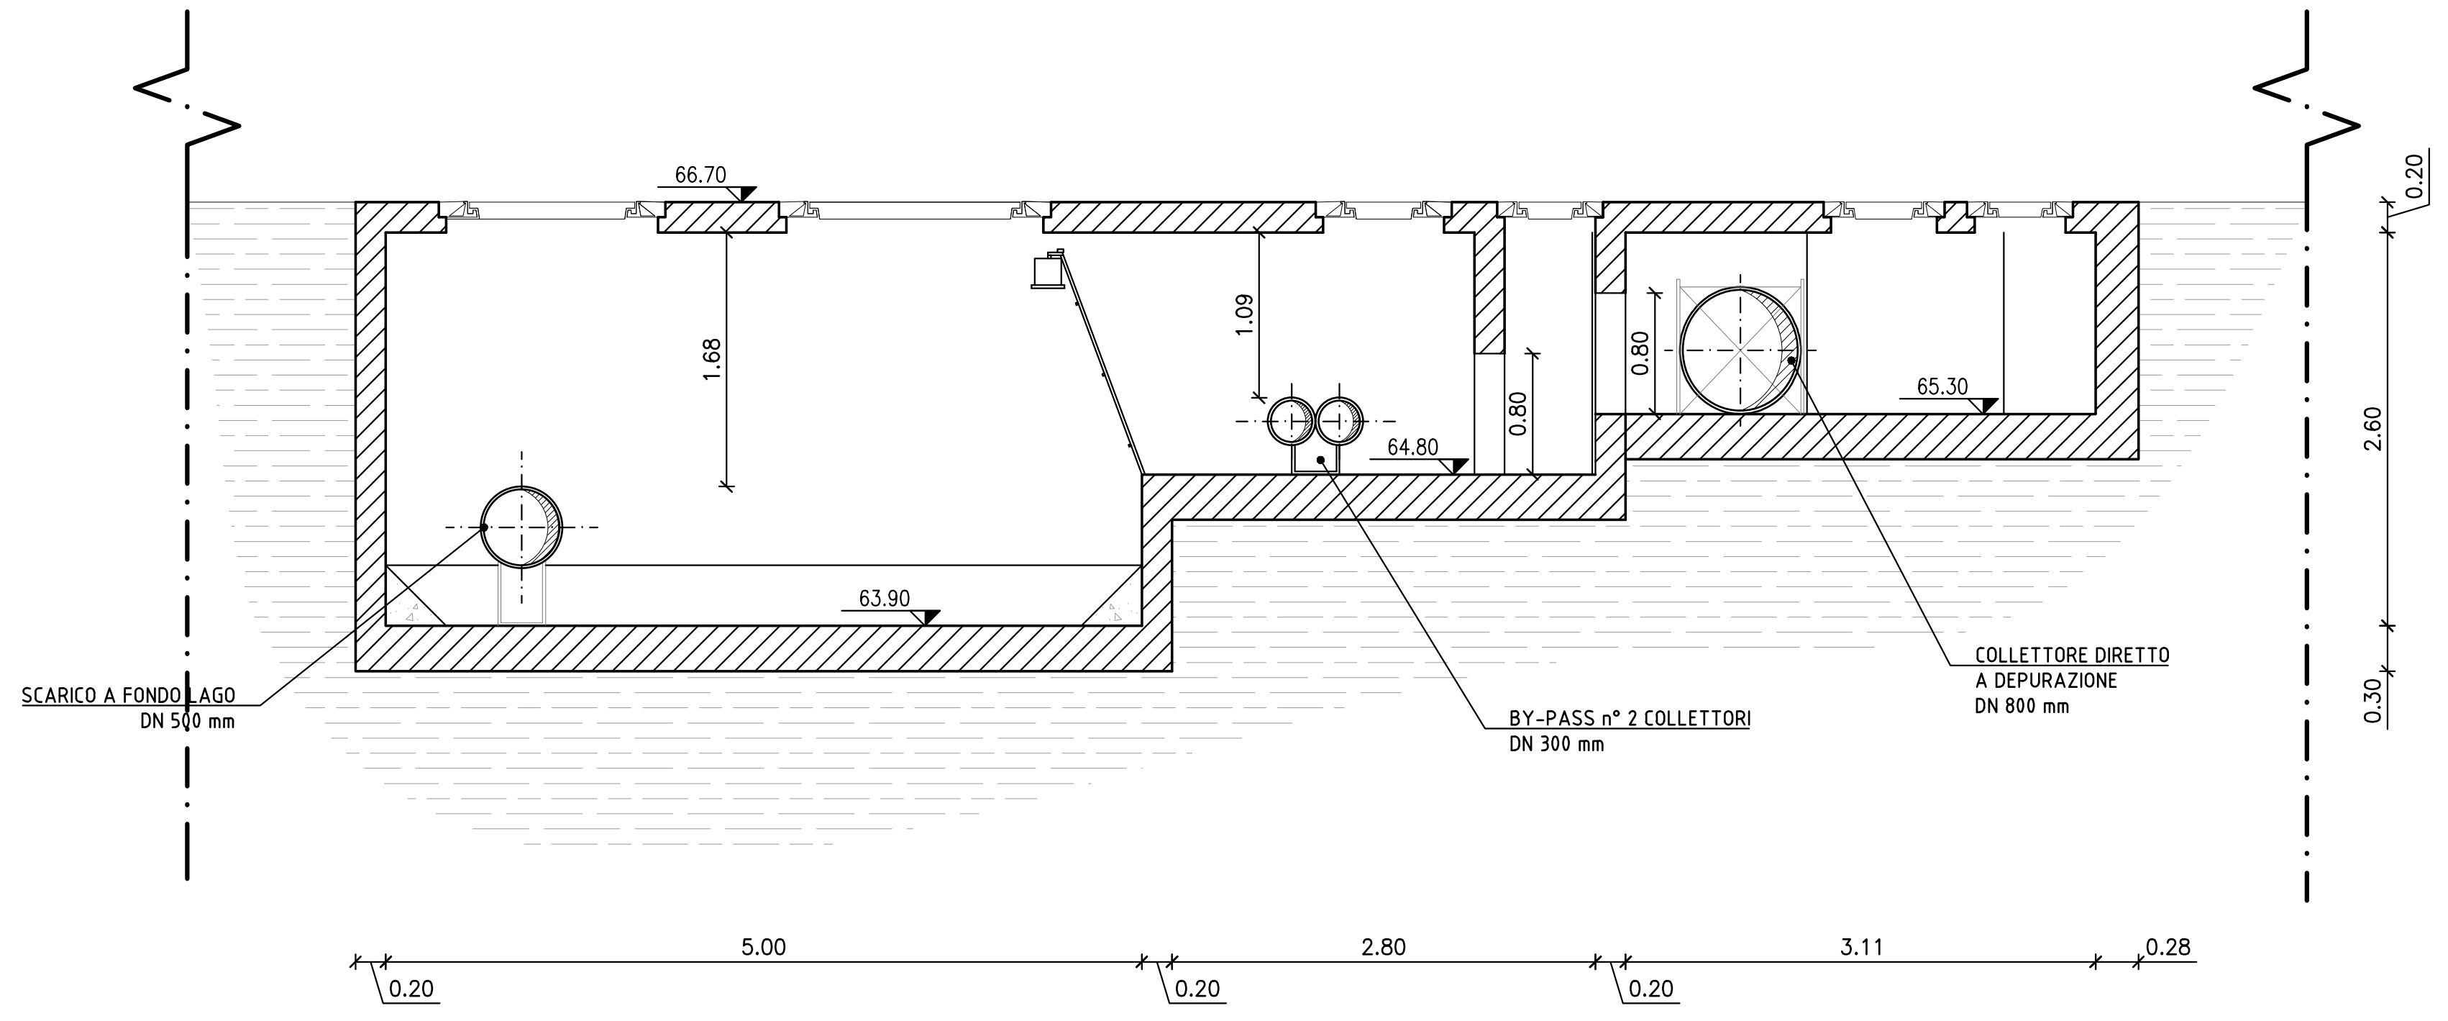
66.70
1.68
1.09
0.80
0.80
64.80
65.30
63.90
0.20
1.20
2.60
0.30
0.30
SCARICO A FONDO LAGO
DN 500 mm
BY-PASS n° 2 COLLETTORI
DN 300 mm
COLLETTORE DIRETTO
A DEPURAZIONE
DN 800 mm
5.00
2.80
3.11
0.28
0.20
0.20
0.20

STRALCIO PLANIMETRICO

SCALA 1:500

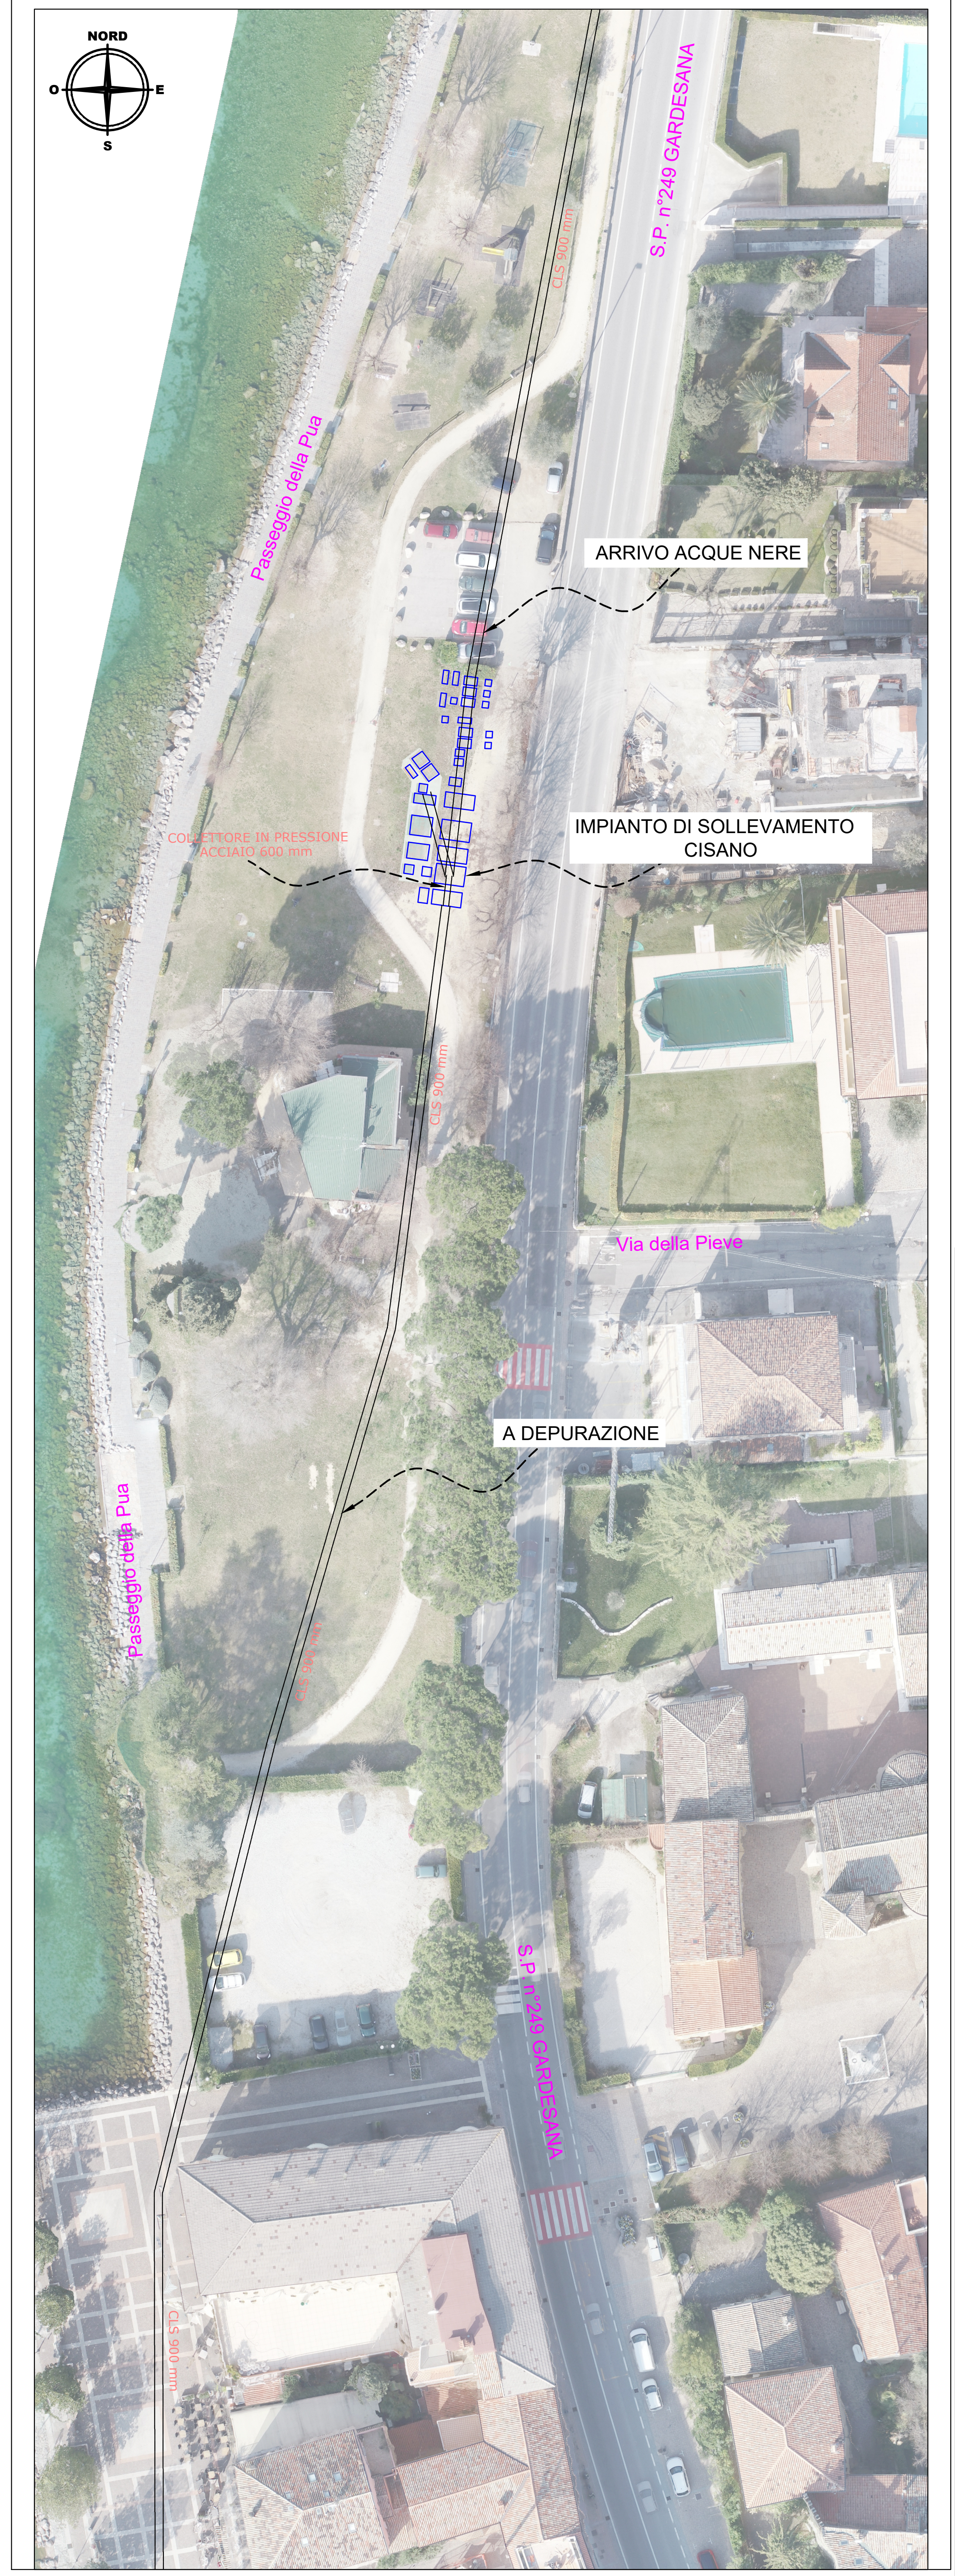
NORD
O
E
S
S.P. n°249 GARDESANA
Passeggio della Pua
CLS 900 mm
ARRIVO ACQUE NERE
IMPIANTO DI SOLLEVAMENTO
CISANO
COLLETTORE IN PRESSIONE
ACCIAIO 600 mm
Via della Pieve
A DEPURAZIONE
Passeggio della Pua

AZIENDA GARDESANA SERVIZI

"INTERVENTI DI RIQUALIFICAZIONE DEL SISTEMA DI RACCOLTA DEI REFLUI NEL BACINO DEL LAGO DI GARDA - SPONDA VERONESE"
Lotto 1 - Tratto 4 - 2°Stralcio
"OPERE COLLETTORE IN PRESSIONE ED OPERE COMPLEMENTARI TRATTO PERGOLANA - ROCCA VELA - COMUNE BARDOLINO"
Lotto 8 - Tratto 4_OC
CIG: B7E3B750B2 - CUP: J33F17000010002

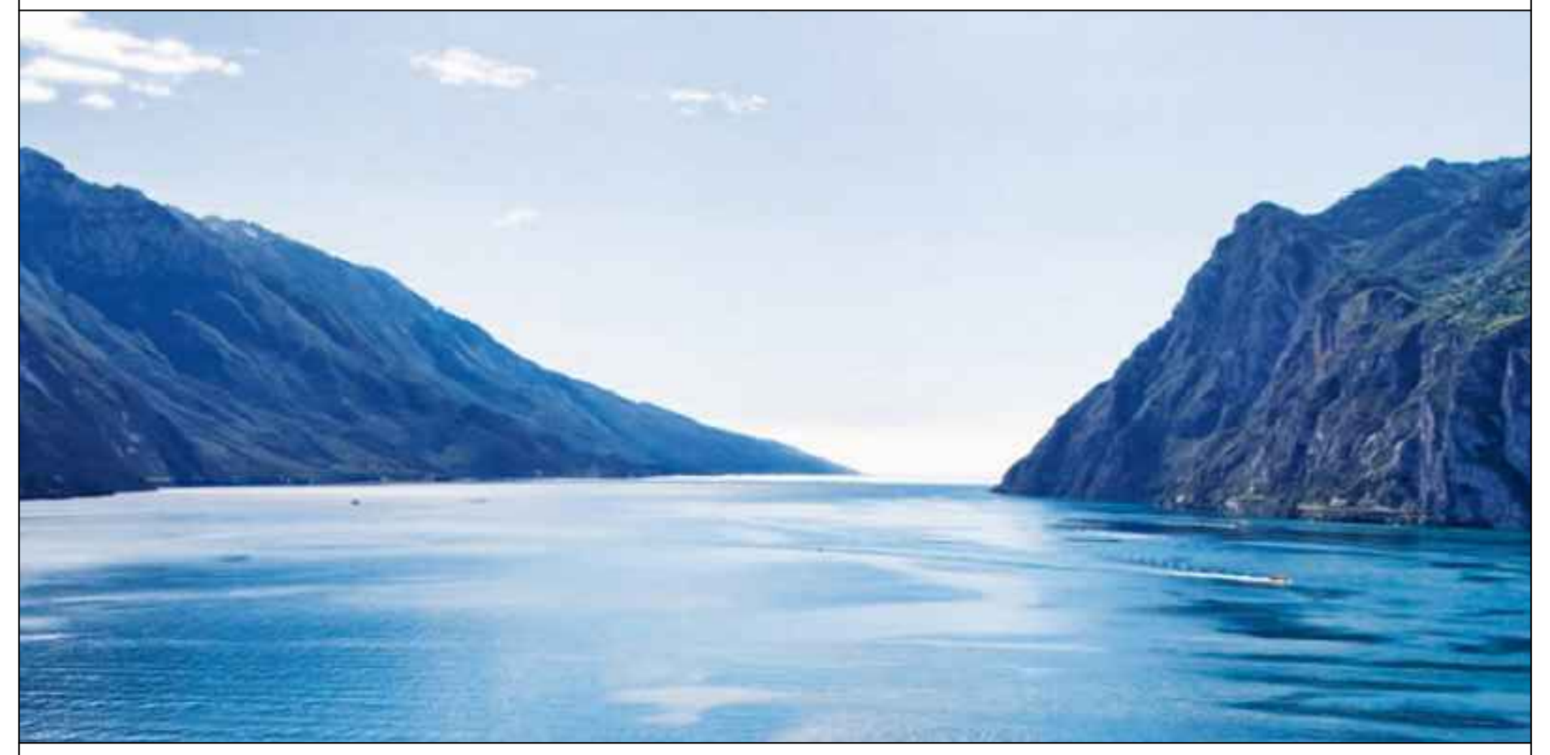

PROGETTO ESECUTIVO

PROGETTISTA E COORDINATORE SICUREZZA IN FASE DI PROGETTO:
Ing. Giovanni Battista Matteotti

COLLABORAZIONE:
Ing. Luca Petracin
Ing. Andrea Martinello
Ing. Emanuele Anderlini
Ing. Filiberto Boscolo Lisetto
Geom. Elisa Zatti

mass
INGEGNERIA E ARCHITETTURA SRL
Via Sorio 33/a, 35141 PADOVA
Tel: 049-723320 - Mail: Info@matteotti.com

ING.
G.B. MATTEOTTI

RESPONSABILE UNICO DEL PROGETTO:
Dott. Ing. Carlo Alberto Voi

TITOLO	*SCALA*	*CODICE ELABORATO*
IMPIANTO DI SOLLEVAMENTO ESISTENTE DI CISANO - PIANTA E SEZIONI	varie	B-69-000

N° REV	*DATA*	*DESCRIZIONE*	*ESEGUITO*	*VERIFICATO*	*APPROVATO*
00	Marzo 2026	PRIMA EMISSIONE	Ing. E. Anderlini	Ing. L. Petracin	Ing. G. B. Matteotti
01					
02					
03					
04					