

PLANIMETRIA GENERALE SCALA 1:100

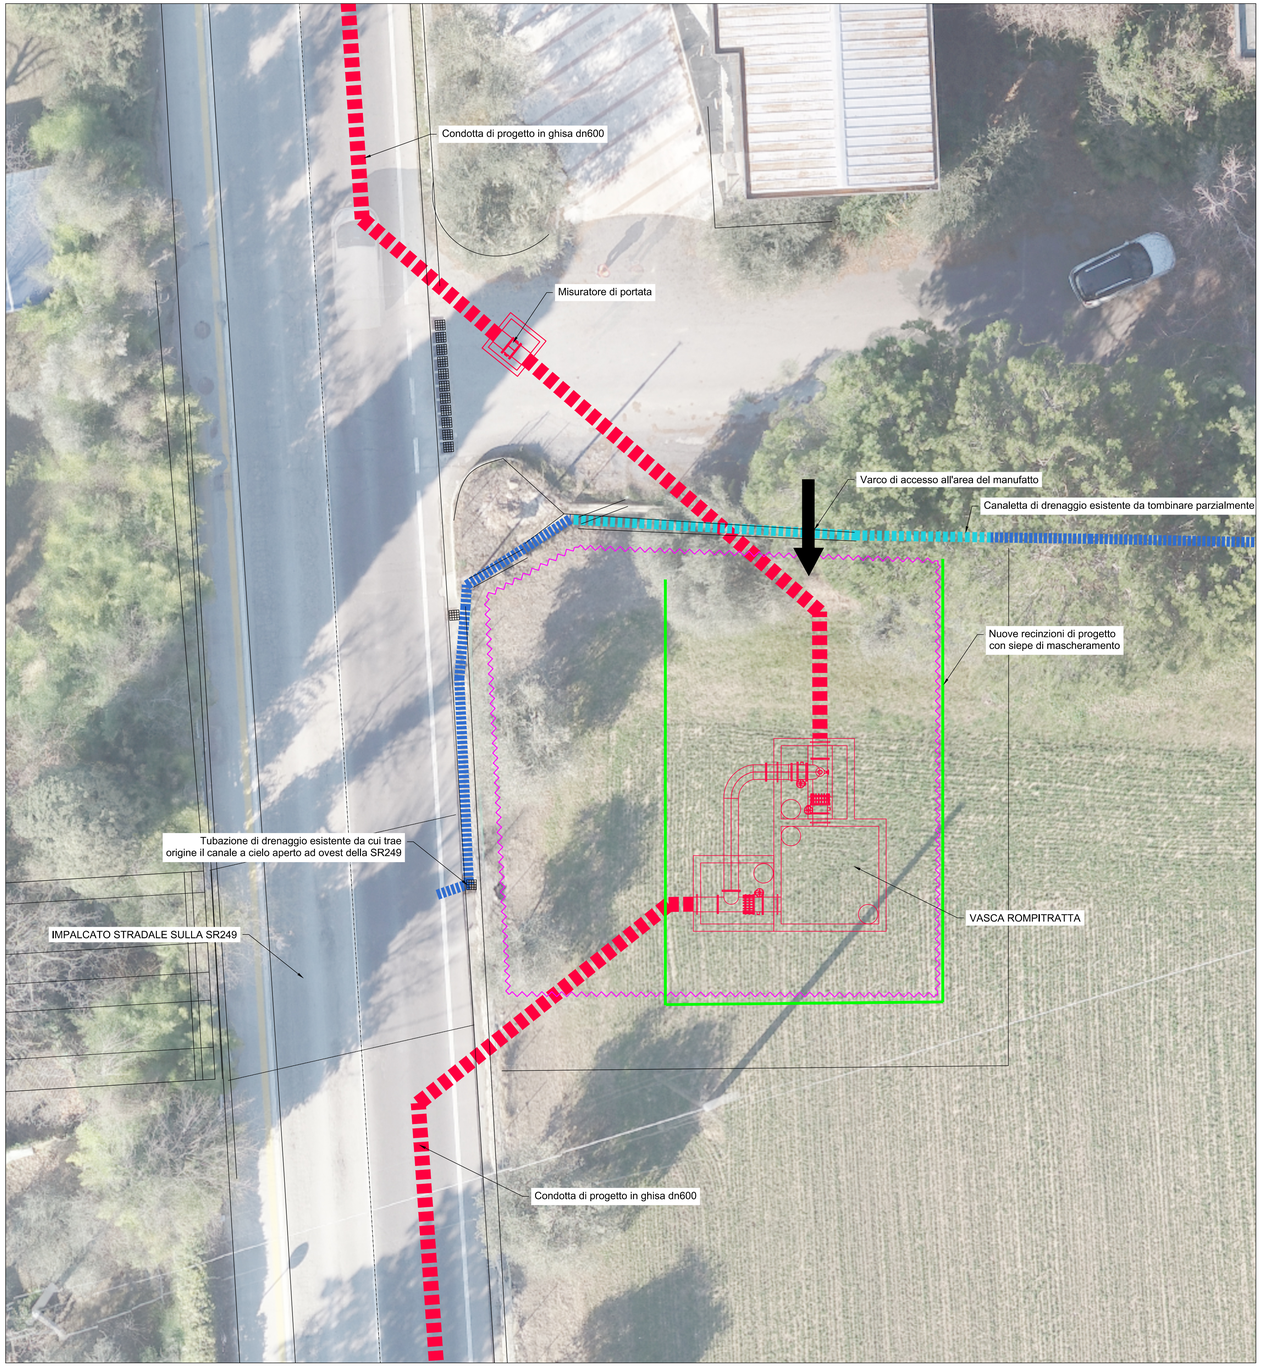


PLANIMETRIA CATASTALE - foglio 15 Bardolino SCALA 1:500

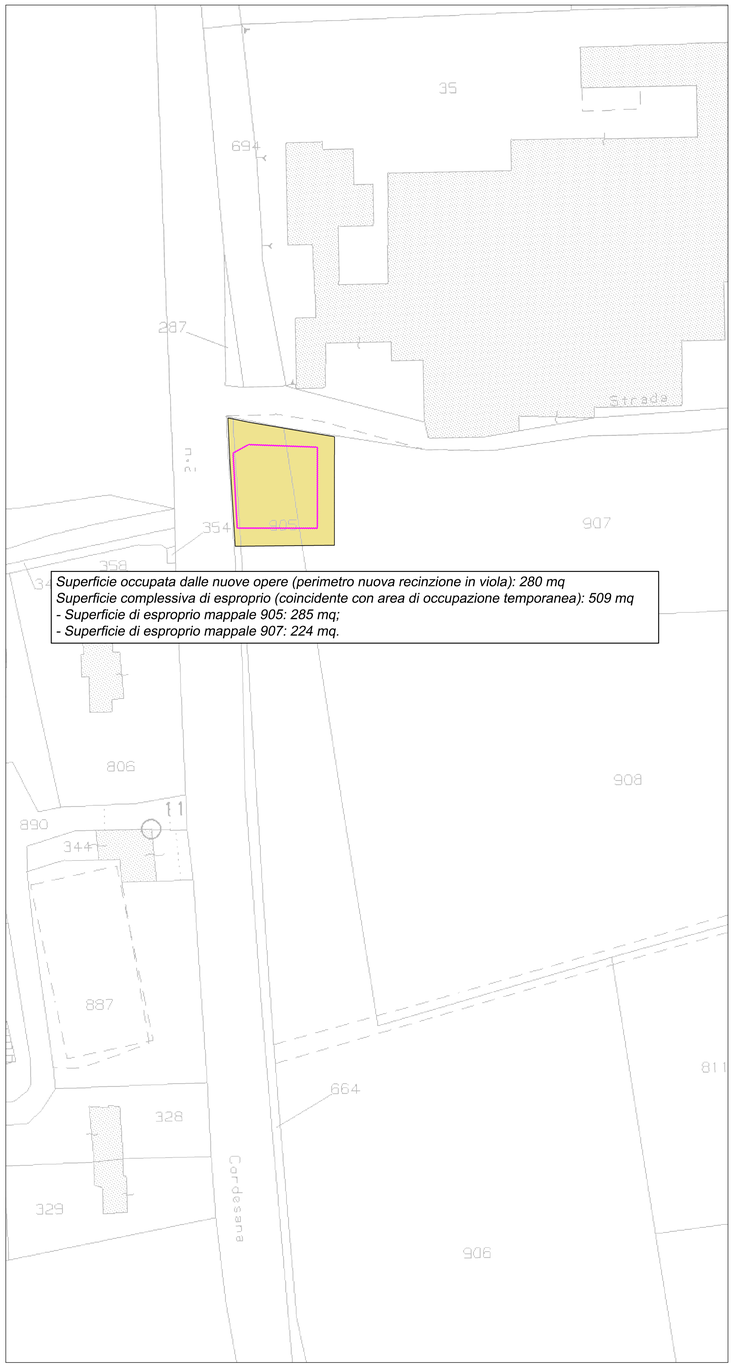

Superficie occupata dalle nuove opere (perimetro nuova recinzione in viola): 280 mq
Superficie complessiva di esproprio (coincidente con area di occupazione temporanea): 509 mq
- Superficie di esproprio mappale 905: 285 mq;
- Superficie di esproprio mappale 907: 224 mq.

INQUADRAMENTO NEL PIANO INTERVENTI COMUNALE (2020)

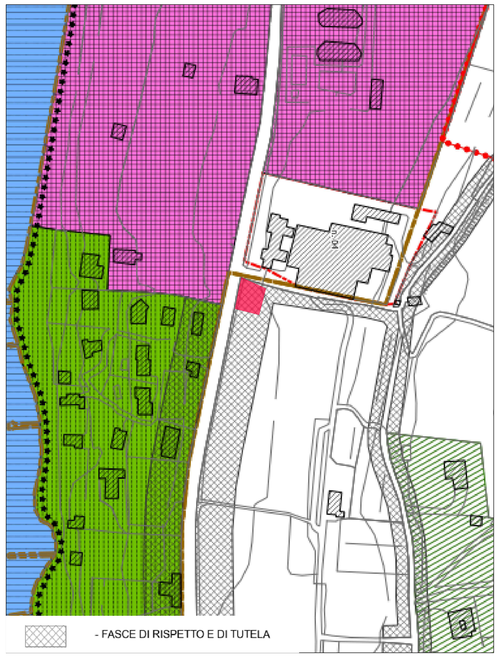

- FASCE DI RISPETTO E DI TUTELA

AZIENDA GARDESANA SERVIZI

"INTERVENTI DI RIQUALIFICAZIONE DEL SISTEMA DI RACCOLTA DEI REFLUI NEL BACINO DEL LAGO DI GARDA - SPONDA VERONESE"
Lotto 1 - Tratto 4 - 2°Stralcio
"OPERE COLLETTORE IN PRESSIONE ED OPERE COMPLEMENTARI TRATTO PERGOLANA - ROCCA VELA - COMUNE BARDOLINO"
Lotto 8 - Tratto 4_OC
CIG: B7E3B750B2 - CUP: J33F17000010002



PROGETTO ESECUTIVO

PROGETTISTA E COORDINATORE SICUREZZA IN FASE DI PROGETTO:
Ing. Giovanni Battista Matteotti

COLLABORAZIONE:
Ing. Luca Petracin
Ing. Andrea Martinello
Ing. Emanuele Anderlini
Ing. Filiberto Boscolo Lisetto
Geom. Elisa Zatti

mass INGEGNERIA E ARCHITETTURA SRL
Via Sorio 33/a, 35141 PADOVA
Tel. 049 723300 - Mail: info@massrl.com

RESPONSABILE UNICO DEL PROGETTO:
Dott. Ing. Carlo Alberto Voi

TITOLO			SCALA	CODICE ELABORATO	
VASCA ROMPITRATTA - PLANIMETRIA GENERALE E INQUADRAMENTO CATASTALE			varie	B-75-000	
N° REV	DATA	DESCRIZIONE	ESEGUITO	VERIFICATO	APPROVATO
00	Marzo 2026	PRIMA EMISSIONE	Ing. L. Petracin	Ing. L. Petracin	Ing. G. B. Matteotti
01					
02					
03					
04					