

PIANTA OPERE INTERRATE

SCALA 1:50

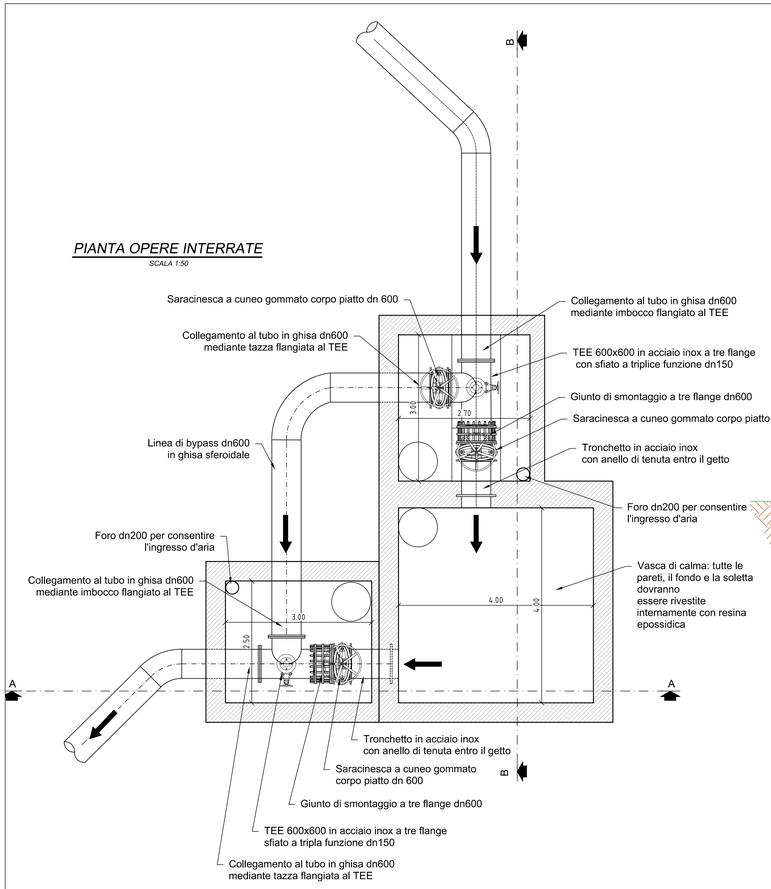


SEZIONE TRASVERSALE B-B

SCALA 1:50

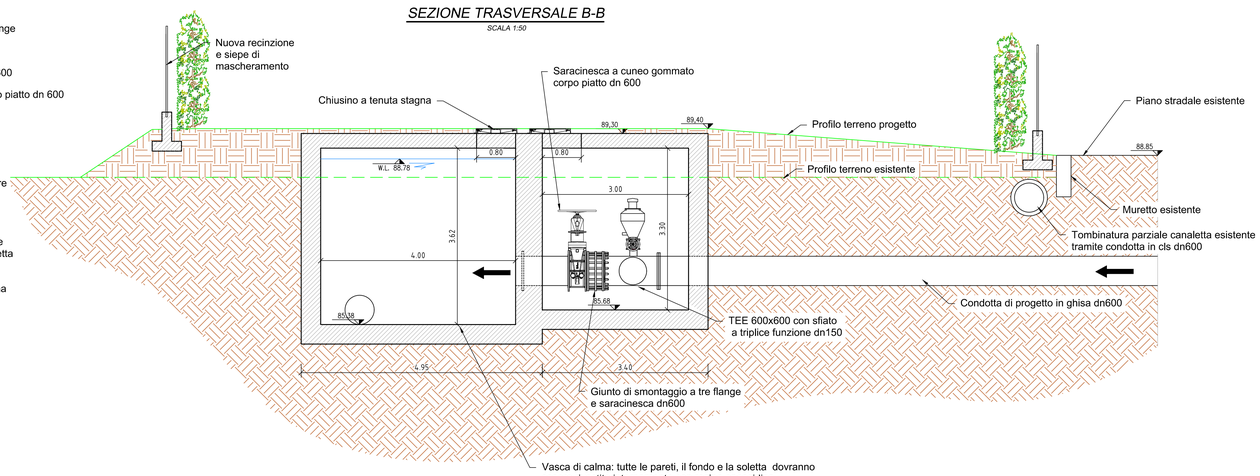

SEZIONE TRASVERSALE A-A

SCALA 1:50

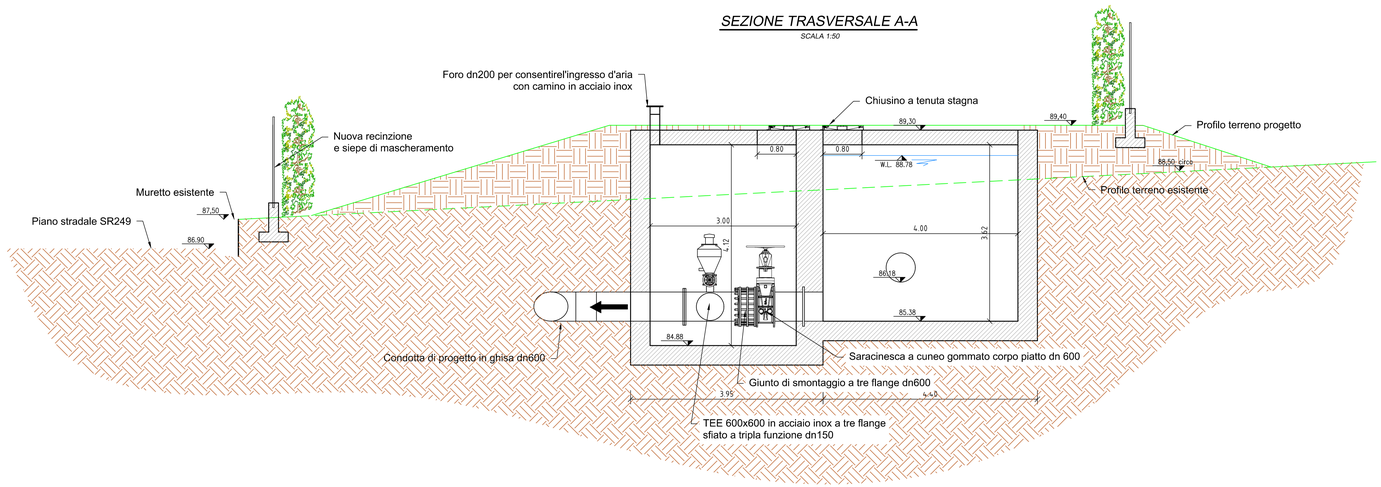

SCALA GRAFICA 1:50

0m 0.50 1.00 1.50 2.00 2.50m

AZIENDA GARDESANA SERVIZI

azienda gardesana servizi

"INTERVENTI DI RIQUALIFICAZIONE DEL SISTEMA DI RACCOLTA DEI REFLUI NEL BACINO DEL LAGO DI GARDA - SPONDA VERONESE"
Lotto 1 - Tratto 4 - 2°Stralcio
"OPERE COLLETTORE IN PRESSIONE ED OPERE COMPLEMENTARI TRATTO PERGOLANA - ROCCA VELA - COMUNE BARDOLINO"
Lotto 8 - Tratto 4_OC

CIG: B7E3B750B2 - CUP: J33F17000010002



PROGETTO ESECUTIVO

PROGETTISTA E COORDINATORE SICUREZZA IN FASE DI PROGETTO:
Ing. Giovanni Battista Matteotti

COLLABORAZIONE:
Ing. Luca Petracin
Ing. Andrea Martinello
Ing. Emanuele Anderlini
Ing. Filiberto Boscolo Lisetto
Geom. Elisa Zatti

mass
INGEGNERIA E ARCHITETTURA SRL
Via Sorio 35/a, 35141 PADOVA
Tel. 049 723320 - Mail: info@matteotti.com

RESPONSABILE UNICO DEL PROGETTO:
Dott. Ing. Carlo Alberto Voi

TITOLO			*SCALA*	*CODICE ELABORATO*	
VASCA ROMPITRATTA - PIANTA E SEZIONI			varie	B-76-001	
N° REV	*DATA*	*DESCRIZIONE*	*ESEGUITO*	*VERIFICATO*	*APPROVATO*
00	Marzo 2026	PRIMA EMISSIONE	Ing. L. Petracin	Ing. L. Petracin	Ing. G. B. Matteotti
01	Luglio 2026	AGGIORNAMENTO POST VERIFICA AGS	Ing. L. Petracin	Ing. L. Petracin	Ing. G. B. Matteotti
02					
03					
04					