PIANTA OPERE INTERRATE
SCALA 1:50

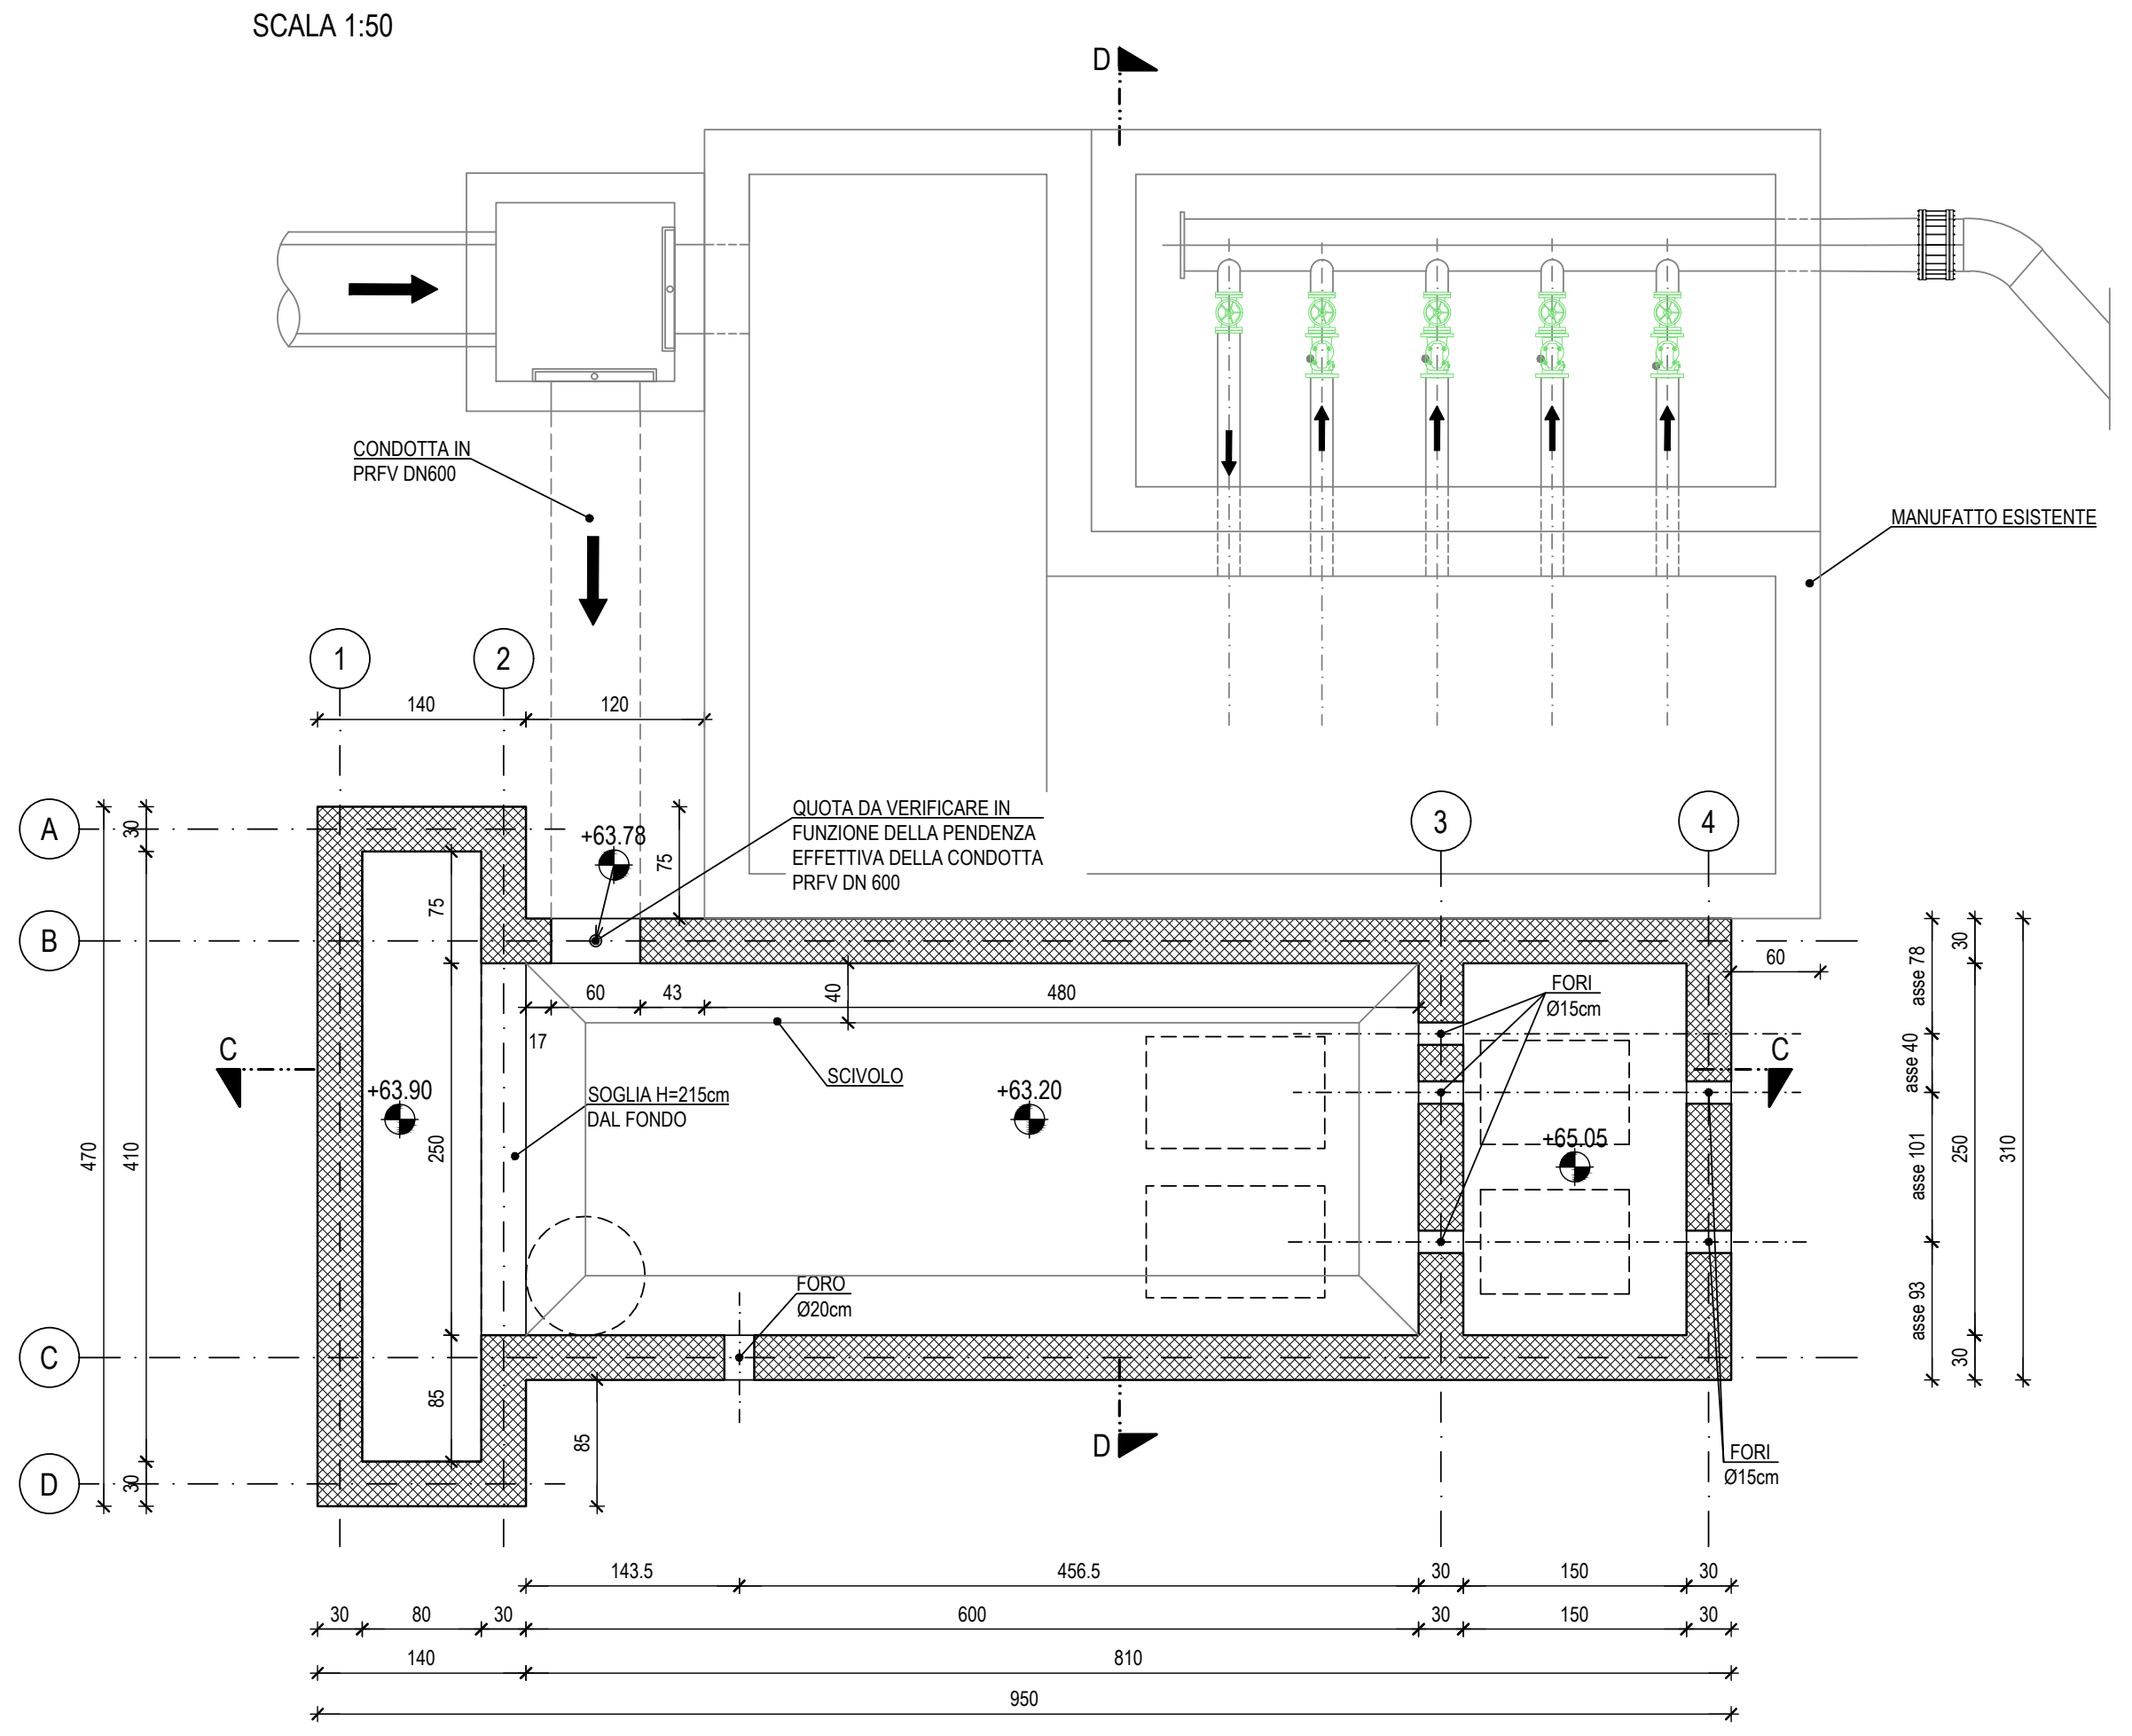

PIANTA COPERTURA
SCALA 1:50

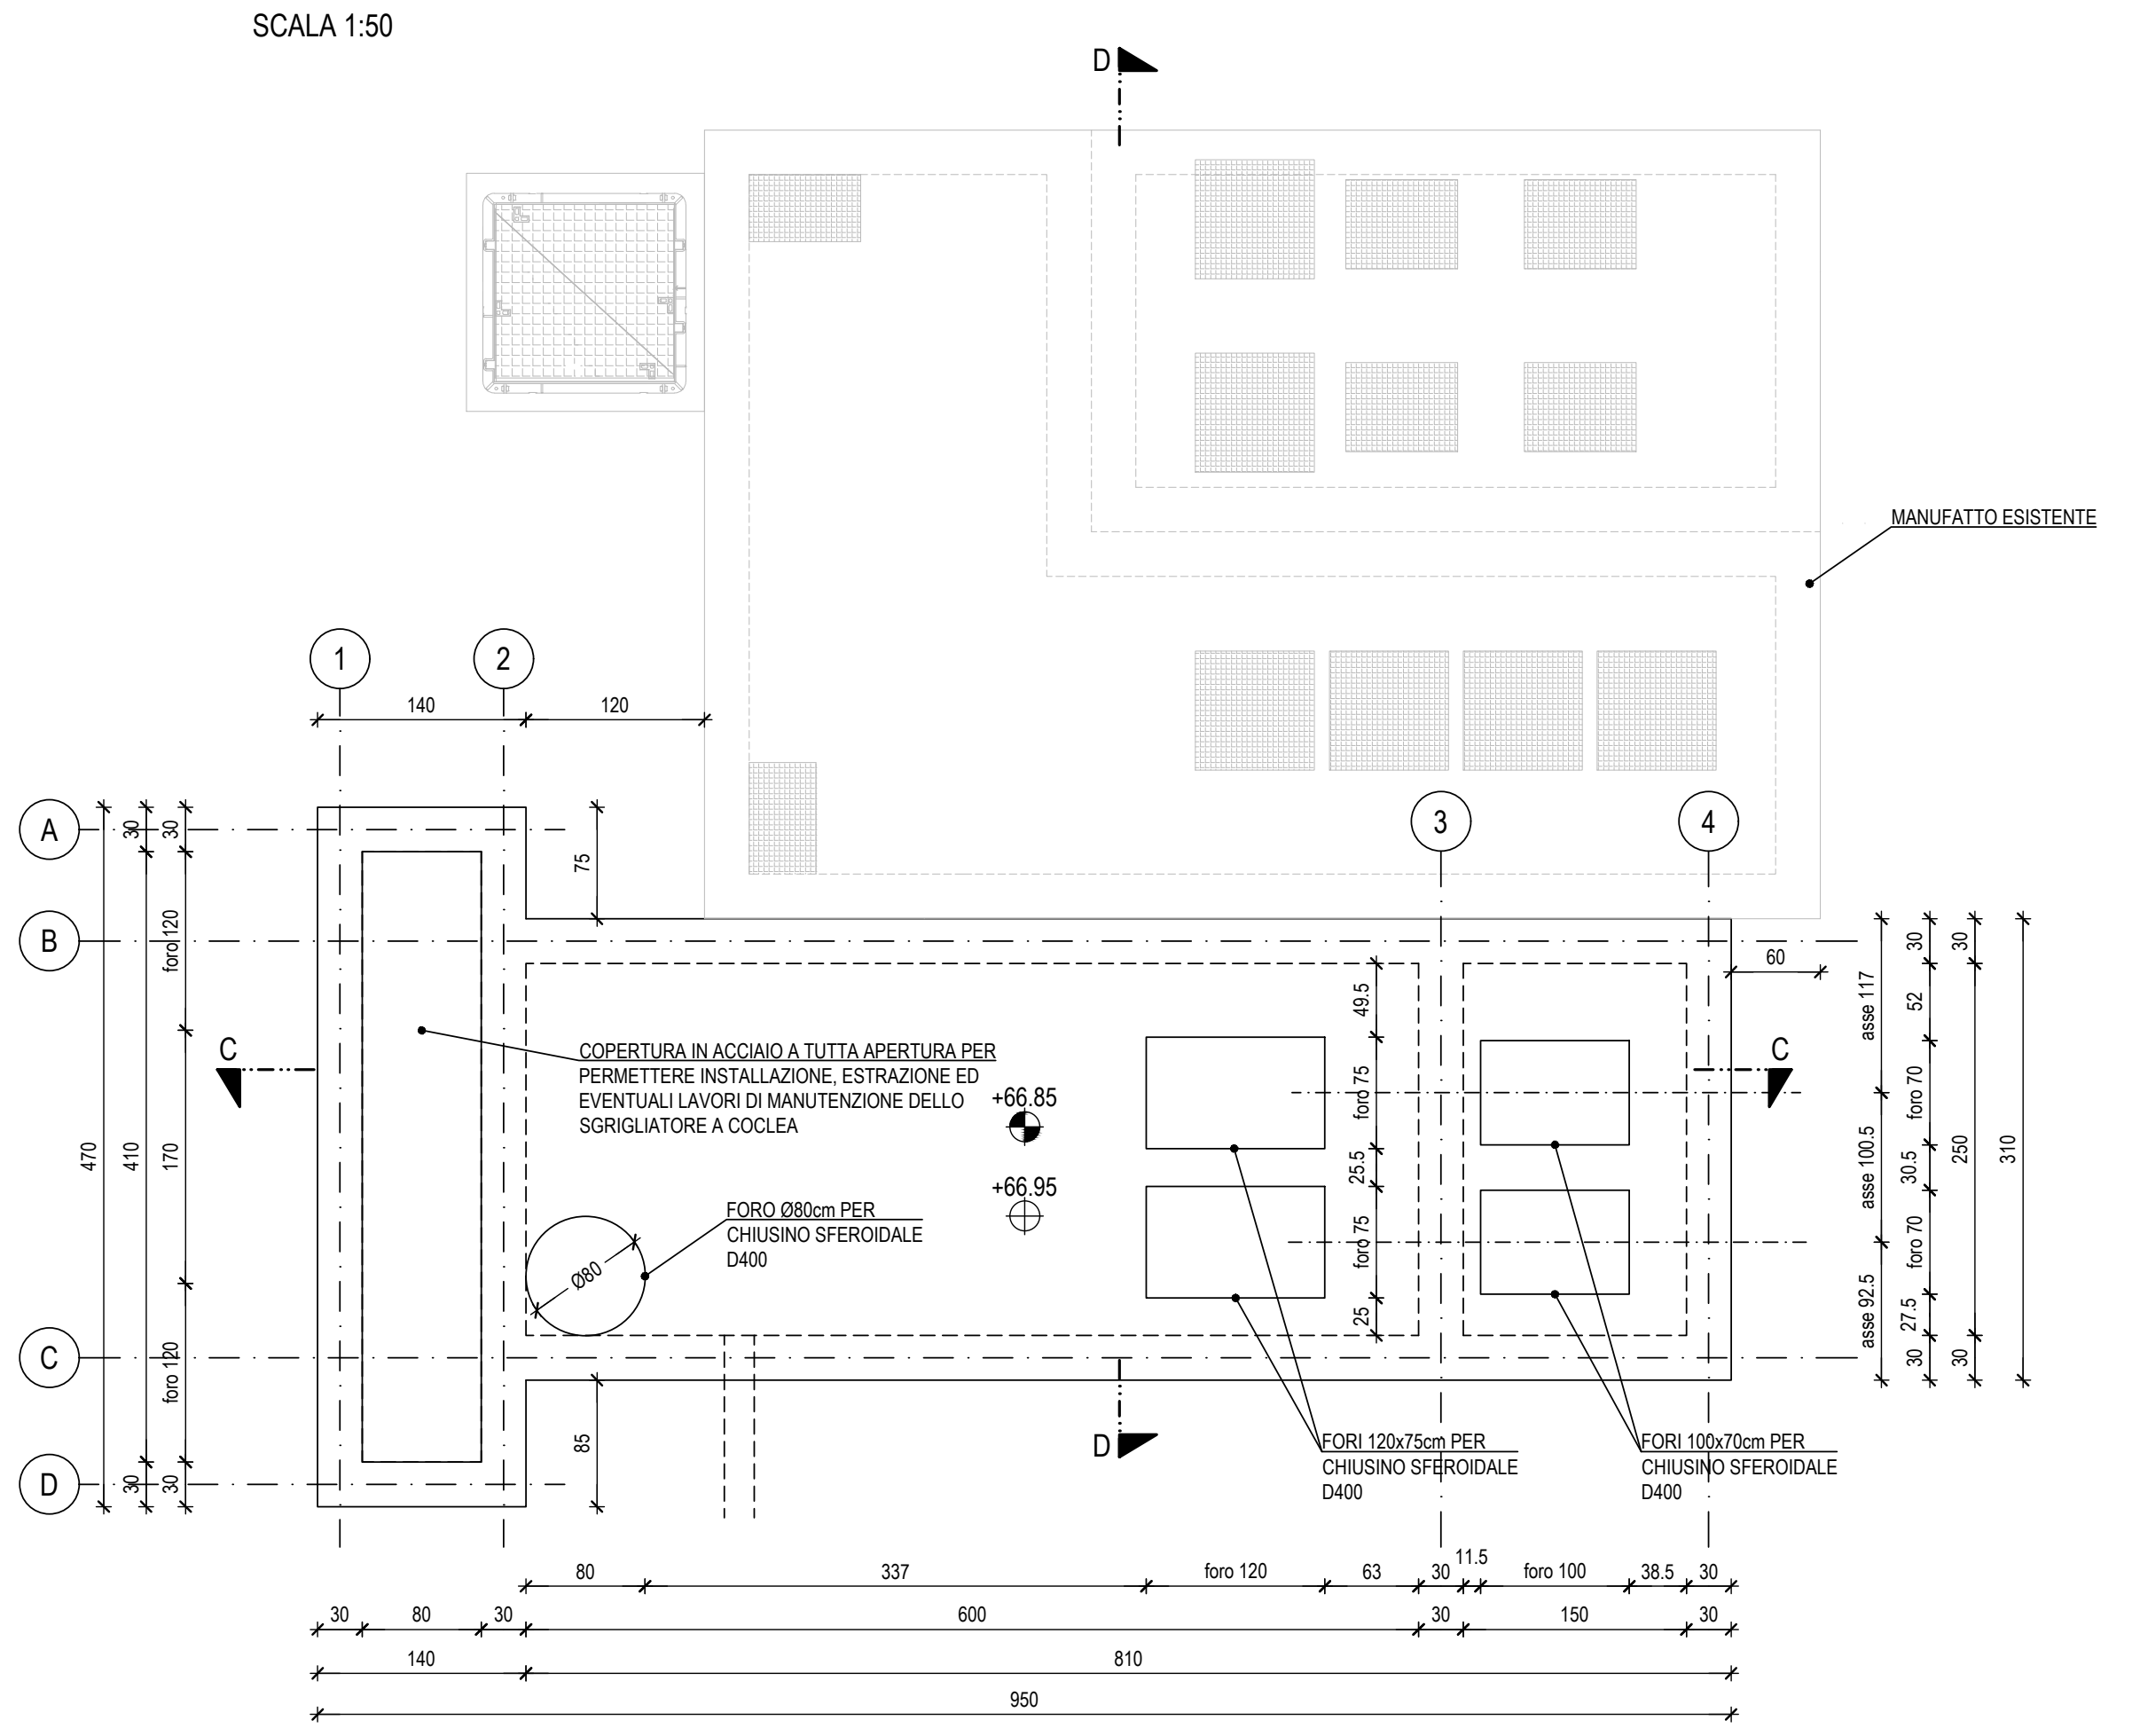
MANUFATTO ESISTENTE
COPERTURA IN ACCIAIO A TUTTA APERTURA PER PERMETTERE INSTALLAZIONE, ESTRAZIONE ED EVENTUALI LAVORI DI MANUTENZIONE DELLO SGRIGLIATORE A COCLEA
FORO Ø80cm PER CHIUSINO SFEROIDALE D400
FORI 120x70cm PER CHIUSINO SFEROIDALE D400
FORI 100x70cm PER CHIUSINO SFEROIDALE D400
+66.85
+66.95
950
810
600

SEZIONE C-C
SCALA 1:50

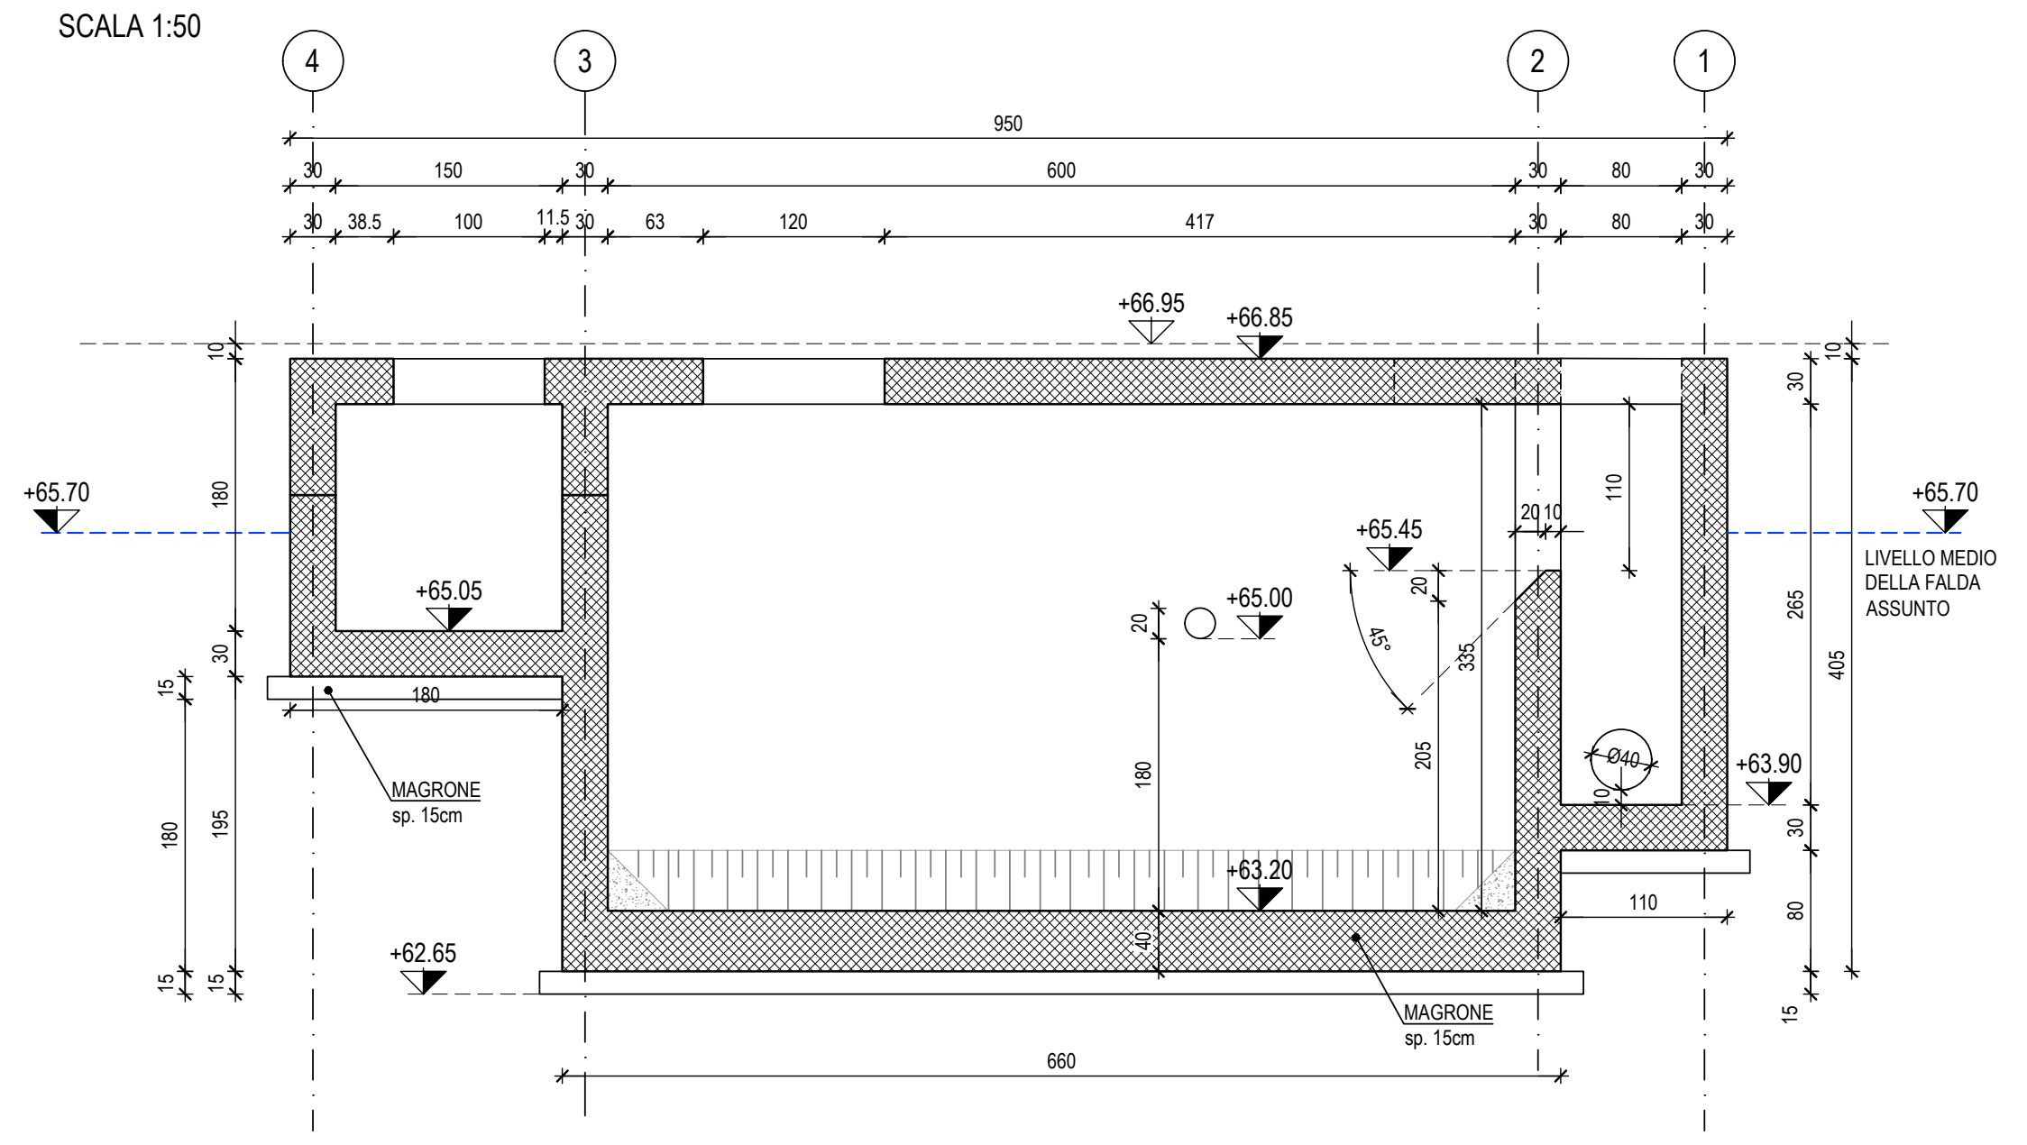

SEZIONE D-D
SCALA 1:50

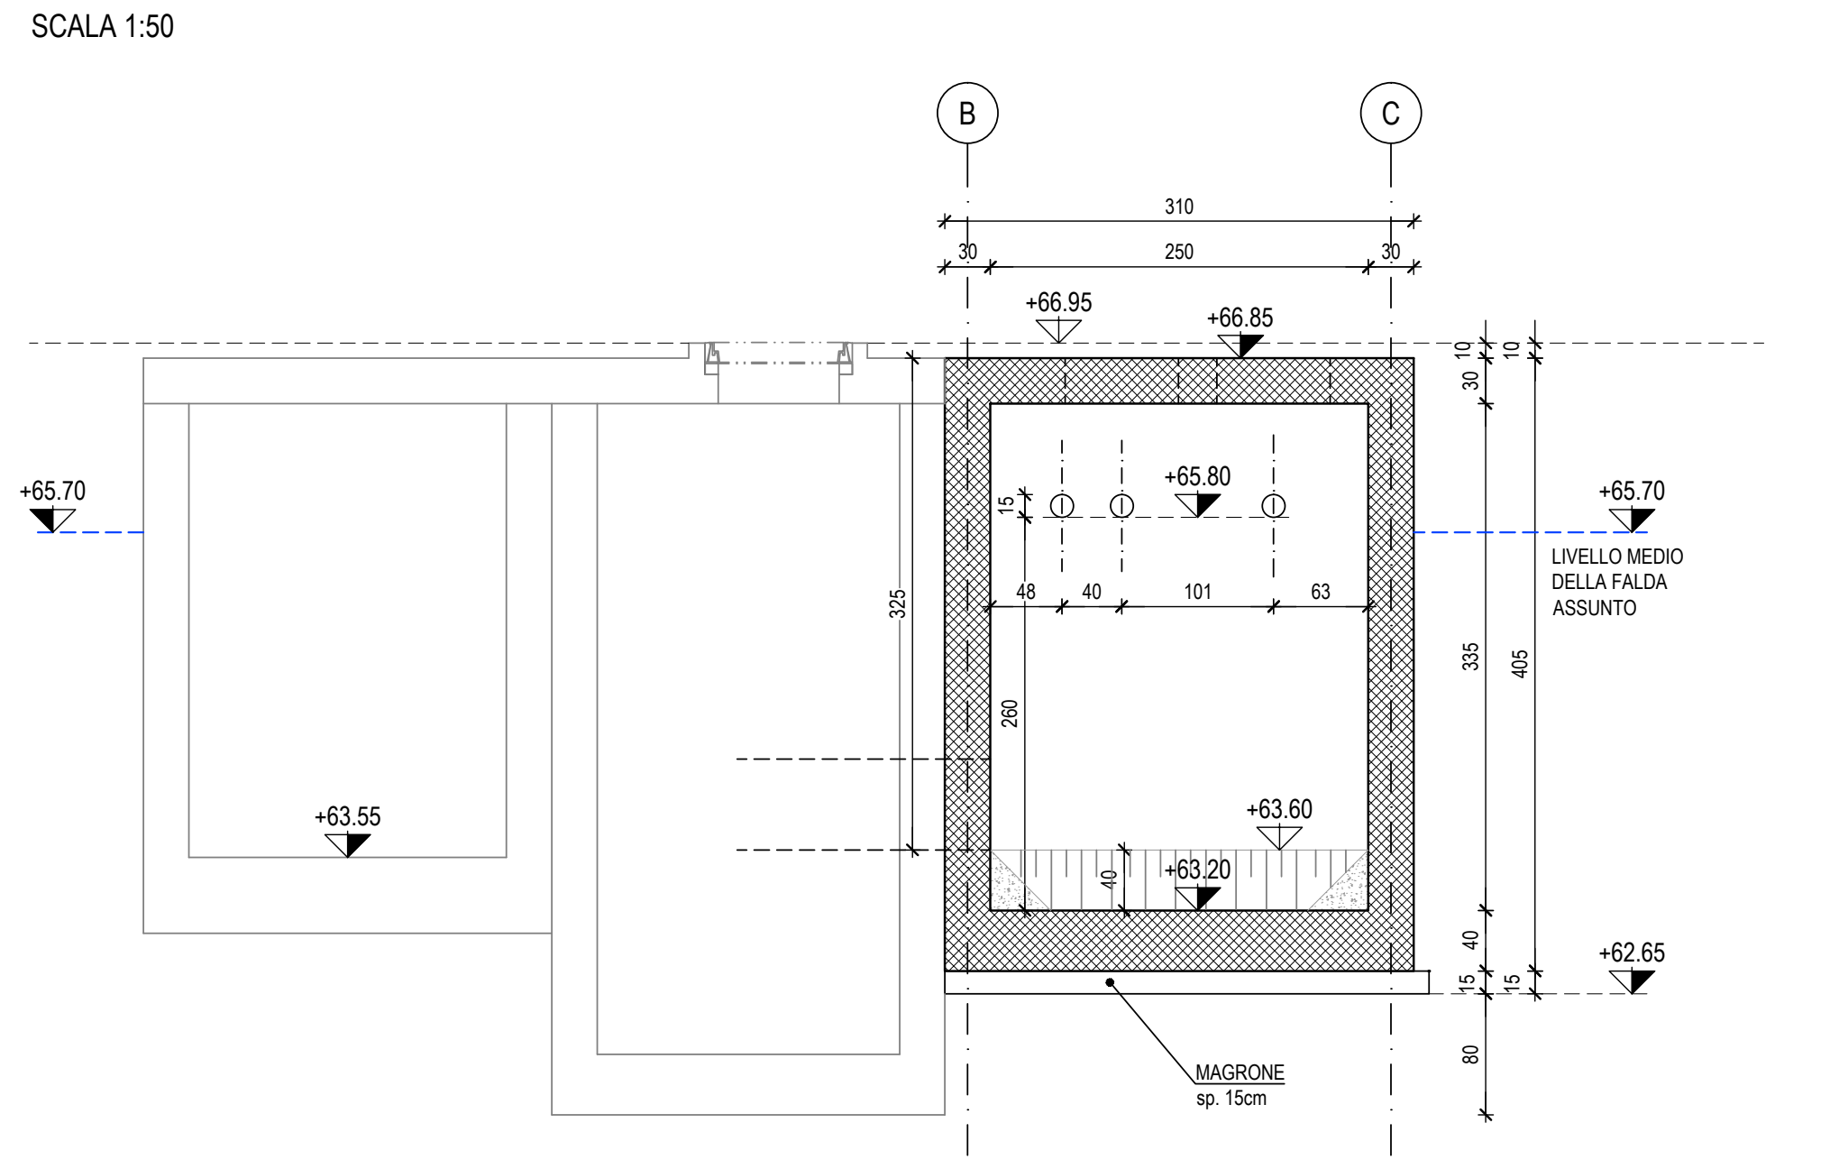

PARTICOLARE - CAVALLOTTI PLATEA/SOLETTE sp.30cm
SCALA 1:10

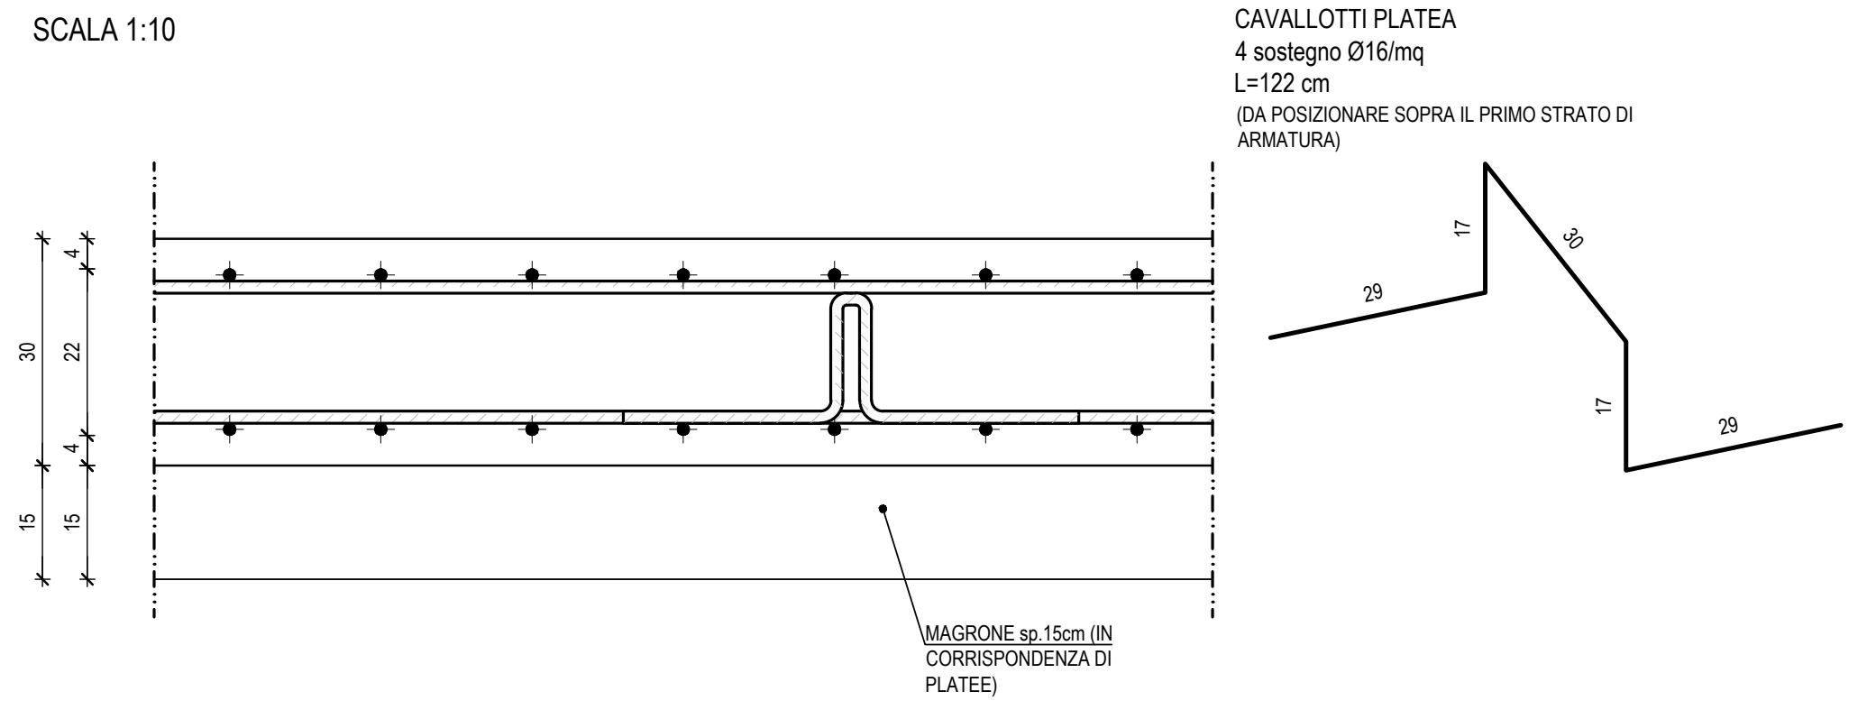
CAVALLOTTI PLATEA
4 sostegno Ø16/mq
L=122 cm
(DA POSIZIONARE SOPRA IL PRIMO STRATO DI ARMATURA)
MAGRONE sp.15cm (IN CORRISPONDENZA DI PLATEE)
30
22
15
4
29
17
30
17
29

ARMATURA
4° strato (sup.) direzione Y Ø16/20;
3° strato (sup.) direzione X Ø16/20;
2° strato (inf.) direzione X Ø16/20;
1° strato (inf.) direzione Y Ø16/20;

PARTICOLARE - CAVALLOTTI PLATEA sp.40cm
SCALA 1:10

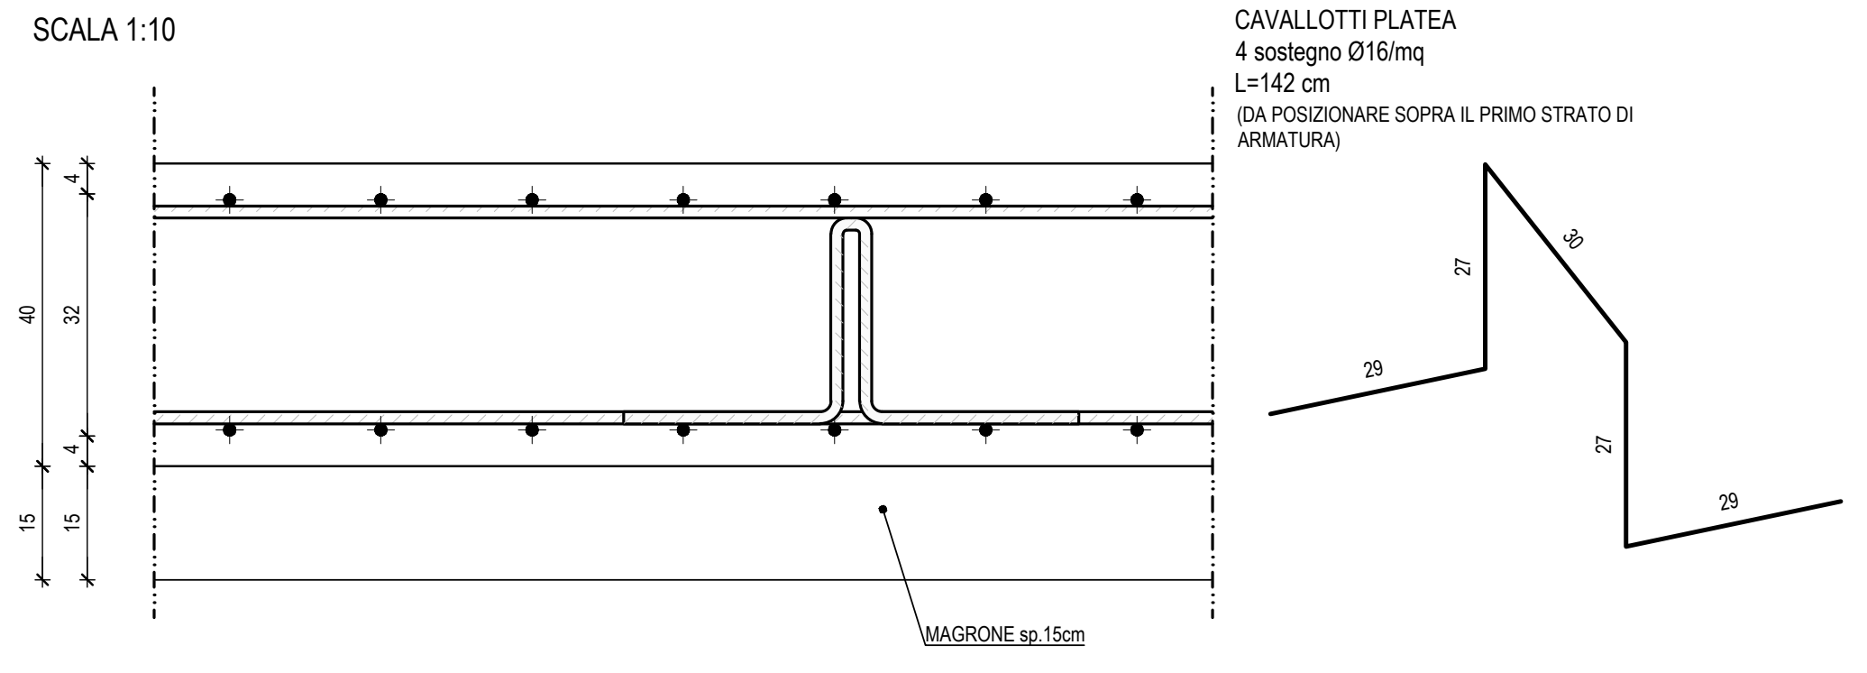

ARMATURA
4° strato (sup.) direzione Y Ø16/20;
3° strato (sup.) direzione X Ø16/20;
2° strato (inf.) direzione X Ø16/20;
1° strato (inf.) direzione Y Ø16/20;

PIANTA ARMATURA PLATEA sp. 40cm QUOTA +63.20m
SCALA 1:50

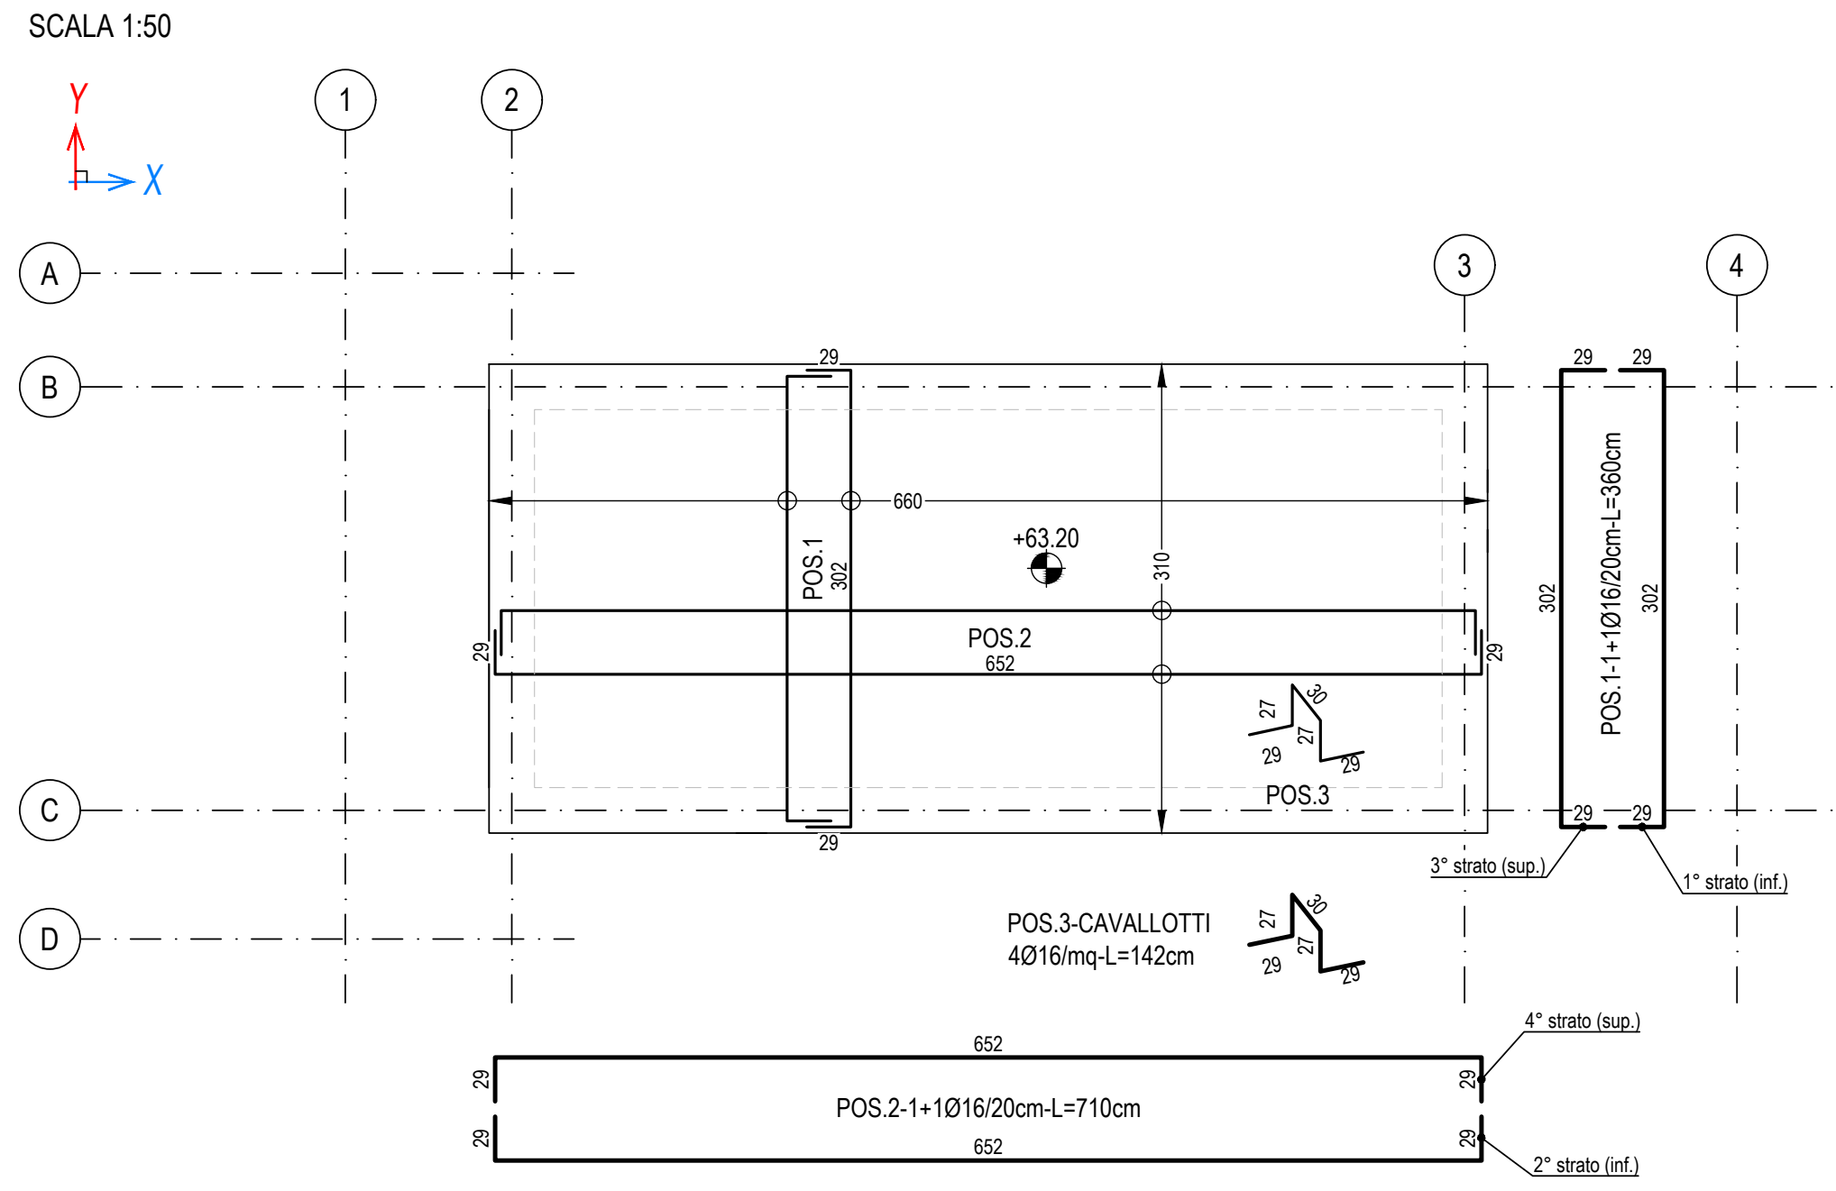
+63.20
POS.1
POS.2
POS.3
POS.1-1+1Ø16/20cm-L=360cm
POS.2-1+1Ø16/20cm-L=710cm
POS.3-CAVALLOTTI 4Ø16/mq-L=142cm

PIANTA ARMATURA PLATEA sp. 30cm QUOTA +63.90m
SCALA 1:50

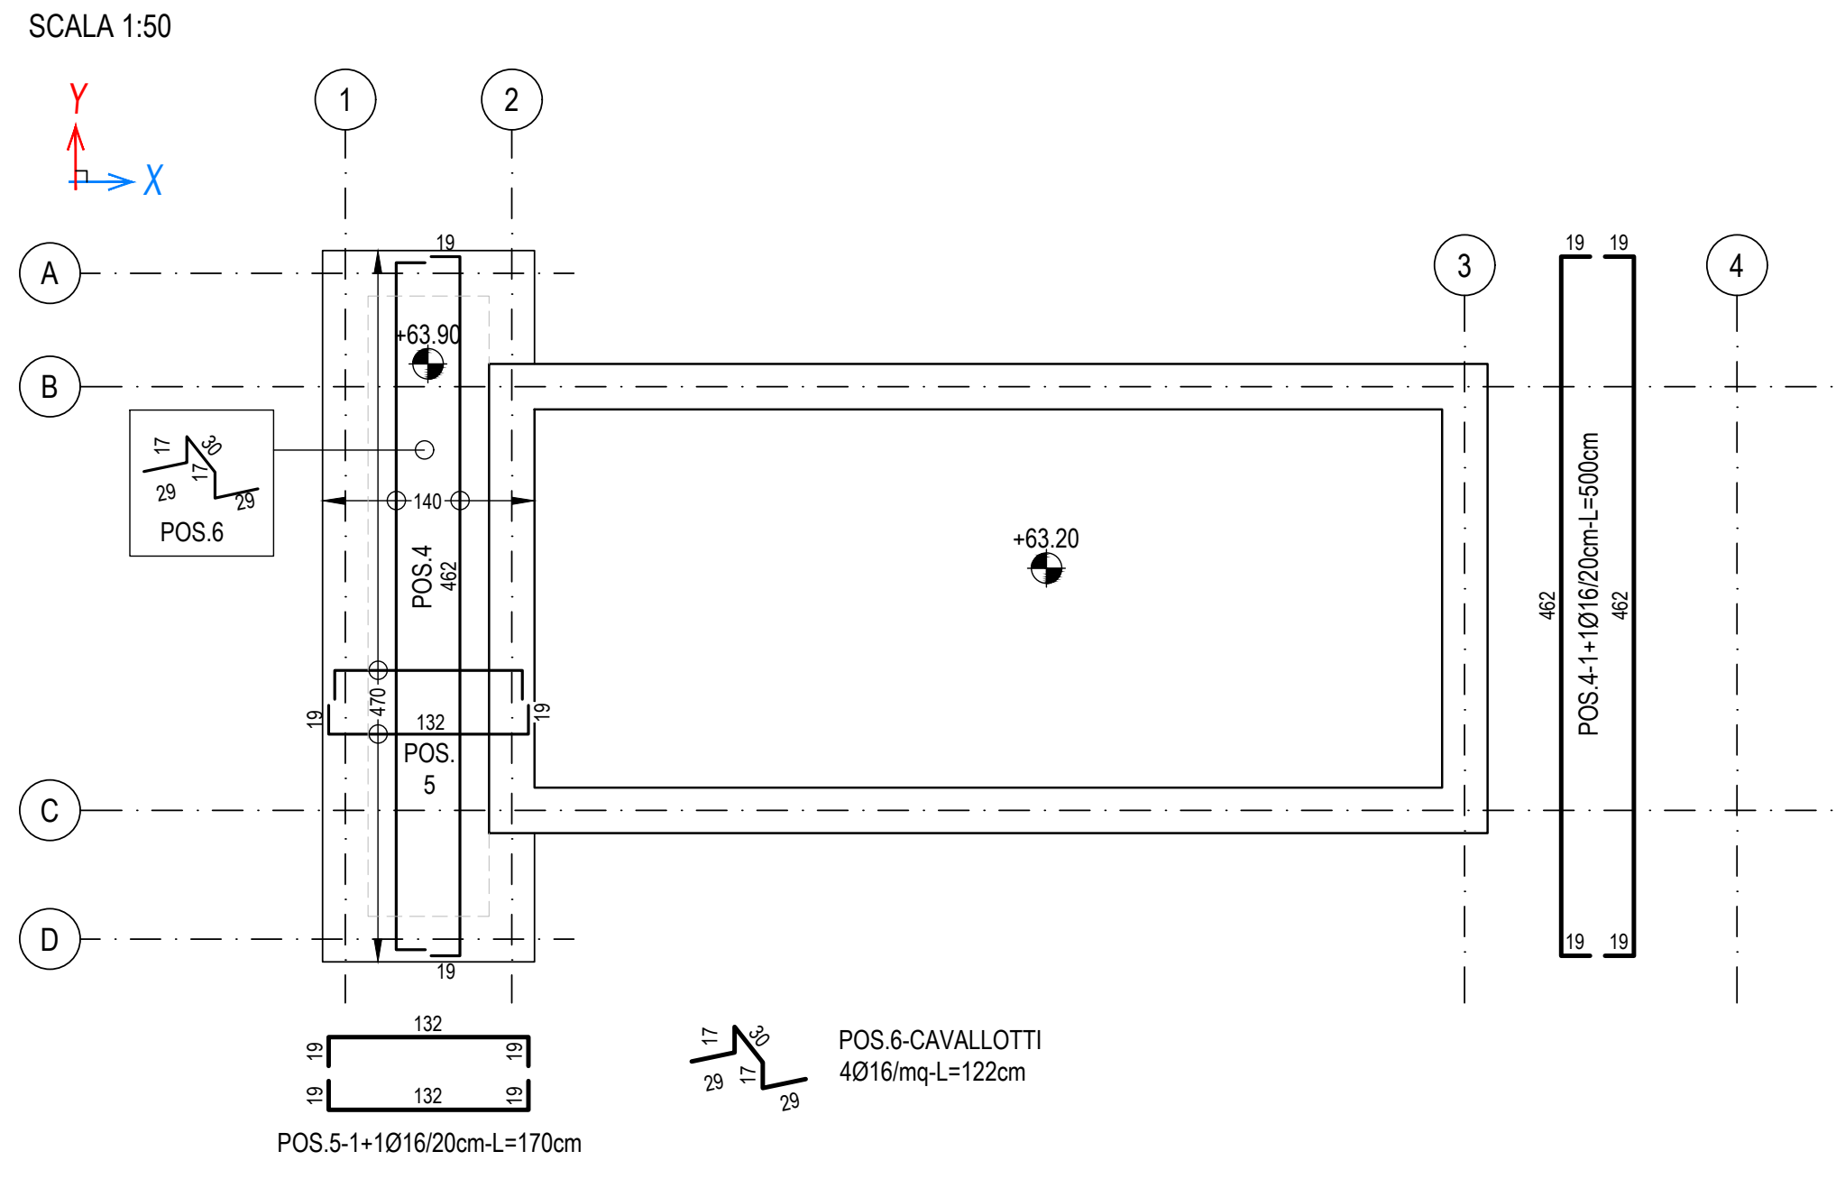
+63.90
+63.20
POS.4
POS.5
POS.6
POS.4-1+1Ø16/20cm-L=500cm
POS.5-1+1Ø16/20cm-L=170cm
POS.6-CAVALLOTTI 4Ø16/mq-L=122cm

PIANTA ARMATURA PLATEA sp. 30cm QUOTA +65.35m
SCALA 1:50

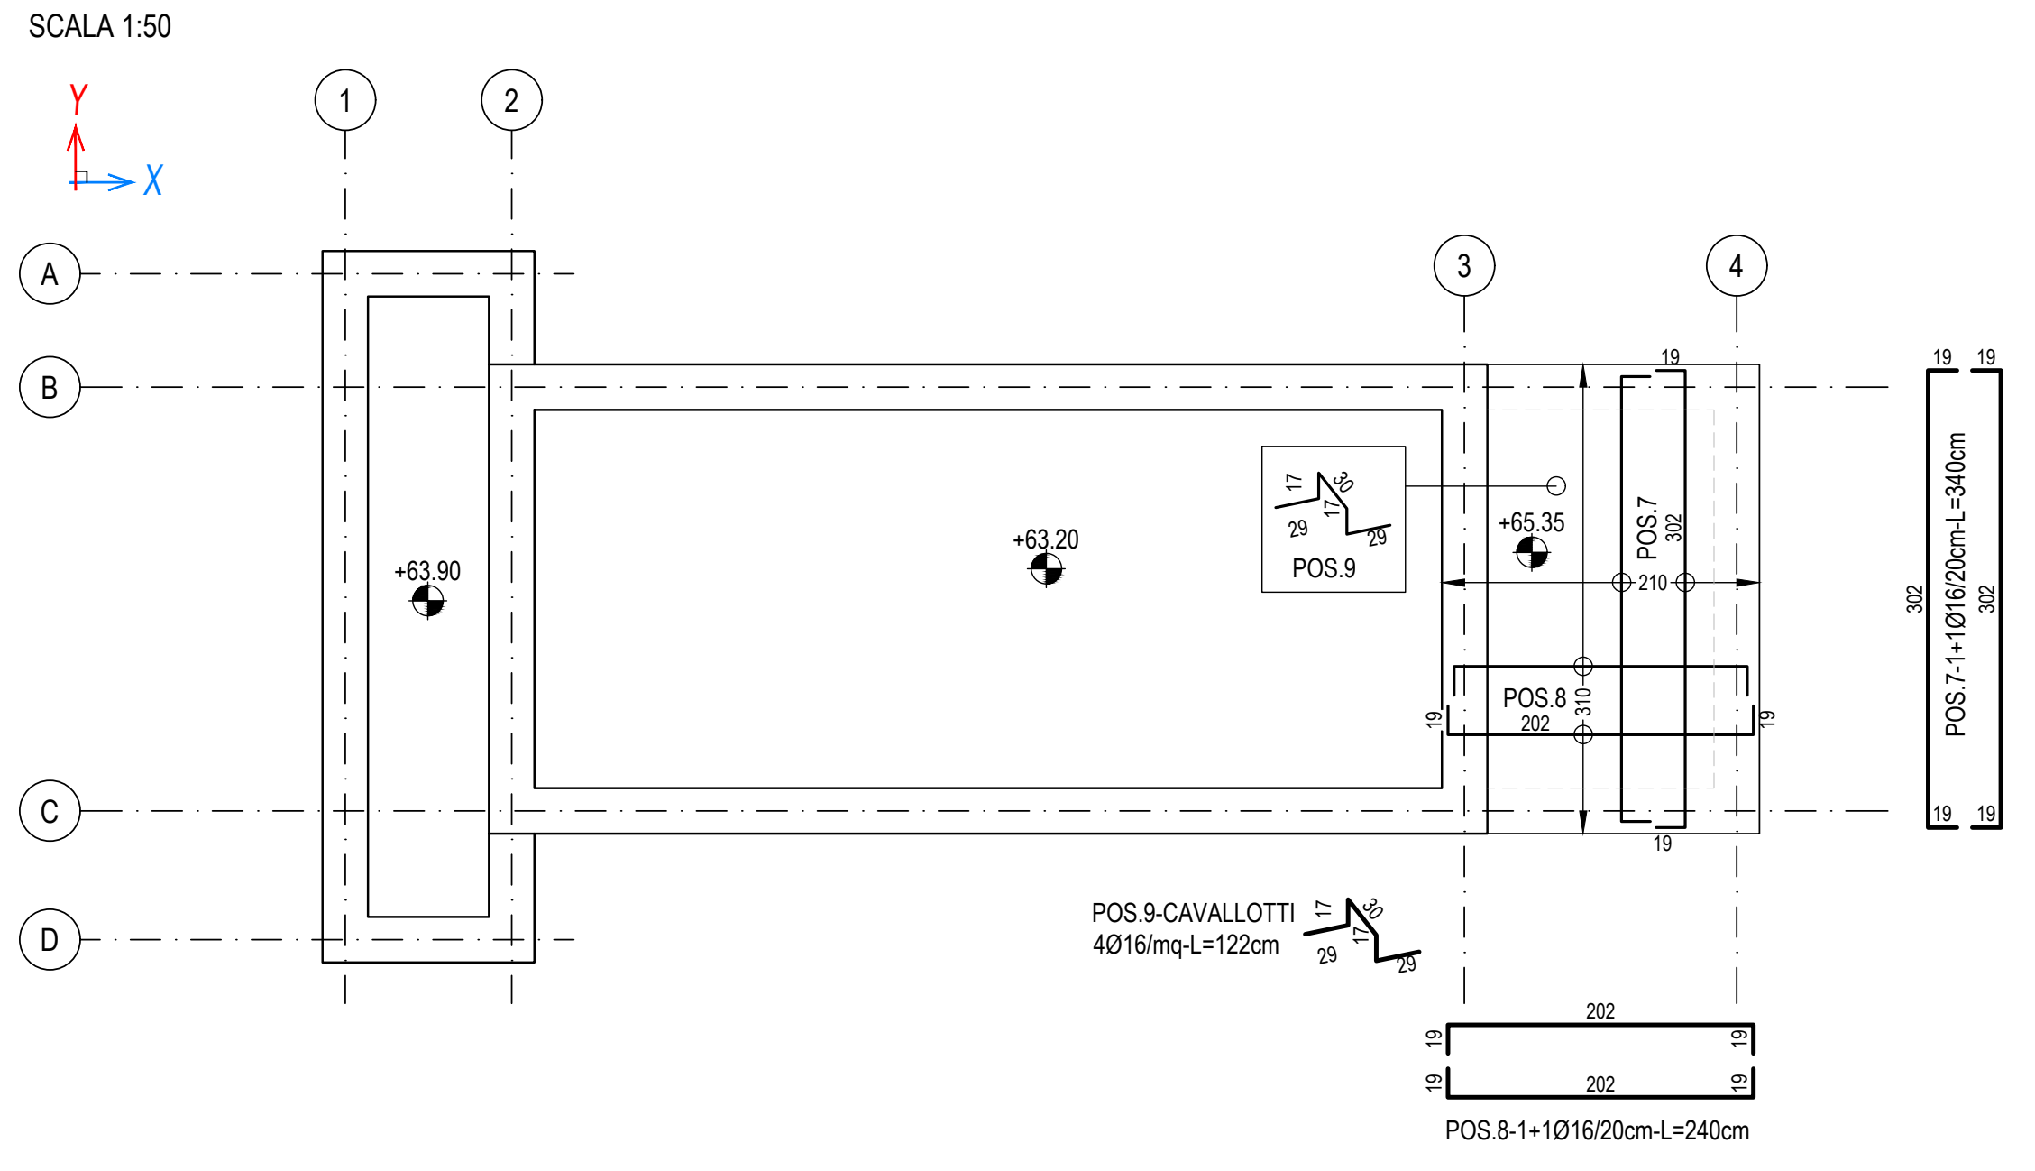
+63.90
+63.20
+65.35
POS.7
POS.8
POS.9
POS.7-1+1Ø16/20cm-L=340cm
POS.8-1+1Ø16/20cm-L=240cm
POS.9-CAVALLOTTI 4Ø16/mq-L=122cm

PIANTA ARMATURA DI BASE SOLETTA DI CHIUSURA SUPERIORE sp. 30cm QUOTA +66.85m (DIREZIONE Y)
SCALA 1:50

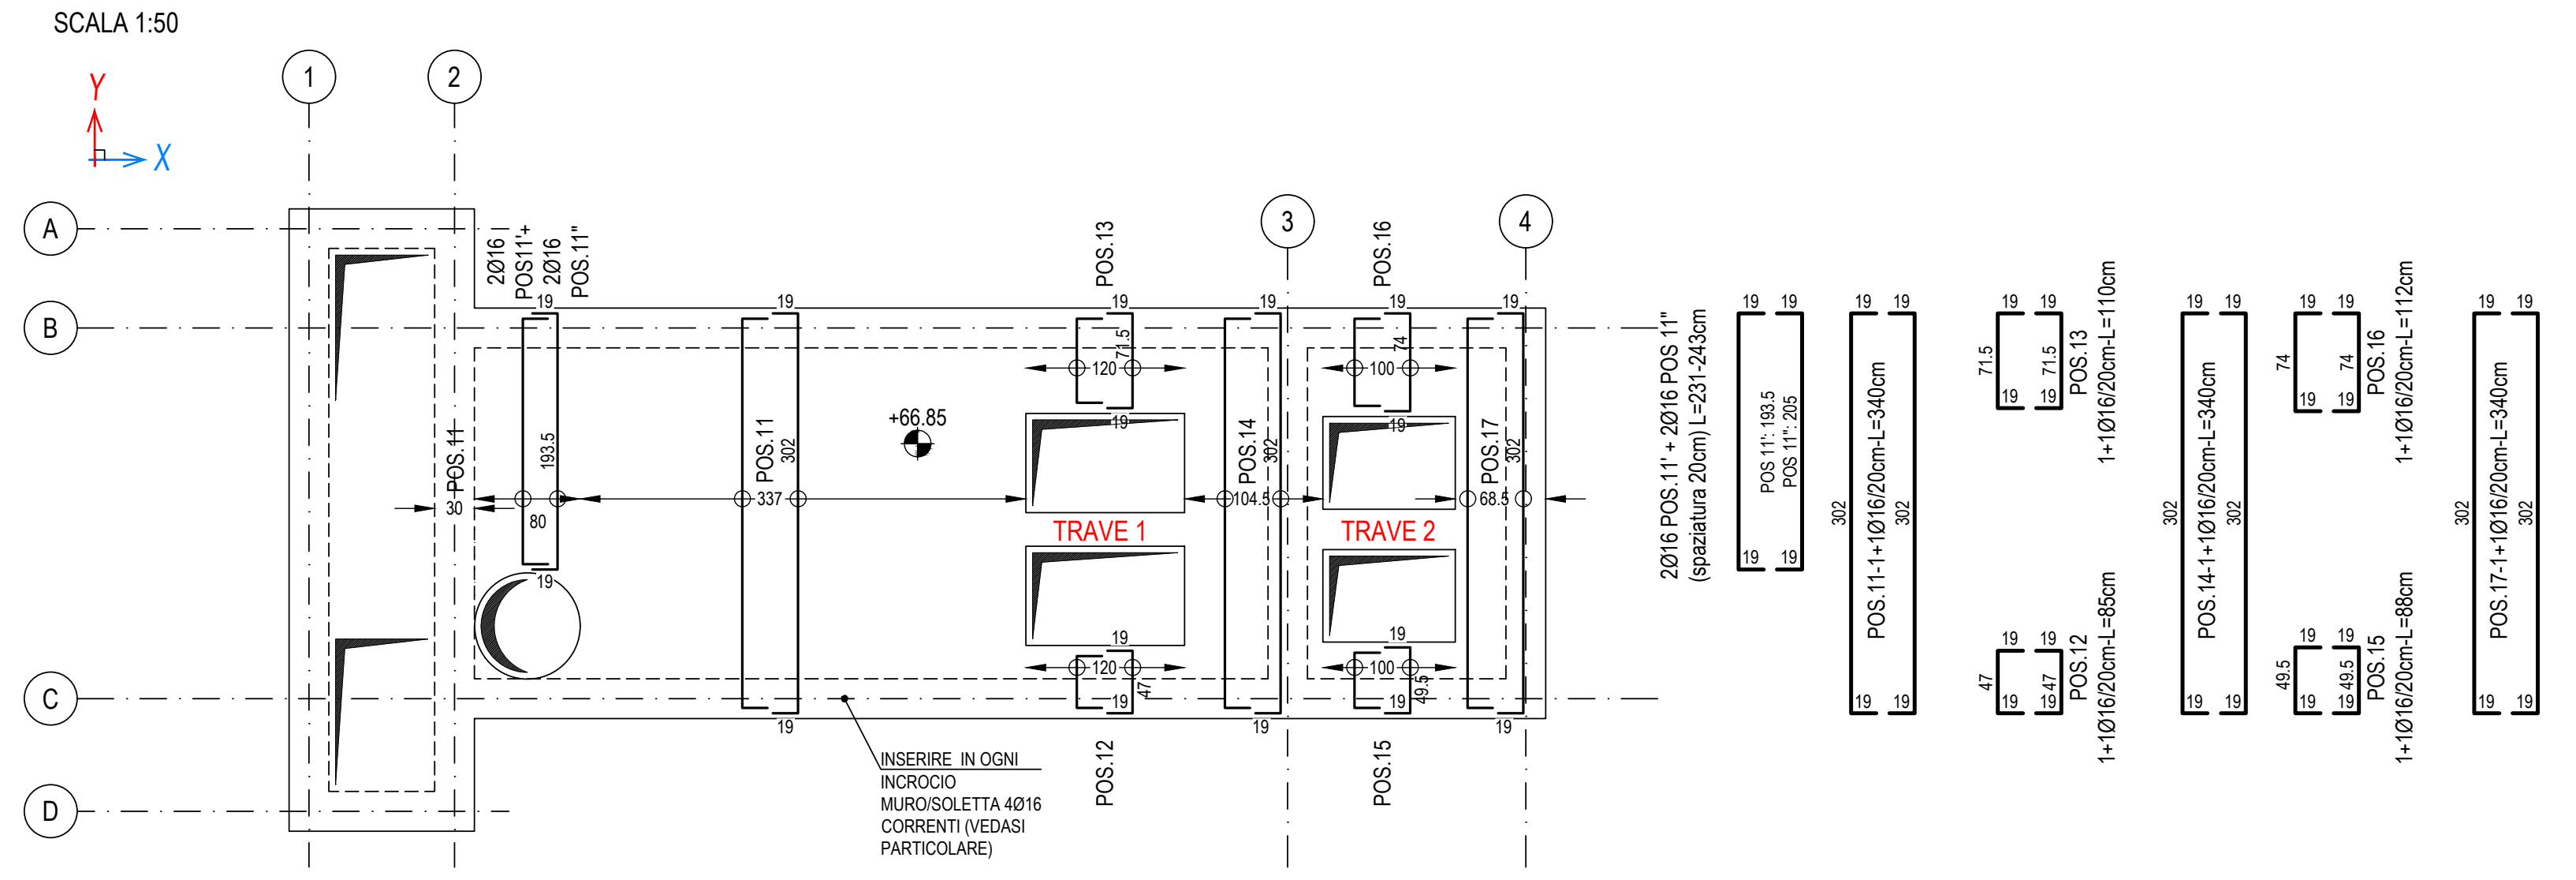
+66.85
TRAVE 1
TRAVE 2
INSERIRE IN OGNI INCROCIO MURO/SOLETTA 4Ø16 CORRENTI (VEDASI PARTICOLARE)
POS.11-1+1Ø16/20cm-L=340cm
POS.14-1+1Ø16/20cm-L=340cm
POS.17-1+1Ø16/20cm-L=340cm

PIANTA ARMATURA DI BASE SOLETTA DI CHIUSURA SUPERIORE sp. 30cm QUOTA +66.85m (DIREZIONE X)
SCALA 1:50

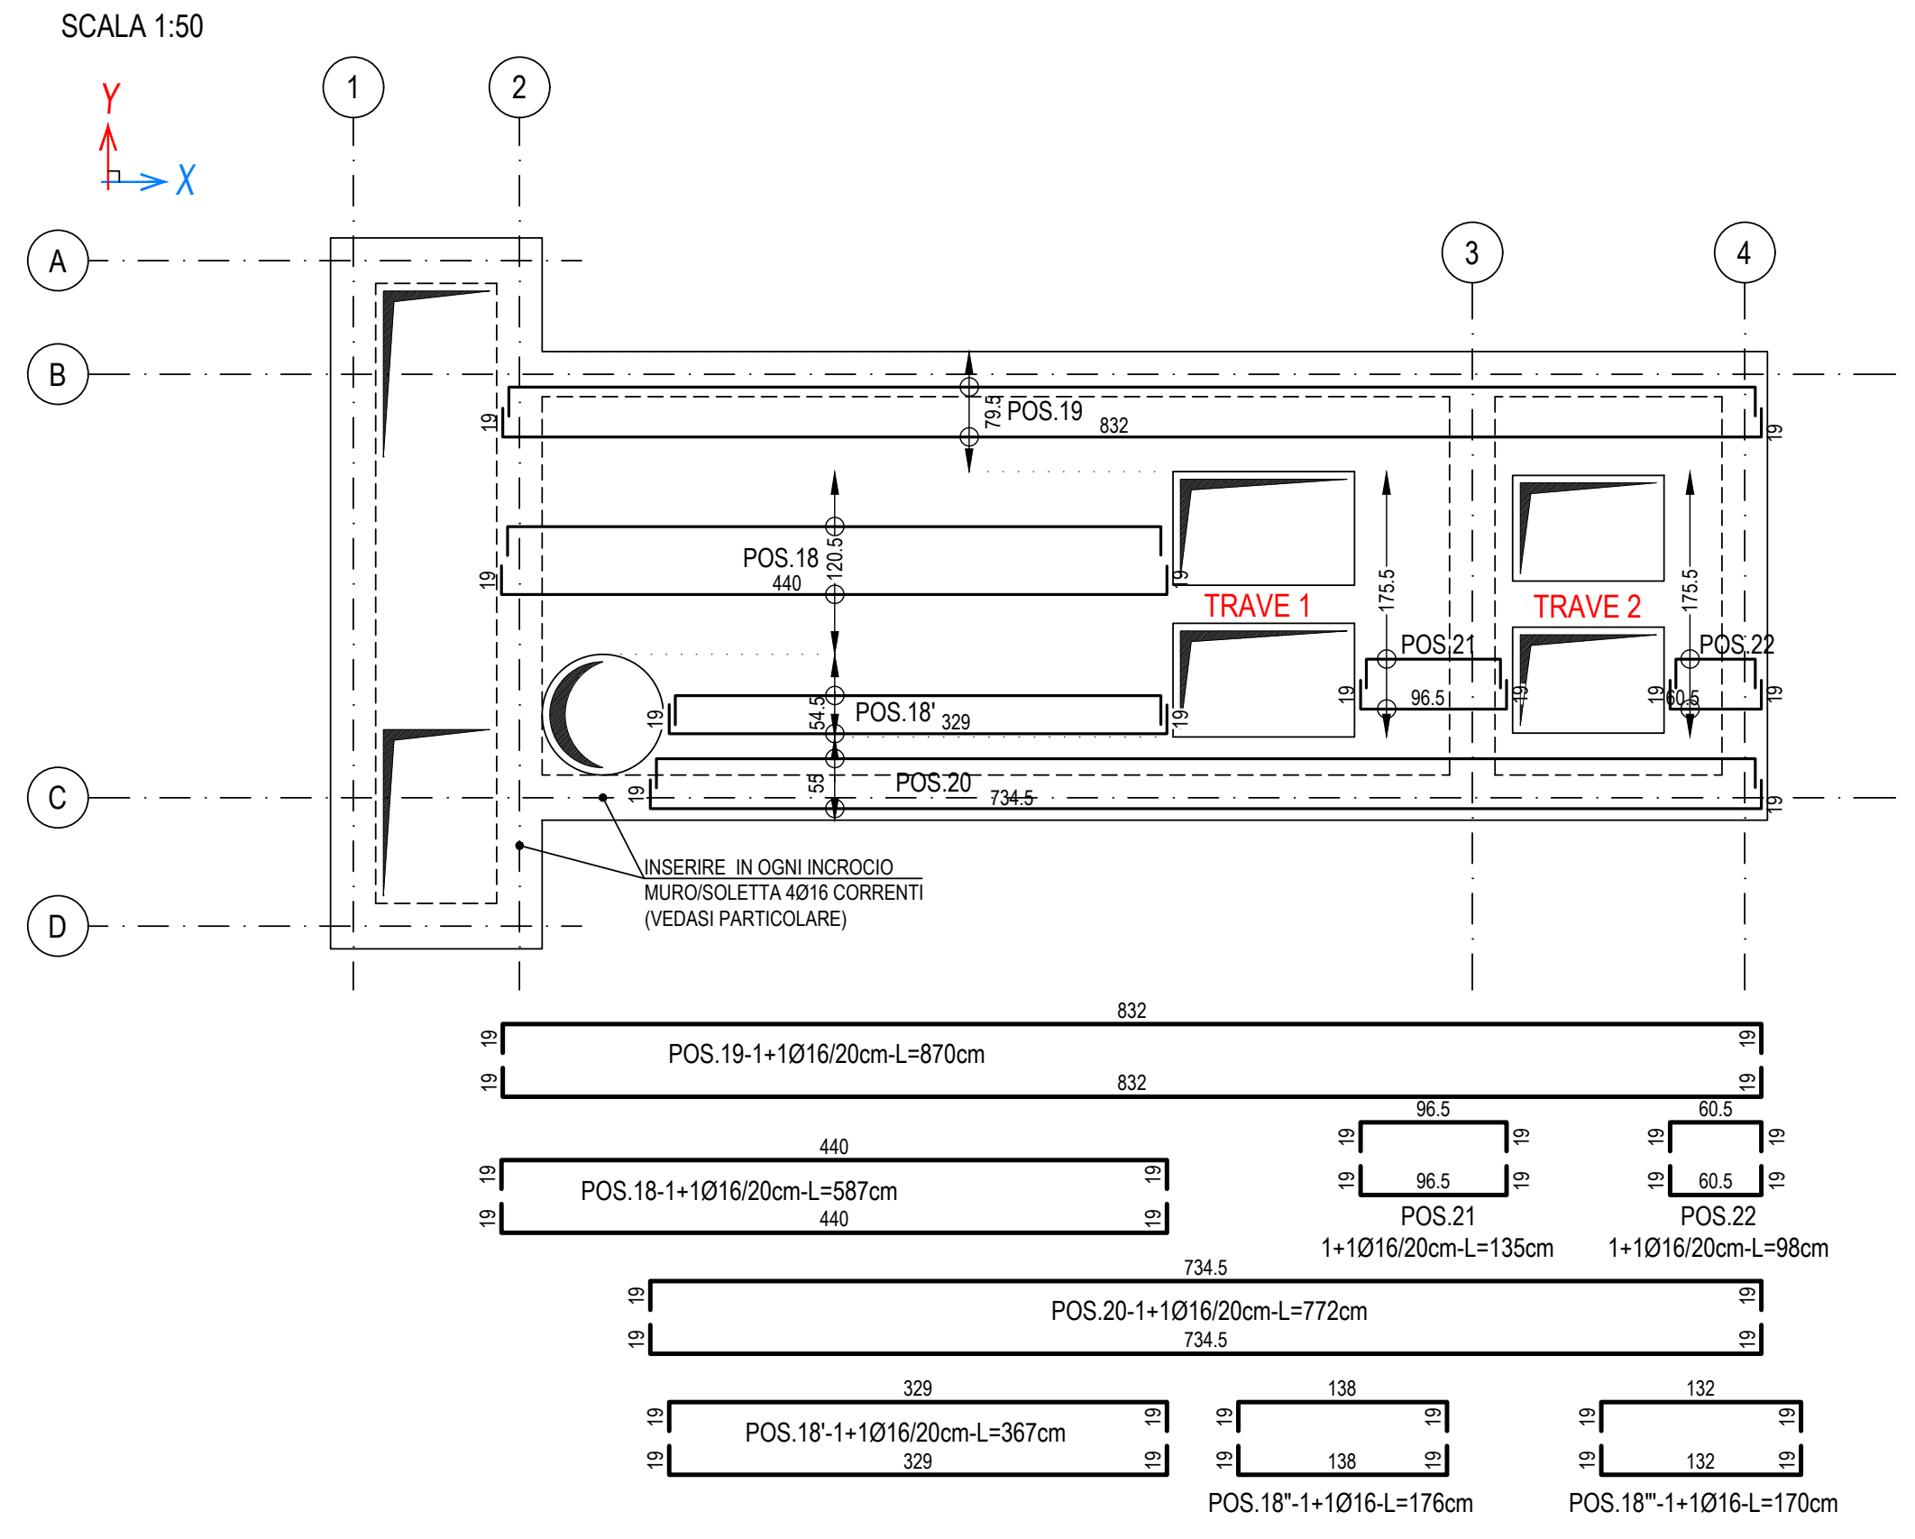
TRAVE 1
TRAVE 2
INSERIRE IN OGNI INCROCIO MURO/SOLETTA 4Ø16 CORRENTI (VEDASI PARTICOLARE)
POS.19-1+1Ø16/20cm-L=870cm
POS.18-1+1Ø16/20cm-L=587cm
POS.20-1+1Ø16/20cm-L=772cm
POS.18'-1+1Ø16/20cm-L=367cm
POS.21 1+1Ø16/20cm-L=135cm
POS.22 1+1Ø16/20cm-L=98cm
POS.18"-1+1Ø16/20cm-L=176cm
POS.18"'-1+1Ø16/20cm-L=170cm

PARTICOLARE - ESEMPIO TIPOLOGICO INCROCIO MURO-SOLETTA SEZIONE VERTICALE
SCALA 1:10

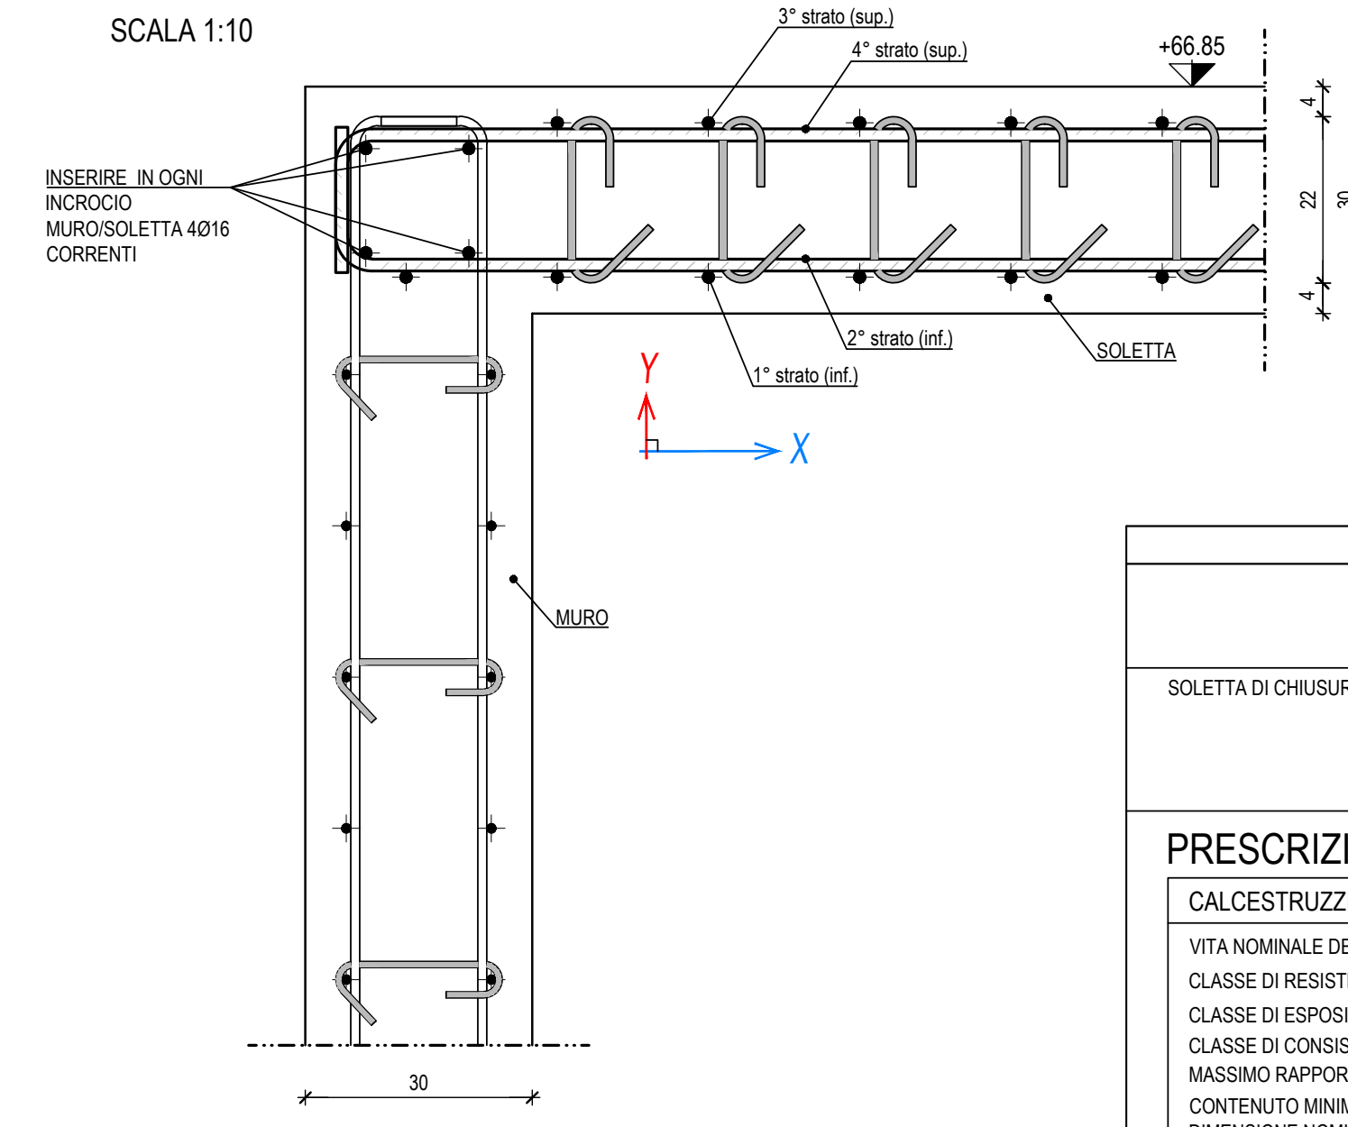

PIANTA ARMATURA INTEGRATIVA SOLETTA DI CHIUSURA SUPERIORE sp. 30cm QUOTA +66.85m (DIREZIONE Y)
SCALA 1:50

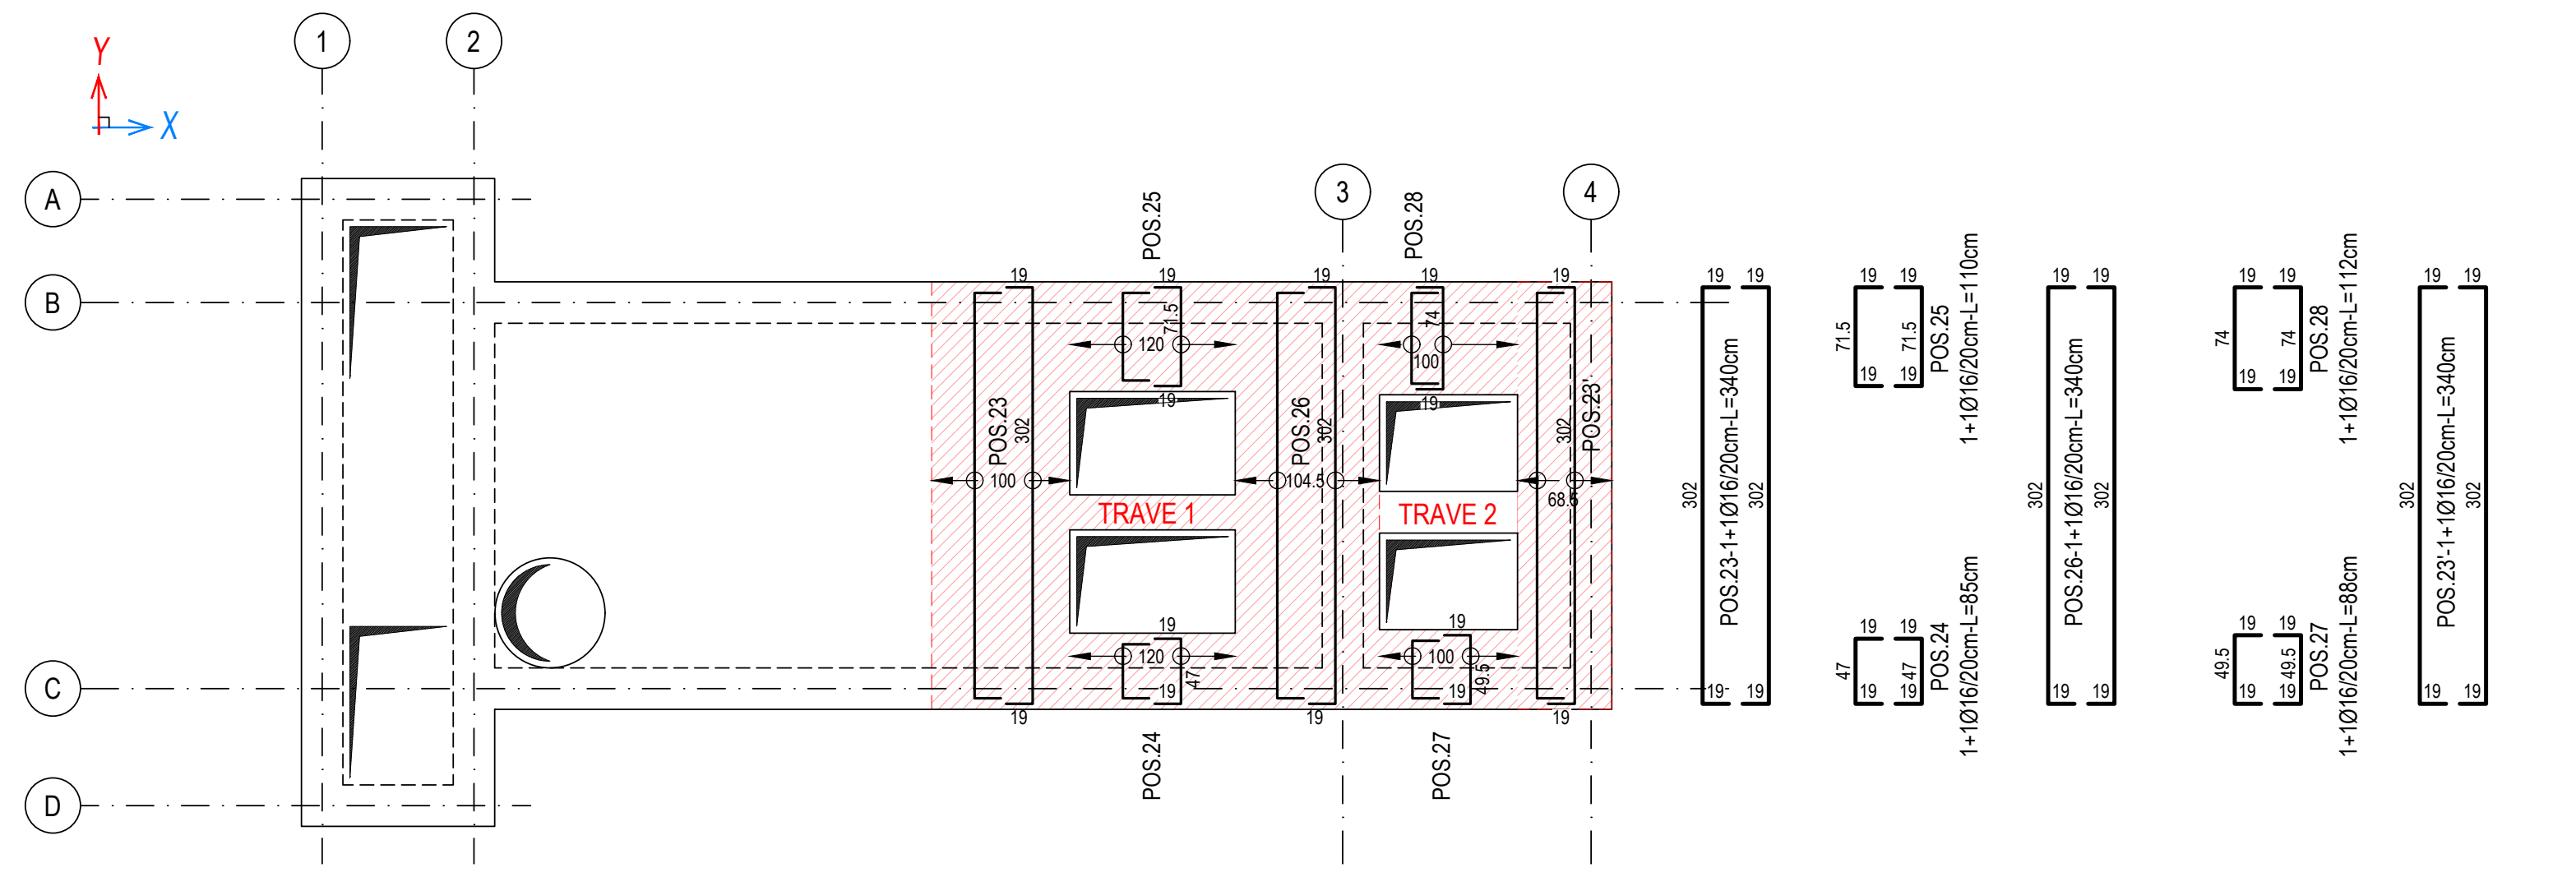

PIANTA ARMATURA INTEGRATIVA SOLETTA DI CHIUSURA SUPERIORE sp. 30cm QUOTA +66.85m (DIREZIONE X)
SCALA 1:50

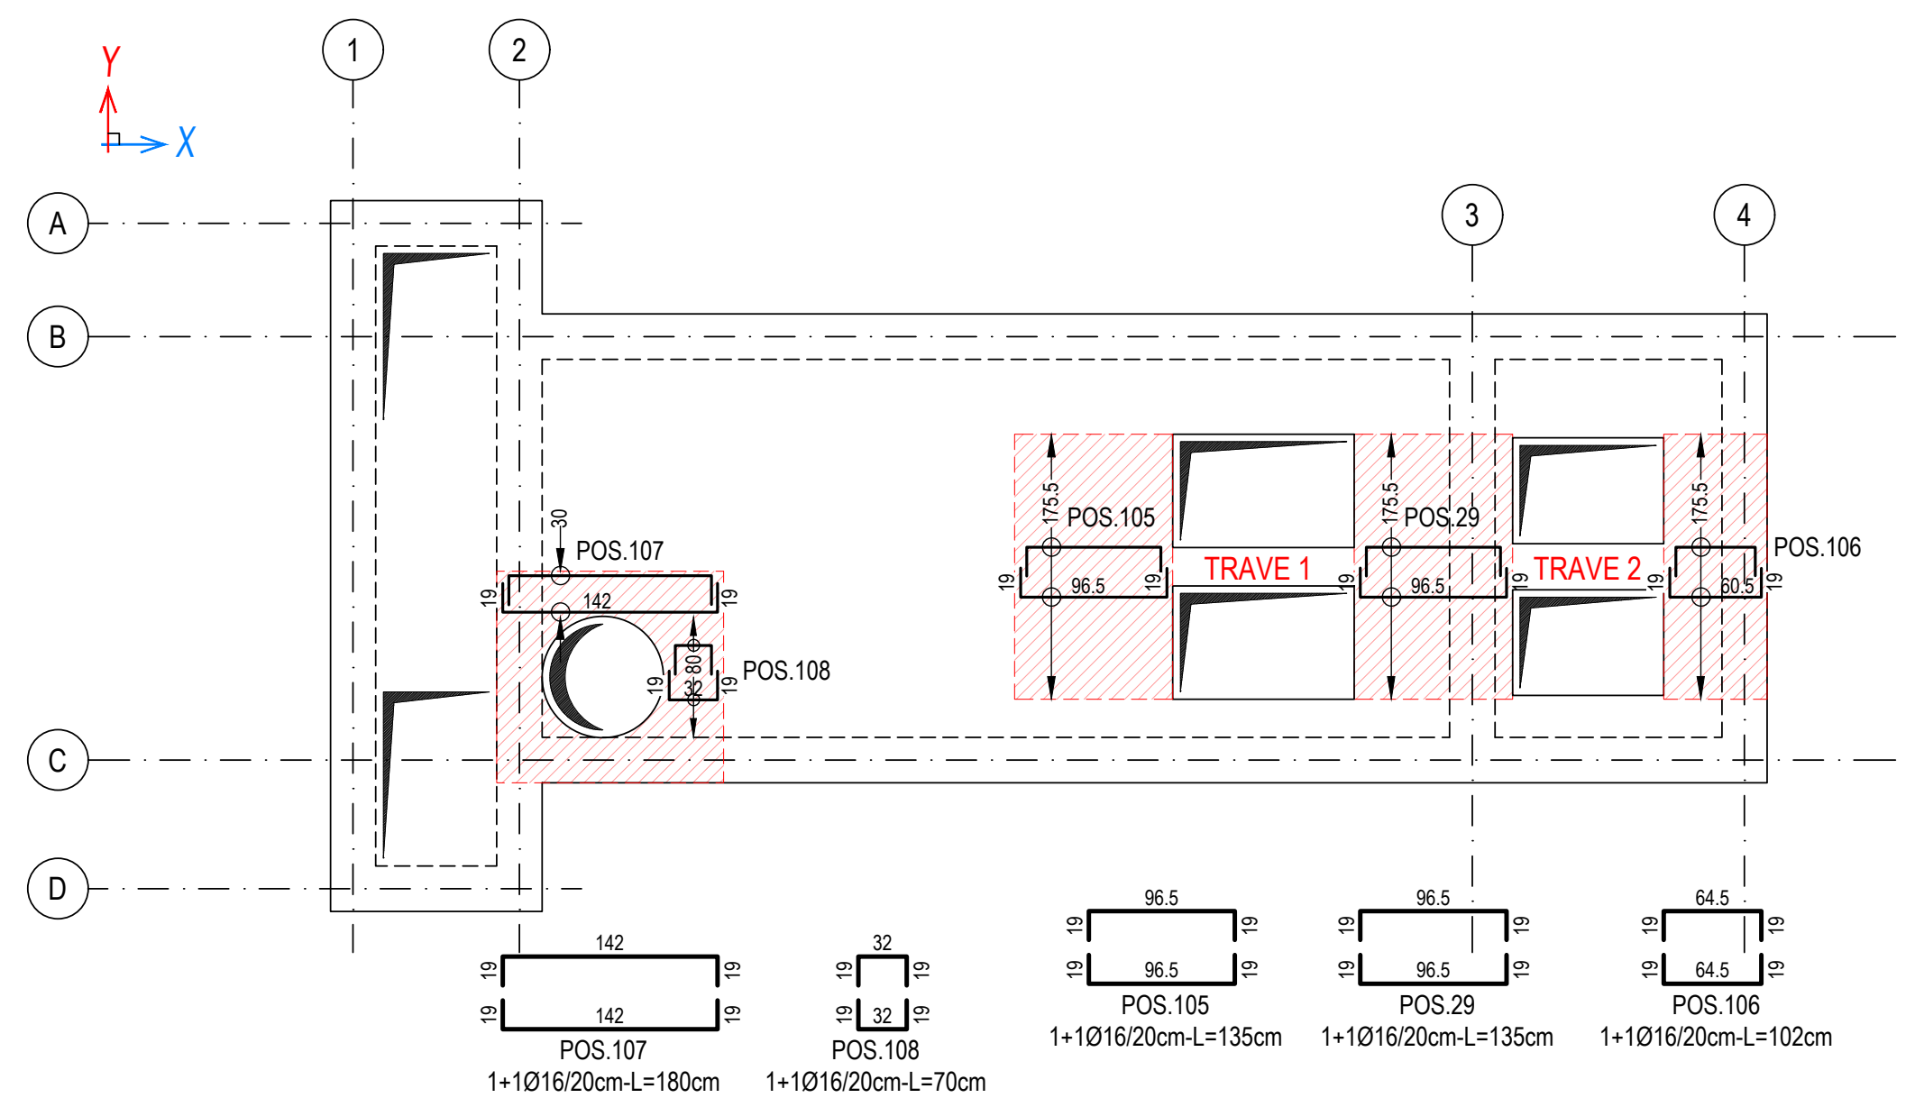
TRAVE 1
TRAVE 2
POS.105
POS.29
POS.106
POS.107
POS.108
POS.107 1+1Ø16/20cm-L=180cm
POS.108 1+1Ø16/20cm-L=70cm
POS.105 1+1Ø16/20cm-L=135cm
POS.29 1+1Ø16/20cm-L=135cm
POS.106 1+1Ø16/20cm-L=102cm

PIANTA ARMATURA GANCI SOLETTA DI CHIUSURA SUPERIORE sp. 30cm QUOTA +66.85m
SCALA 1:50

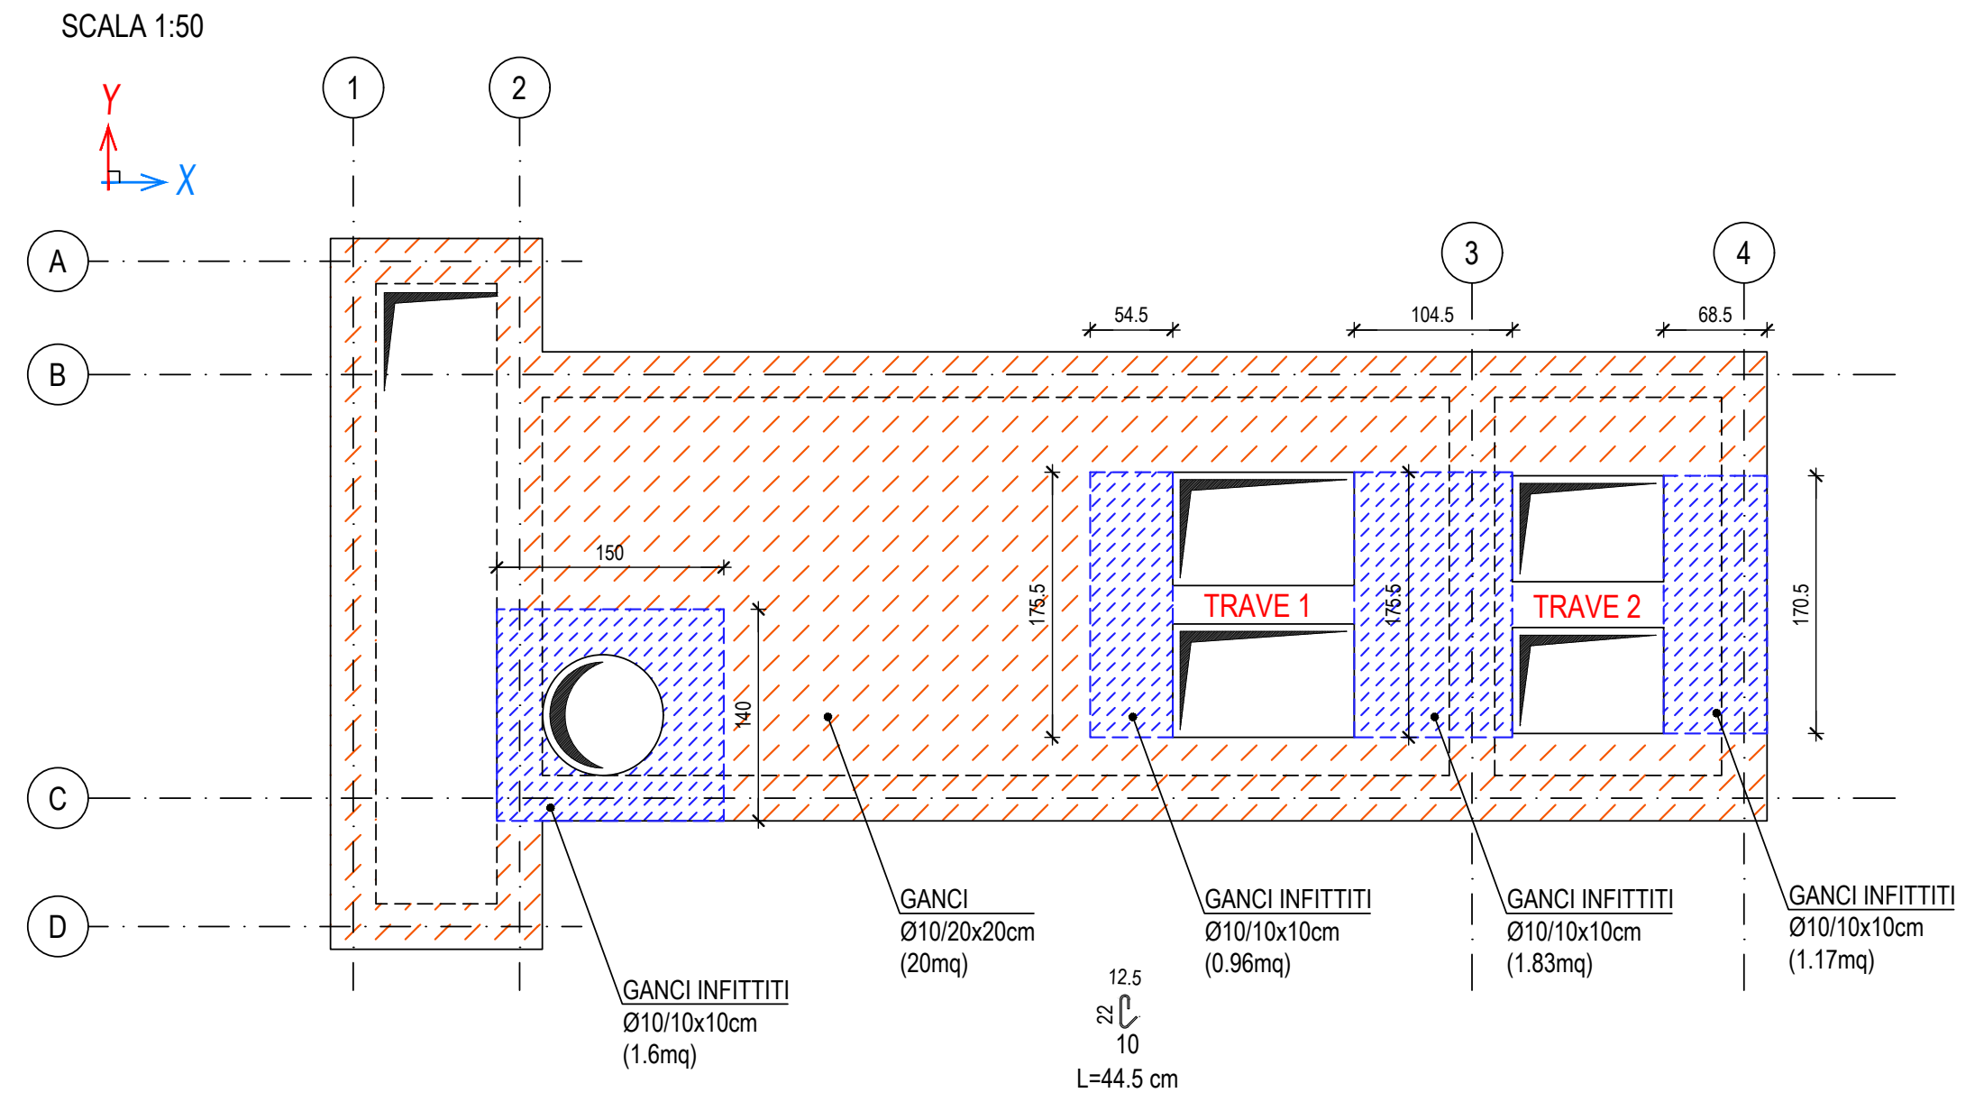
TRAVE 1
TRAVE 2
GANCI INFITTITI Ø10/10x10cm (1.6mq)
GANCI Ø10/20x20cm (20mq)
GANCI INFITTITI Ø10/10x10cm (0.96mq)
GANCI INFITTITI Ø10/10x10cm (1.83mq)
GANCI INFITTITI Ø10/10x10cm (1.17mq)
L=44.5 cm

Trave: 1

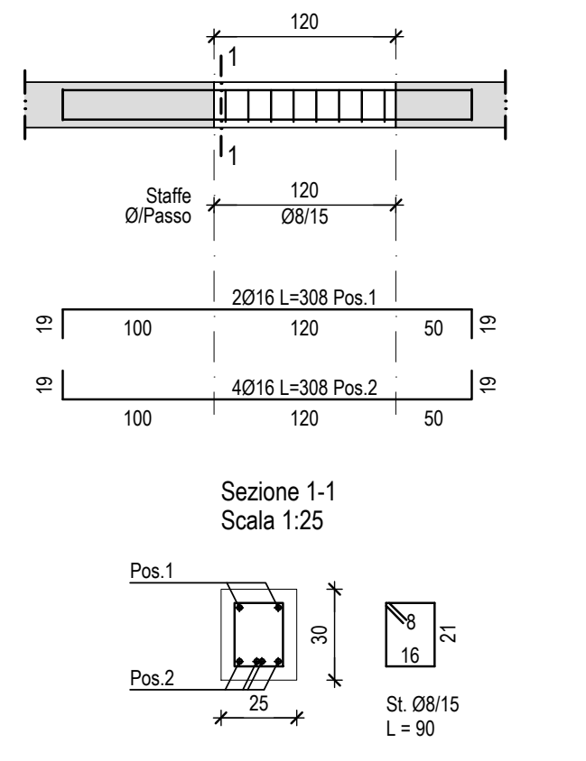

Trave: 2

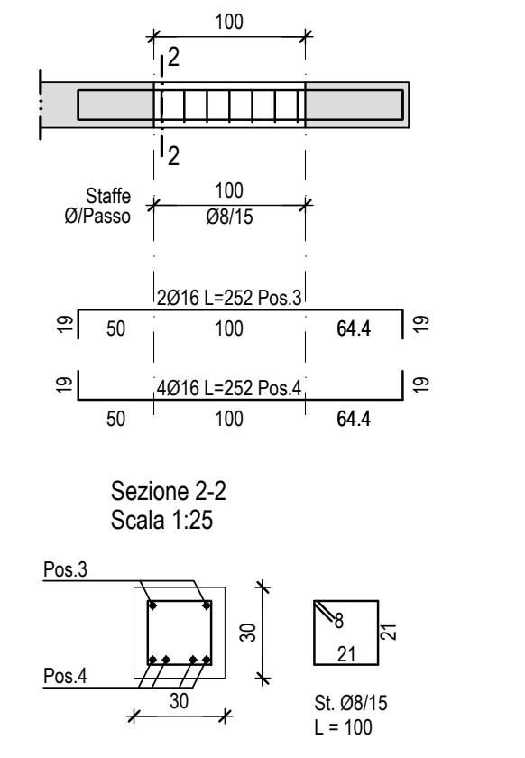

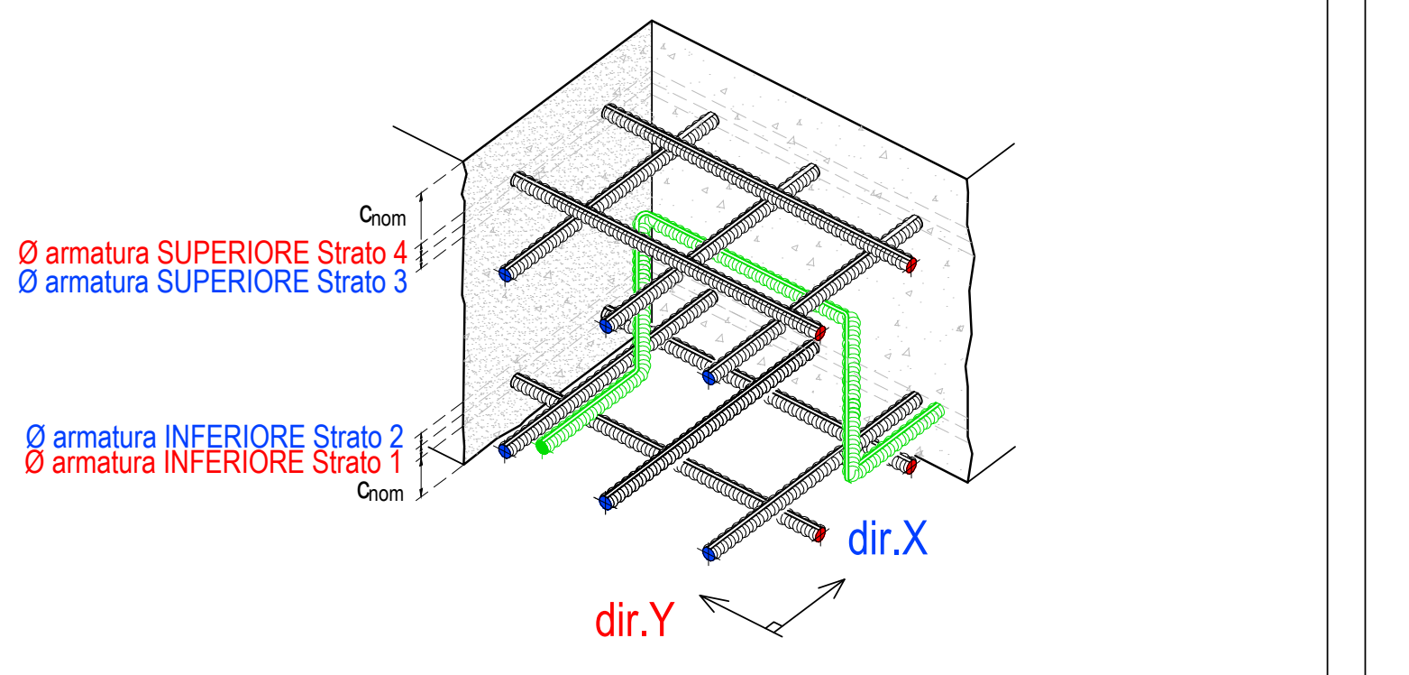
cnom
Ø armatura SUPERIORE Strato 4
Ø armatura SUPERIORE Strato 3
Ø armatura INFERIORE Strato 2
Ø armatura INFERIORE Strato 1
cnom
dir.X
dir.Y

PARTICOLARE
DISPOSIZIONE ARMO PARETI sp. 30cm
PIANTA SCALA 1:25

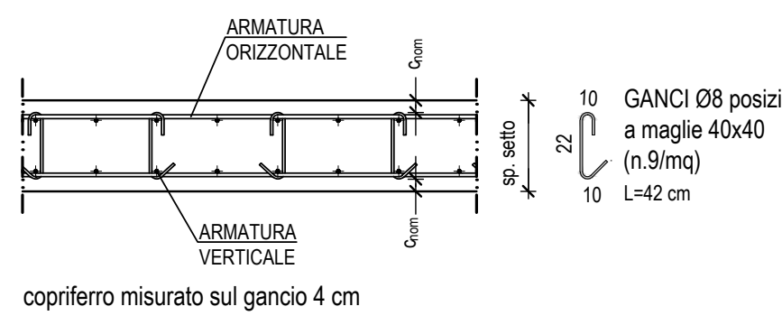

copriferro misurato sul gancio 4 cm

ARMATURA orizz. Ø12/20, vert. Ø12/20 (su entrambe le facce)

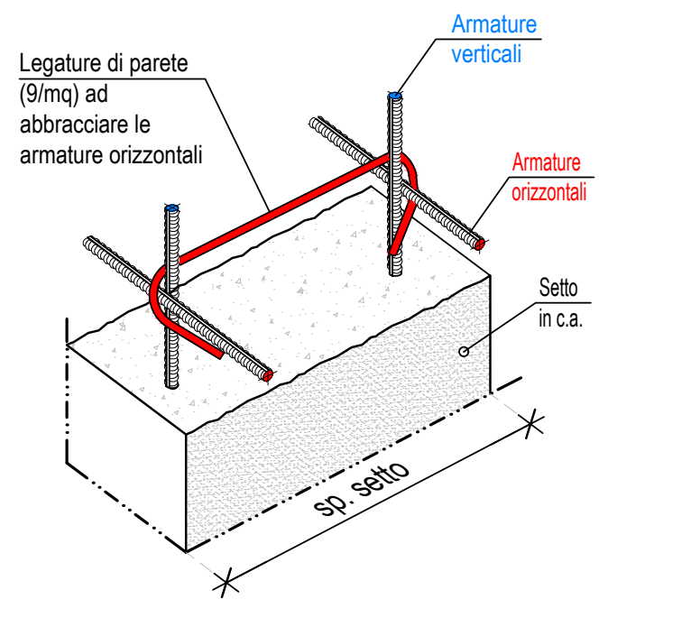
Legature di parete (9/mq) ad abbracciare le armature orizzontali
Armature verticali
Armature orizzontali
Setto in c.a.
sp. setto

CARICHI DI PROGETTO

	TIPOLOGIA	CARICHI PERMANENTI	CARICHI ACCIDENTALI
SOLETTA DI CHIUSURA	ACCIDENTALE DISTRIBUITO ACCIDENTALE CONCENTRATO	- -	9.00 kN/mq 150 kN/ruota
	PERMANENTE PORTATO NEVE	2.00 kN/mq -	- kN/mq 0.80 kN/mq

PRESCRIZIONI SUI MATERIALI IN OPERA

CALCESTRUZZI PER: PLATEA, MURI, SOLETTE E TRAVI	
VITA NOMINALE DELL'OPERA:	50 anni
CLASSE DI RESISTENZA MINIMA:	C32/40
CLASSE DI ESPOSIZIONE (UNI EN 206 / UNI 11104):	XC4+XA2
CLASSE DI CONSISTENZA (UNI EN 206 / UNI 11104):	S4
MASSIMO RAPPORTO A/C (UNI EN 206 / UNI 11104):	0.50
CONTENUTO MINIMO DI CEMENTO (UNI EN 206 / UNI 11104):	340 kg/mc
DIMENSIONE NOMINALE MAX INERTI:	20 mm

ACCIAIO PER CALCESTRUZZO ARMATO
- ACCIAIO IN BARRE AD ADERENZA MIGL. TIPO B450C CONTROLLATO IN STABILIMENTO

COPRIFERRI (se non espressamente indicato negli elaborati)
- COPRIFERRO NOMINALE PER PLATEA, MURI E SOLETTE: 40mm
- COPRIFERRO NOMINALE PER TRAVI: 45mm

LEGENDA

▭	ELEMENTI DI PROGETTO ARCHITETTONICO	▨	ELEMENTI IN MURATURA SEZIONATI
▨	MURATURE PORTANTI IN LATERIZIO SEZIONATE	▭	ELEMENTI VISTI IN PROSPETTO
═	MURATURE NON STRUTTURALI	▨	ELEMENTI IN ACCIAIO SEZIONATI
▩	ELEMENTI IN LEGNO SEZIONATI	▭	TRAVI E CORDOLI
▩	ELEMENTI IN C.A. SEZIONATI	◩	FORI SU SOLAIO
■	ELEMENTI IN C.A. SOTTOSTANTI AL SOLAIO CONSIDERATO		
☒ ○	IMPIANTI (TUBAZIONI SERVIZI IGIENICI, ECC)	-··-··	LINEE DI INTERRUZIONE DISEGNO
±0.00 ⊕ ±0.00 ▽	QUOTE ALTIMETRICHE AL FINITO IN PIANTA/SEZIONE		
±0.00 ◐ ±0.00 ▼	QUOTE ALTIMETRICHE AL GREZZO IN PIANTA/SEZIONE		

PIEGATURE ARMATURA

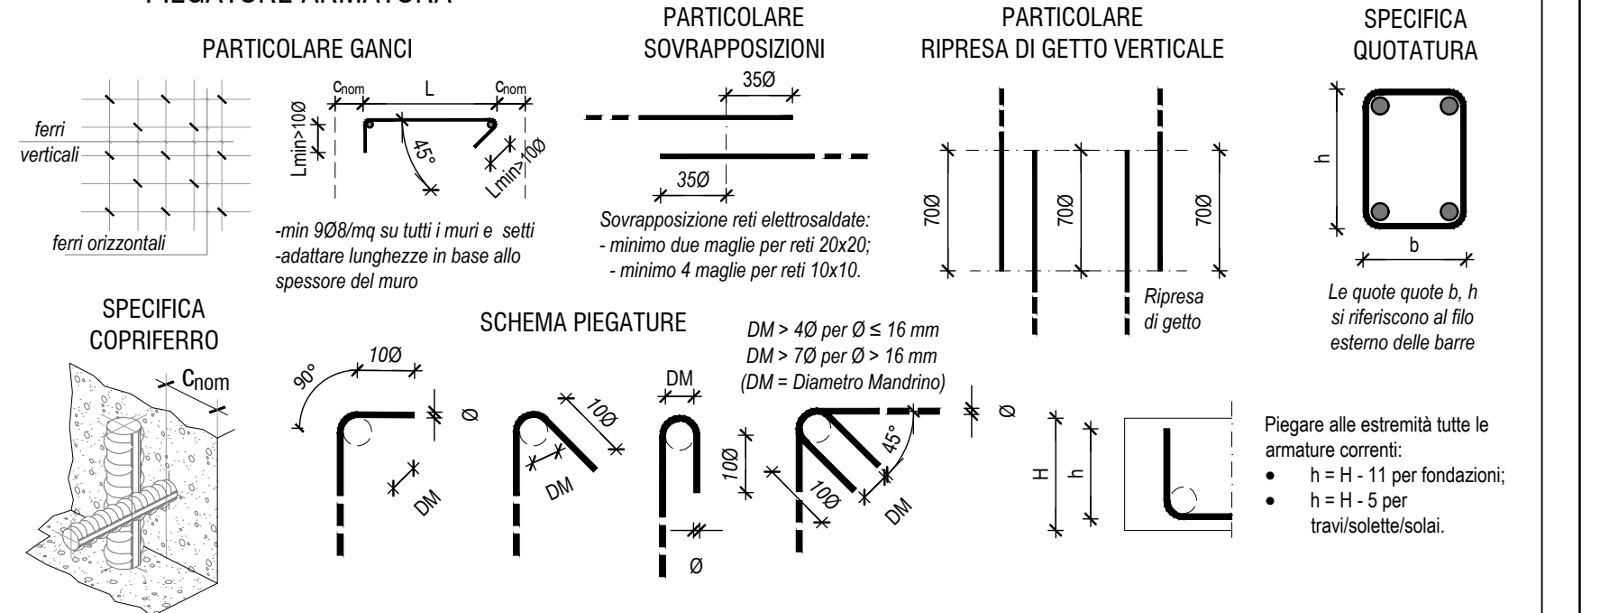

PARTICOLARE GANCI
-min 9Ø8/mq su tutti i muri e setti
-adattare lunghezze in base allo spessore del muro

PARTICOLARE SOVRAPPOSIZIONI
Sovrapposizione reti elettrosaldate:
- minimo due maglie per reti 20x20;
- minimo 4 maglie per reti 10x10.

PARTICOLARE RIPRESA DI GETTO VERTICALE

SPECIFICA QUOTATURA
Le quote quote b, h si riferiscono al filo esterno delle barre

SPECIFICA COPRIFERRO

SCHEMA PIEGATURE
DM > 4Ø per Ø ≤ 16 mm
DM > 7Ø per Ø > 16 mm
(DM = Diametro Mandrino)

Piegare alle estremità tutte le armature correnti:
- h = H - 11 per fondazioni;
- h = H - 5 per travi/solette/solai.

NORMATIVA: D.M. 17/01/2018 (Norme Tecniche per le costruzioni)
AZIONE SISMICA - IDENTIFICAZIONE DEL SITO E PARAMETRI DI CALCOLO

LOCALITA'	BARDOLINO (VR)
LONGITUDINE (WGS84)	10,7125
LATITUDINE (WGS84)	45,5630
VITA NOMINALE V_N	50 anni
CLASSE D'USO	II - C_U = 1,0
CATEGORIA TOPOGRAFICA	T1
CATEGORIA SOTTOSUOLO	Tipo C

NORMATIVA DI RIFERIMENTO:
- D.M. 17/01/2018 (Norme Tecniche per le costruzioni);
- C.Min. del 21 Gennaio 2019;
- UNI EN 1990 - “Criteri generali di progettazione strutturale”;
- UNI EN 1991 - “Azioni sulle strutture”;
- UNI EN 1992 - “Progettazione delle strutture in calcestruzzo”;
- UNI EN 1993 - “Eurocodice 3 - Progettazione delle strutture in acciaio”;
- UNI EN 1997 - “Progettazione geotecnica”;
- UNI EN 1998 - “Progettazione delle strutture per la resistenza sismica”;
- L. 5 Novembre 1971 n. 1086;
- REGOLAMENTO 305/2011-REGOLAMENTO 2024/3110;
- UNI EN 206:2021;
- UNI 11104:2025

NOTE :
- PER MAGGIORI INFORMAZIONI SI RIMANDA ALLA RELAZIONE DI CALCOLO E RELATIVE SPECIFICHE TECNICHE;
- L'ANALISI DEI CARICHI UTILIZZATA PER IL DIMENSIONAMENTO DELLE STRUTTURE E' CONTENUTA NELLA RELAZIONE DI CALCOLO. VERIFICARE LA CORRISPONDENZA TRA I CARICHI PERMANENTI PREVISTI NELLA RELAZIONE E LE FINITURE RIPORTATE NEGLI ELABORATI ARCHITETTONICI;
- EVENTUALI FORI DI PASSAGGIO IMPIANTI SULLE STRUTTURE PORTANTI DEVONO ESSERE PREVENTIVAMENTE COMUNICATI ED AUTORIZZATI DALLA D.L. DELLE OPERE STRUTTURALI.
- GLI ESECUTIVI STRUTTURALI SONO DA LEGGERSI UNITAMENTE A QUELLI ARCHITETTONICI ED IMPIANTISTICI. EVENTUALI DIFFERENZE PRESENTI TRA GLI ELABORATI DELLE VARIE DISCIPLINE DEVONO ESSERE COMUNICATE TEMPESTIVAMENTE AL DIRETTORE DEI LAVORI. I PROGETTISTI NON SONO RESPONSABILI DI TUTTE LE MODIFICHE APPORTATE SUCCESSIVAMENTE ALLA CONSEGNA UFFICIALE DEL PROGETTO ESECUTIVO CHE NON HANNO OTTENUTO IL RELATIVO BENESTARE

AZIENDA GARDESANA SERVIZI
ags azienda gardesana servizi

"INTERVENTI DI RIQUALIFICAZIONE DEL SISTEMA DI RACCOLTA DEI REFLUI NEL BACINO DEL LAGO DI GARDA - SPONDA VERONESE"
Lotto 1 - Tratto 4 - 2°Stralcio
"OPERE COLLETTORE IN PRESSIONE ED OPERE COMPLEMENTARI TRATTO PERGOLANA - ROCCA VELA - COMUNE BARDOLINO"
Lotto 8 - Tratto 4_OC
CIG: B7E3B750B2 - CUP: J33F17000010002

PROGETTO ESECUTIVO

PROGETTISTA E COORDINATORE SICUREZZA IN FASE DI PROGETTO:
Ing. Giovanni Battista Matteotti

COLLABORAZIONE:
Ing. Luca Petracin
Ing. Andrea Martinello
Ing. Emanuele Anderlini
Ing. Filiberto Boscolo Lisetto
Geom. Elisa Zatti

mass
INGEGNERIA E ARCHITETTURA SRL
Via Sorio 33/a, 35141 PADOVA
Tel: 049-723320 - Mail: Info@matteotti.com

ING. G.B. MATTEOTTI

RESPONSABILE UNICO DEL PROGETTO:
Dott. Ing. Carlo Alberto Voi

TITOLO	*SCALA*	*CODICE ELABORATO*
OPERE STRUTTURALI - NUOVO IMPIANTO DI SOLLEVAMENTO DI ROCCA VELA - tav. 1/2	1:50 - 1:25 - 1:10	C-01-001

N° REV	*DATA*	*DESCRIZIONE*	*ESEGUITO*	*VERIFICATO*	*APPROVATO*
00	Marzo 2026	PRIMA EMISSIONE	Ing. M. Dal Bò	Ing. L. Petracin	Ing. G. B. Matteotti
01	Luglio 2026	AGGIORNAMENTO POST VERIFICA AGS	Ing. M. Dal Bò	Ing. L. Petracin	Ing. G. B. Matteotti
02					
03					
04					