


VASCA ROMPITRATTA
PIANTA MURI – CARPENTERIA
SCALA 1:50

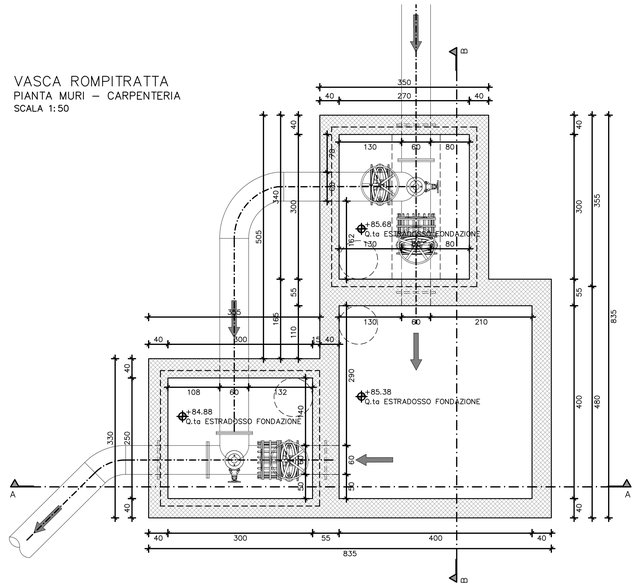


VASCA ROMPITRATTA
PIANTA COPERTURA – CARPENTERIA
SCALA 1:50

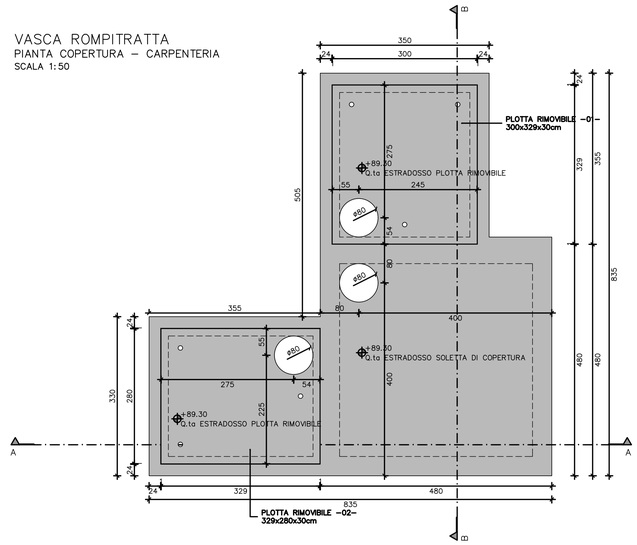

PLOTTA RIMOVIBILE –01–
PIANTA – CARPENTERIA
SCALA 1:50

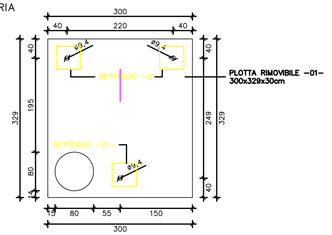

PLOTTA RIMOVIBILE –02–
PIANTA – CARPENTERIA
SCALA 1:50

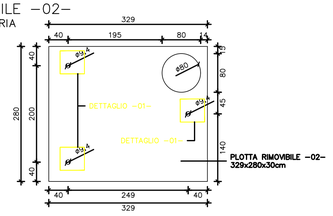

PLOTTA RIMOVIBILE
DETTAGLIO 01 – CARPENTERIA
SCALA 1:10

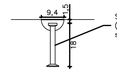


TABELLA MATERIALI

ACCIAIO

ACCIAIO PER C.A.
Rif. DM 17/01/2018

TIPO B450C saldabile:
- Resistenza caratteristica a snervamento: ftk ≥ 450 MPa
- Resistenza caratteristica a rottura: ftk > 540 MPa

*Collegamento di barre d'armatura post-installate (inghisaggio): impiegare ancorante chimico epossidico ad alte prestazioni tipo Hilti HIT-RE 500 v4 o equivalente secondo indicazioni del fornitore

CALCESTRUZZO


CALCESTRUZZO MAGRO
E GETTI DI LIVELLAMENTO

- CLASSE DI RESISTENZA MINIMA: C12/15
- CLASSE DI ESPOSIZIONE AMBIENTALE: X0


CALCESTRUZZO PER OPERE DEFINITIVE
Rif. UNI EN 206

- CLASSE DI CONSISTENZA: S5
- CLASSE DI ESPOSIZIONE AMBIENTALE: XC4+XA2
- RAPPORTO MASSIMO a/c: 0.5
- CONTENUTO DI CLORURI: Cl<0.4
- DIAMETRO MASSIMO DEGLI INERTI: D_{max}=25mm
- CEMENTO RESISTENTE AI SOLFATI
- CLASSE DI RESISTENZA MINIMA: C32/40
- COPRIFERRO NOMINALE: 40 mm

VASCA ROMPITRATTA
SEZIONE A–A – CARPENTERIA
SCALA 1:50

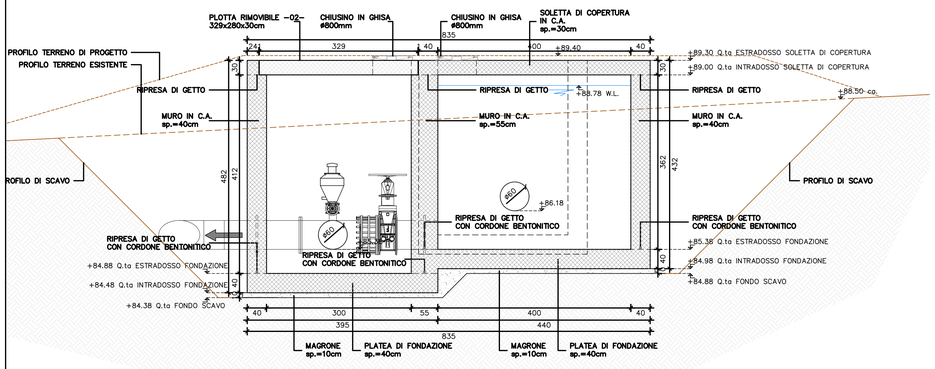

VASCA ROMPITRATTA
SEZIONE B–B – CARPENTERIA
SCALA 1:50

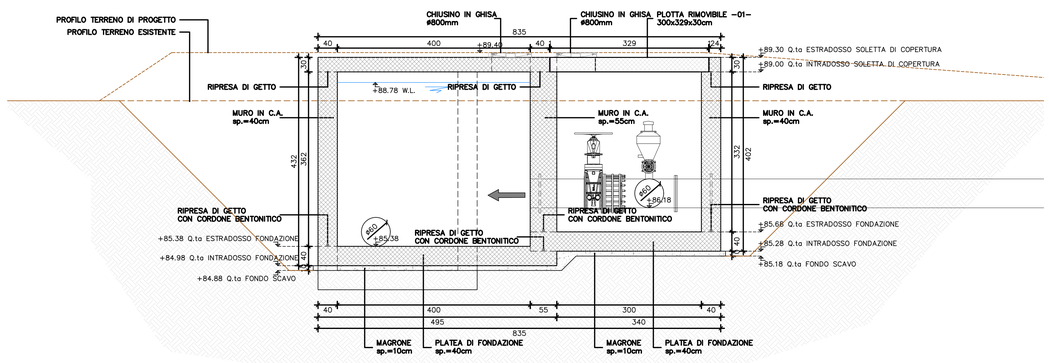

AZIENDA GARDESANA SERVIZI — ags — azienda gardesana servizi

"INTERVENTI DI RIQUALIFICAZIONE DEL SISTEMA DI RACCOLTA DEI REFLUI NEL BACINO DEL LAGO DI GARDA - SPONDA VERONESE"
Lotto 1 - Tratto 4 - 2°Stralcio
"OPERE COLLETTORE IN PRESSIONE ED OPERE COMPLEMENTARI TRATTO PERGOLANA - ROCCA VELA - COMUNE BARDOLINO"
Lotto 8 - Tratto 4_OC
CIG: B7E3B750B2 - CUP: J33F17000010002



PROGETTO ESECUTIVO

PROGETTISTA E COORDINATORE SICUREZZA IN FASE DI PROGETTO:
Ing. Giovanni Battista Matteotti

COLLABORAZIONE:
Ing. Luca Petracin
Ing. Andrea Martinello
Ing. Emanuele Anderlini
Ing. Filiberto Boscolo Lisetto
Geom. Elisa Zatti

mass — INGEGNERIA E ARCHITETTURA SRL
Via Sono 30a, 35141 PADOVA
Tel. 049-723920 - Mail: info@mattetti.com

RESPONSABILE UNICO DEL PROGETTO:
Dott. Ing. Carlo Alberto Voi

TITOLO		*SCALA*	*CODICE ELABORATO*
VASCA ROMPITRATTA - Opere Strutturali - Carpenterie, piante e sezioni		1:50	C-13-002

N° REV.	*DATA*	*DESCRIZIONE*	*ESEGUITO*	*VERIFICATO*	*APPROVATO*
00	Marzo 2026	PRIMA EMISSIONE		Ing. L. Petracin	Ing. G. B. Matteotti
01	Aprile 2026	AGGIORNAMENTO A SEGUITO DI VERIFICA		Ing. L. Petracin	Ing. G. B. Matteotti
02	Luglio 2026	AGGIORNAMENTO POST VERIFICA AGS		Ing. L. Petracin	Ing. G. B. Matteotti
03					
04					