VASCA ROMPITRATTA
PIANTA PLATEE E RIPRESE PARETI - ARMATURA
1:20

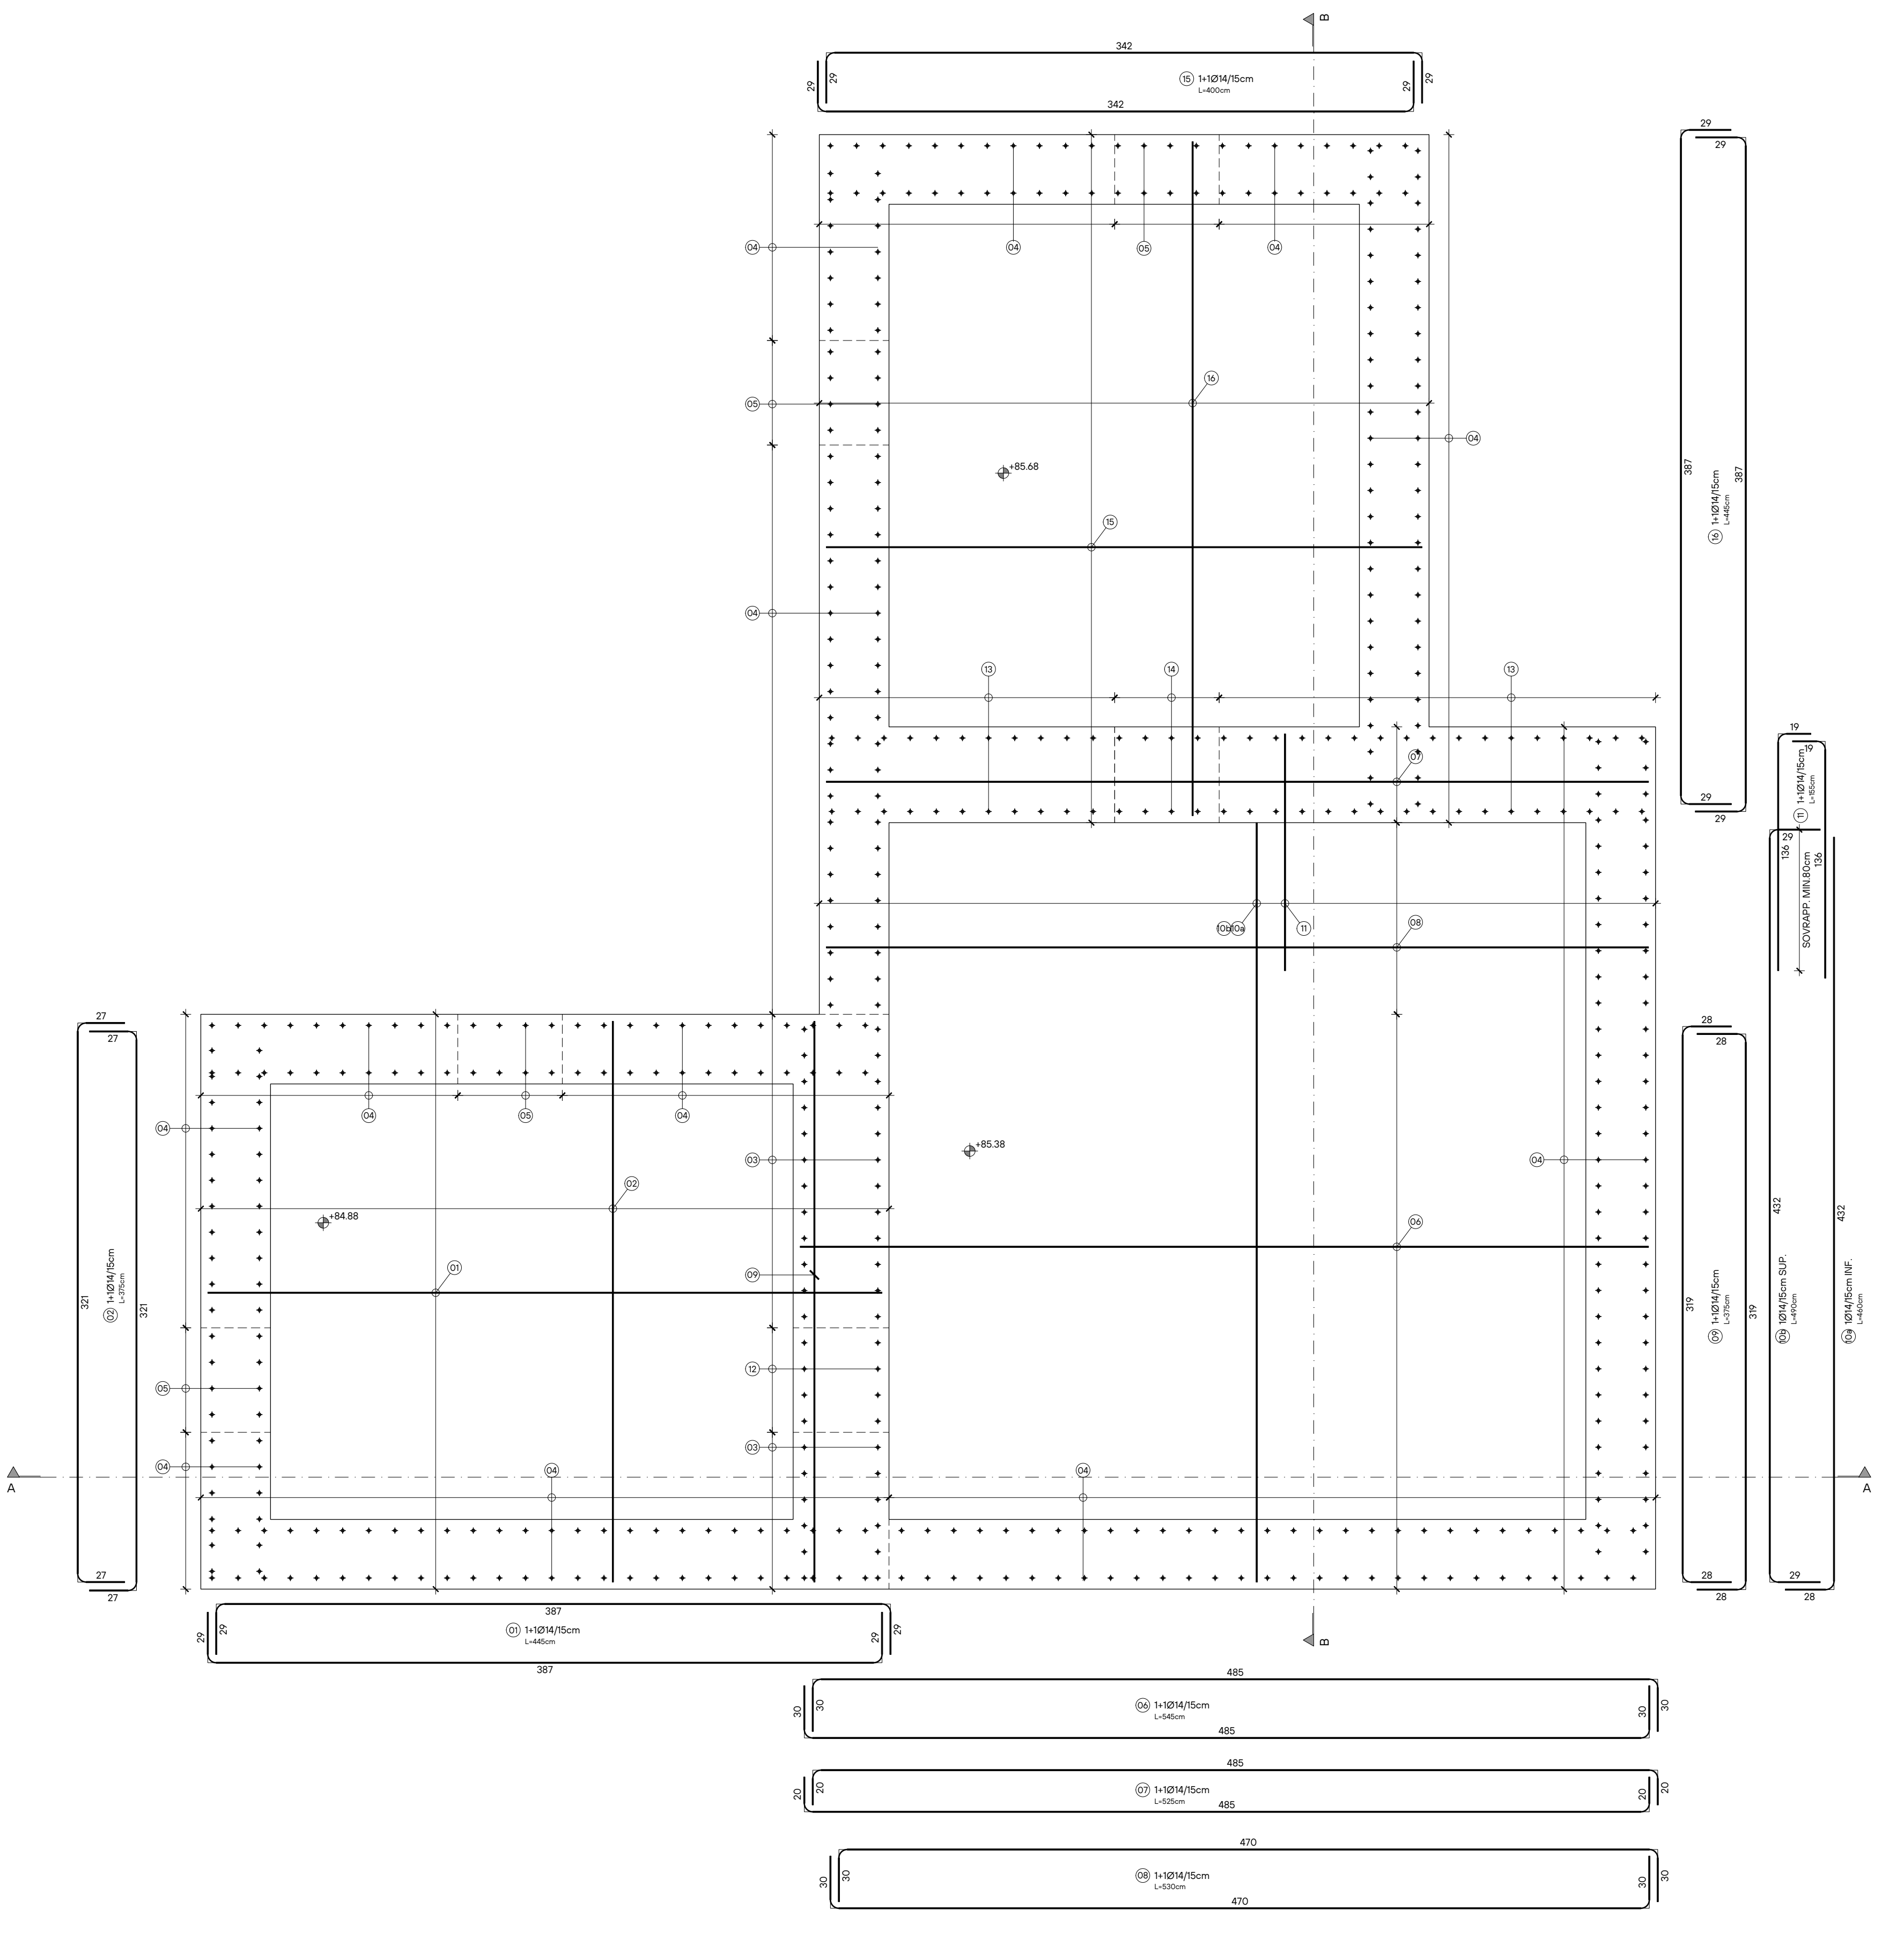

VASCA ROMPITRATTA
PIANTA MURI- ARMATURA
1:20

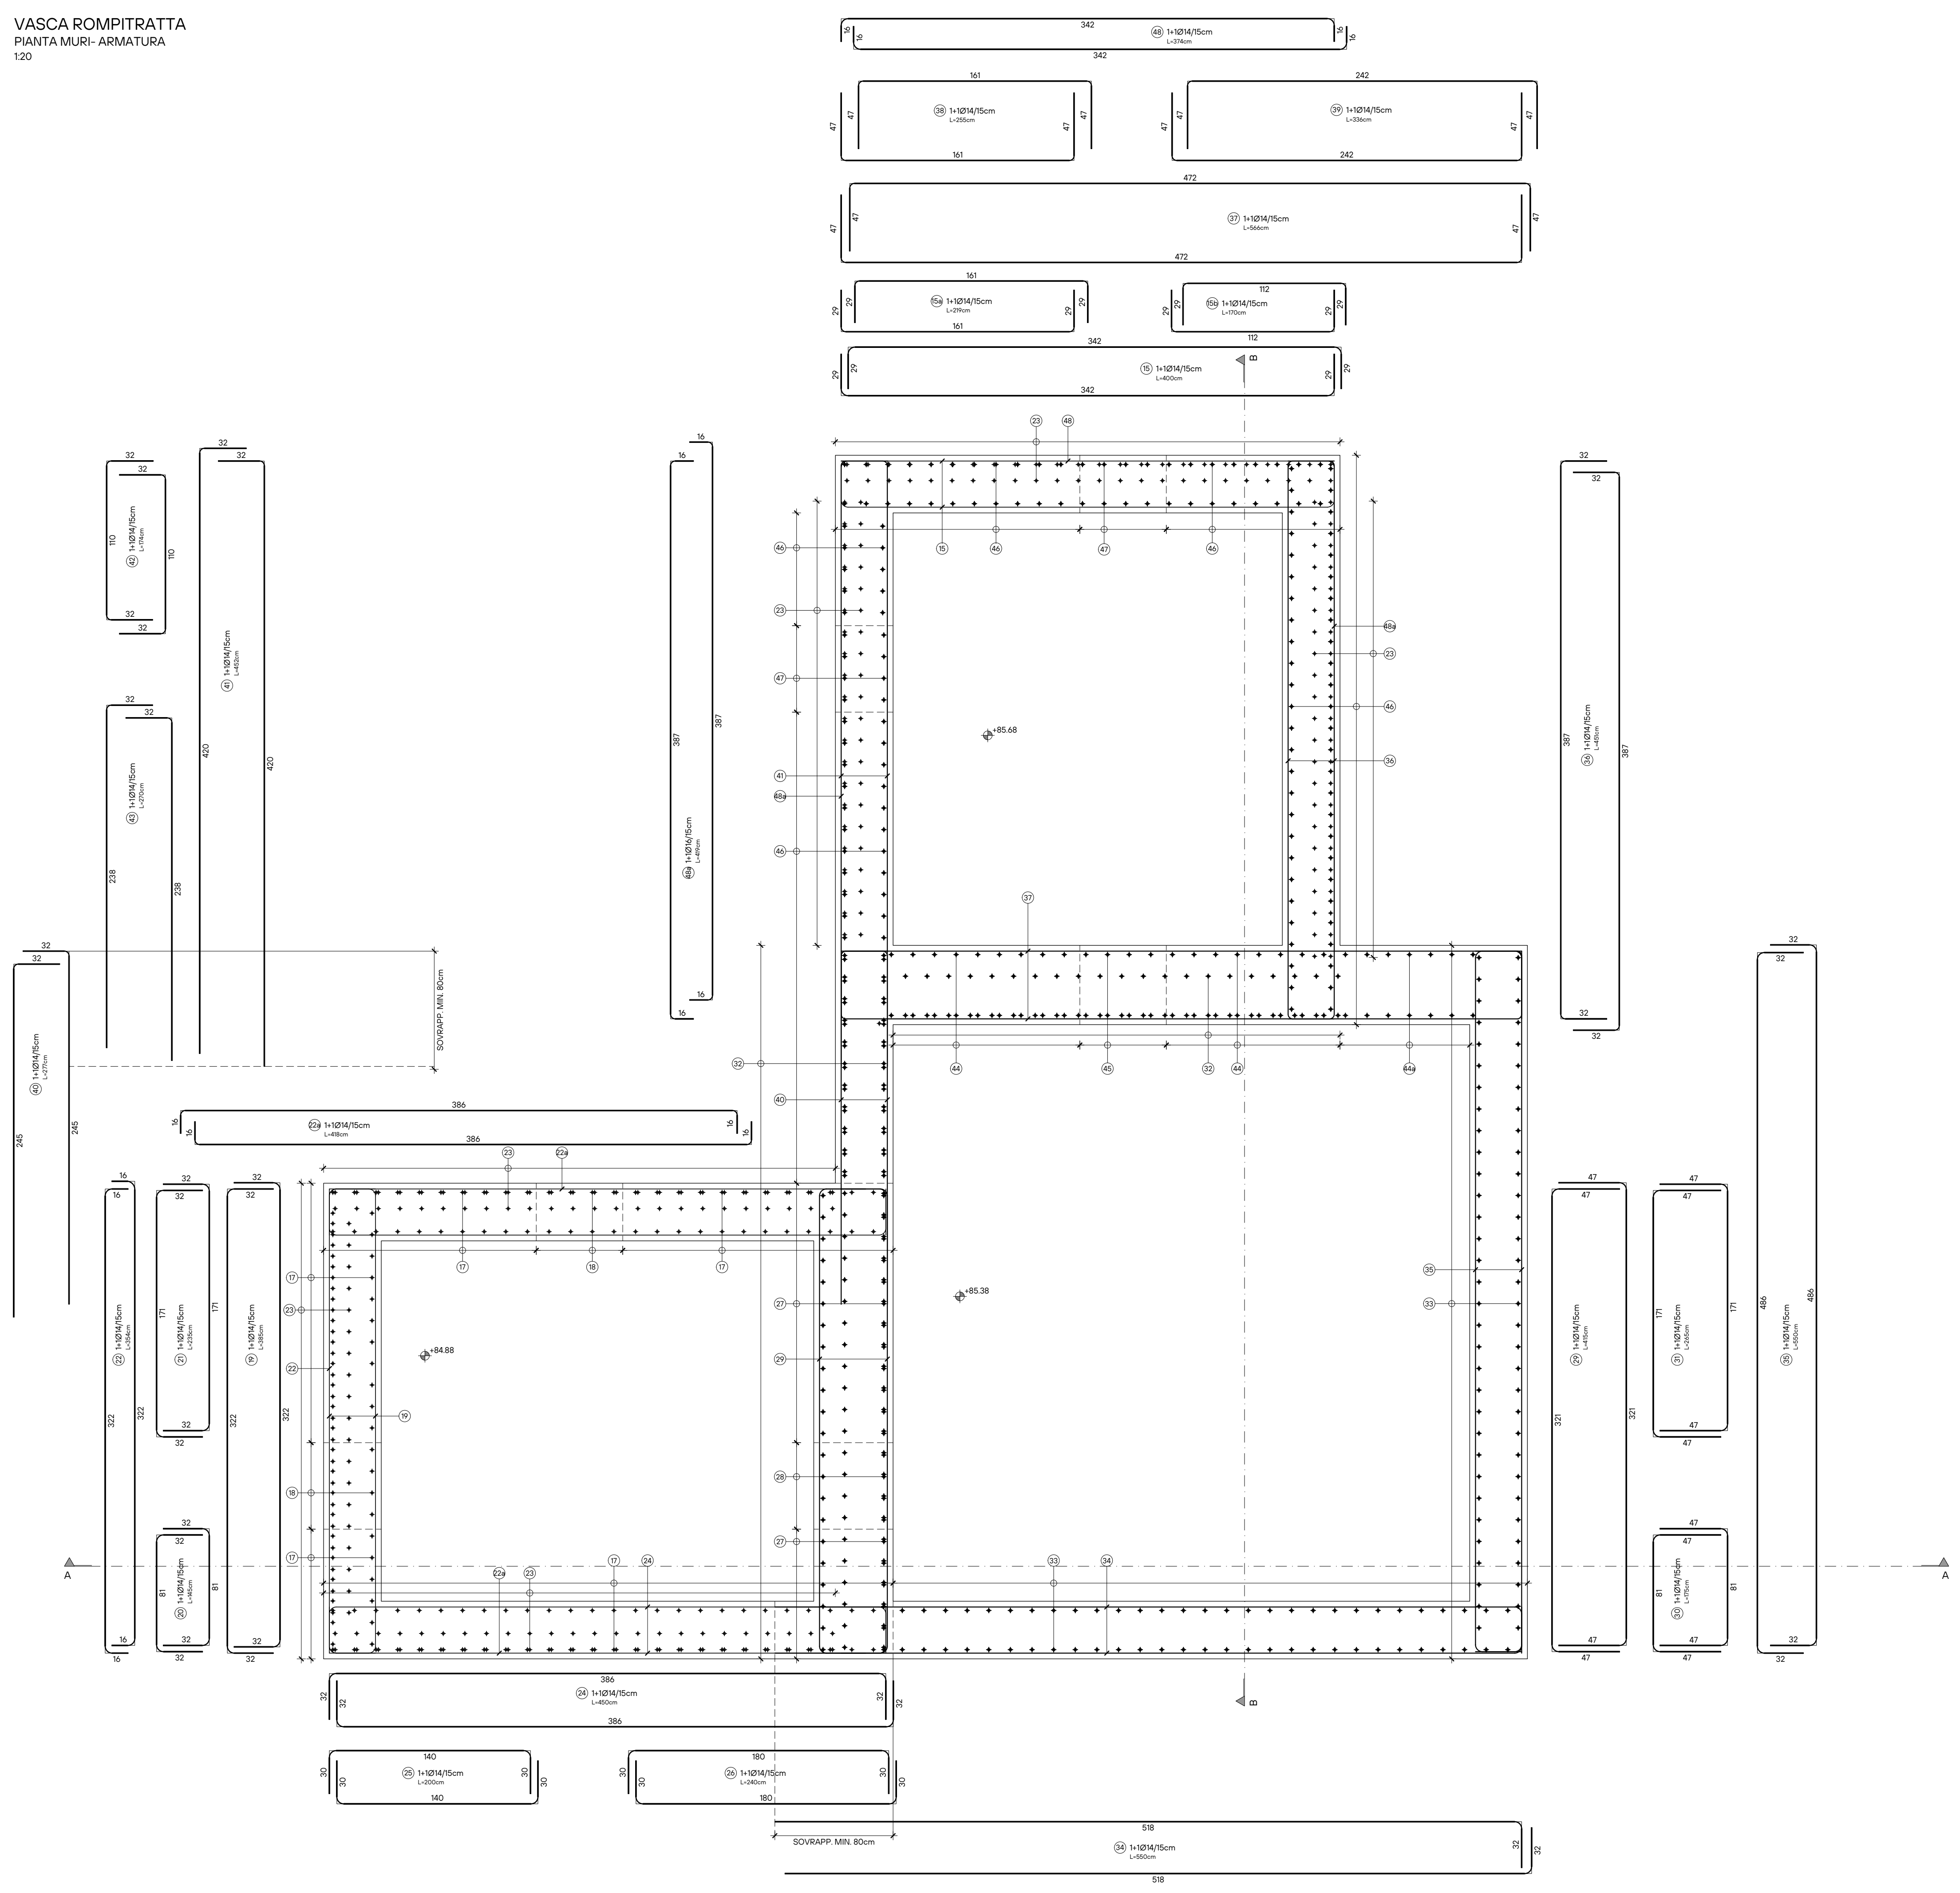

VASCA ROMPITRATTA
SEZIONE A-A - ARMATURA
1:20

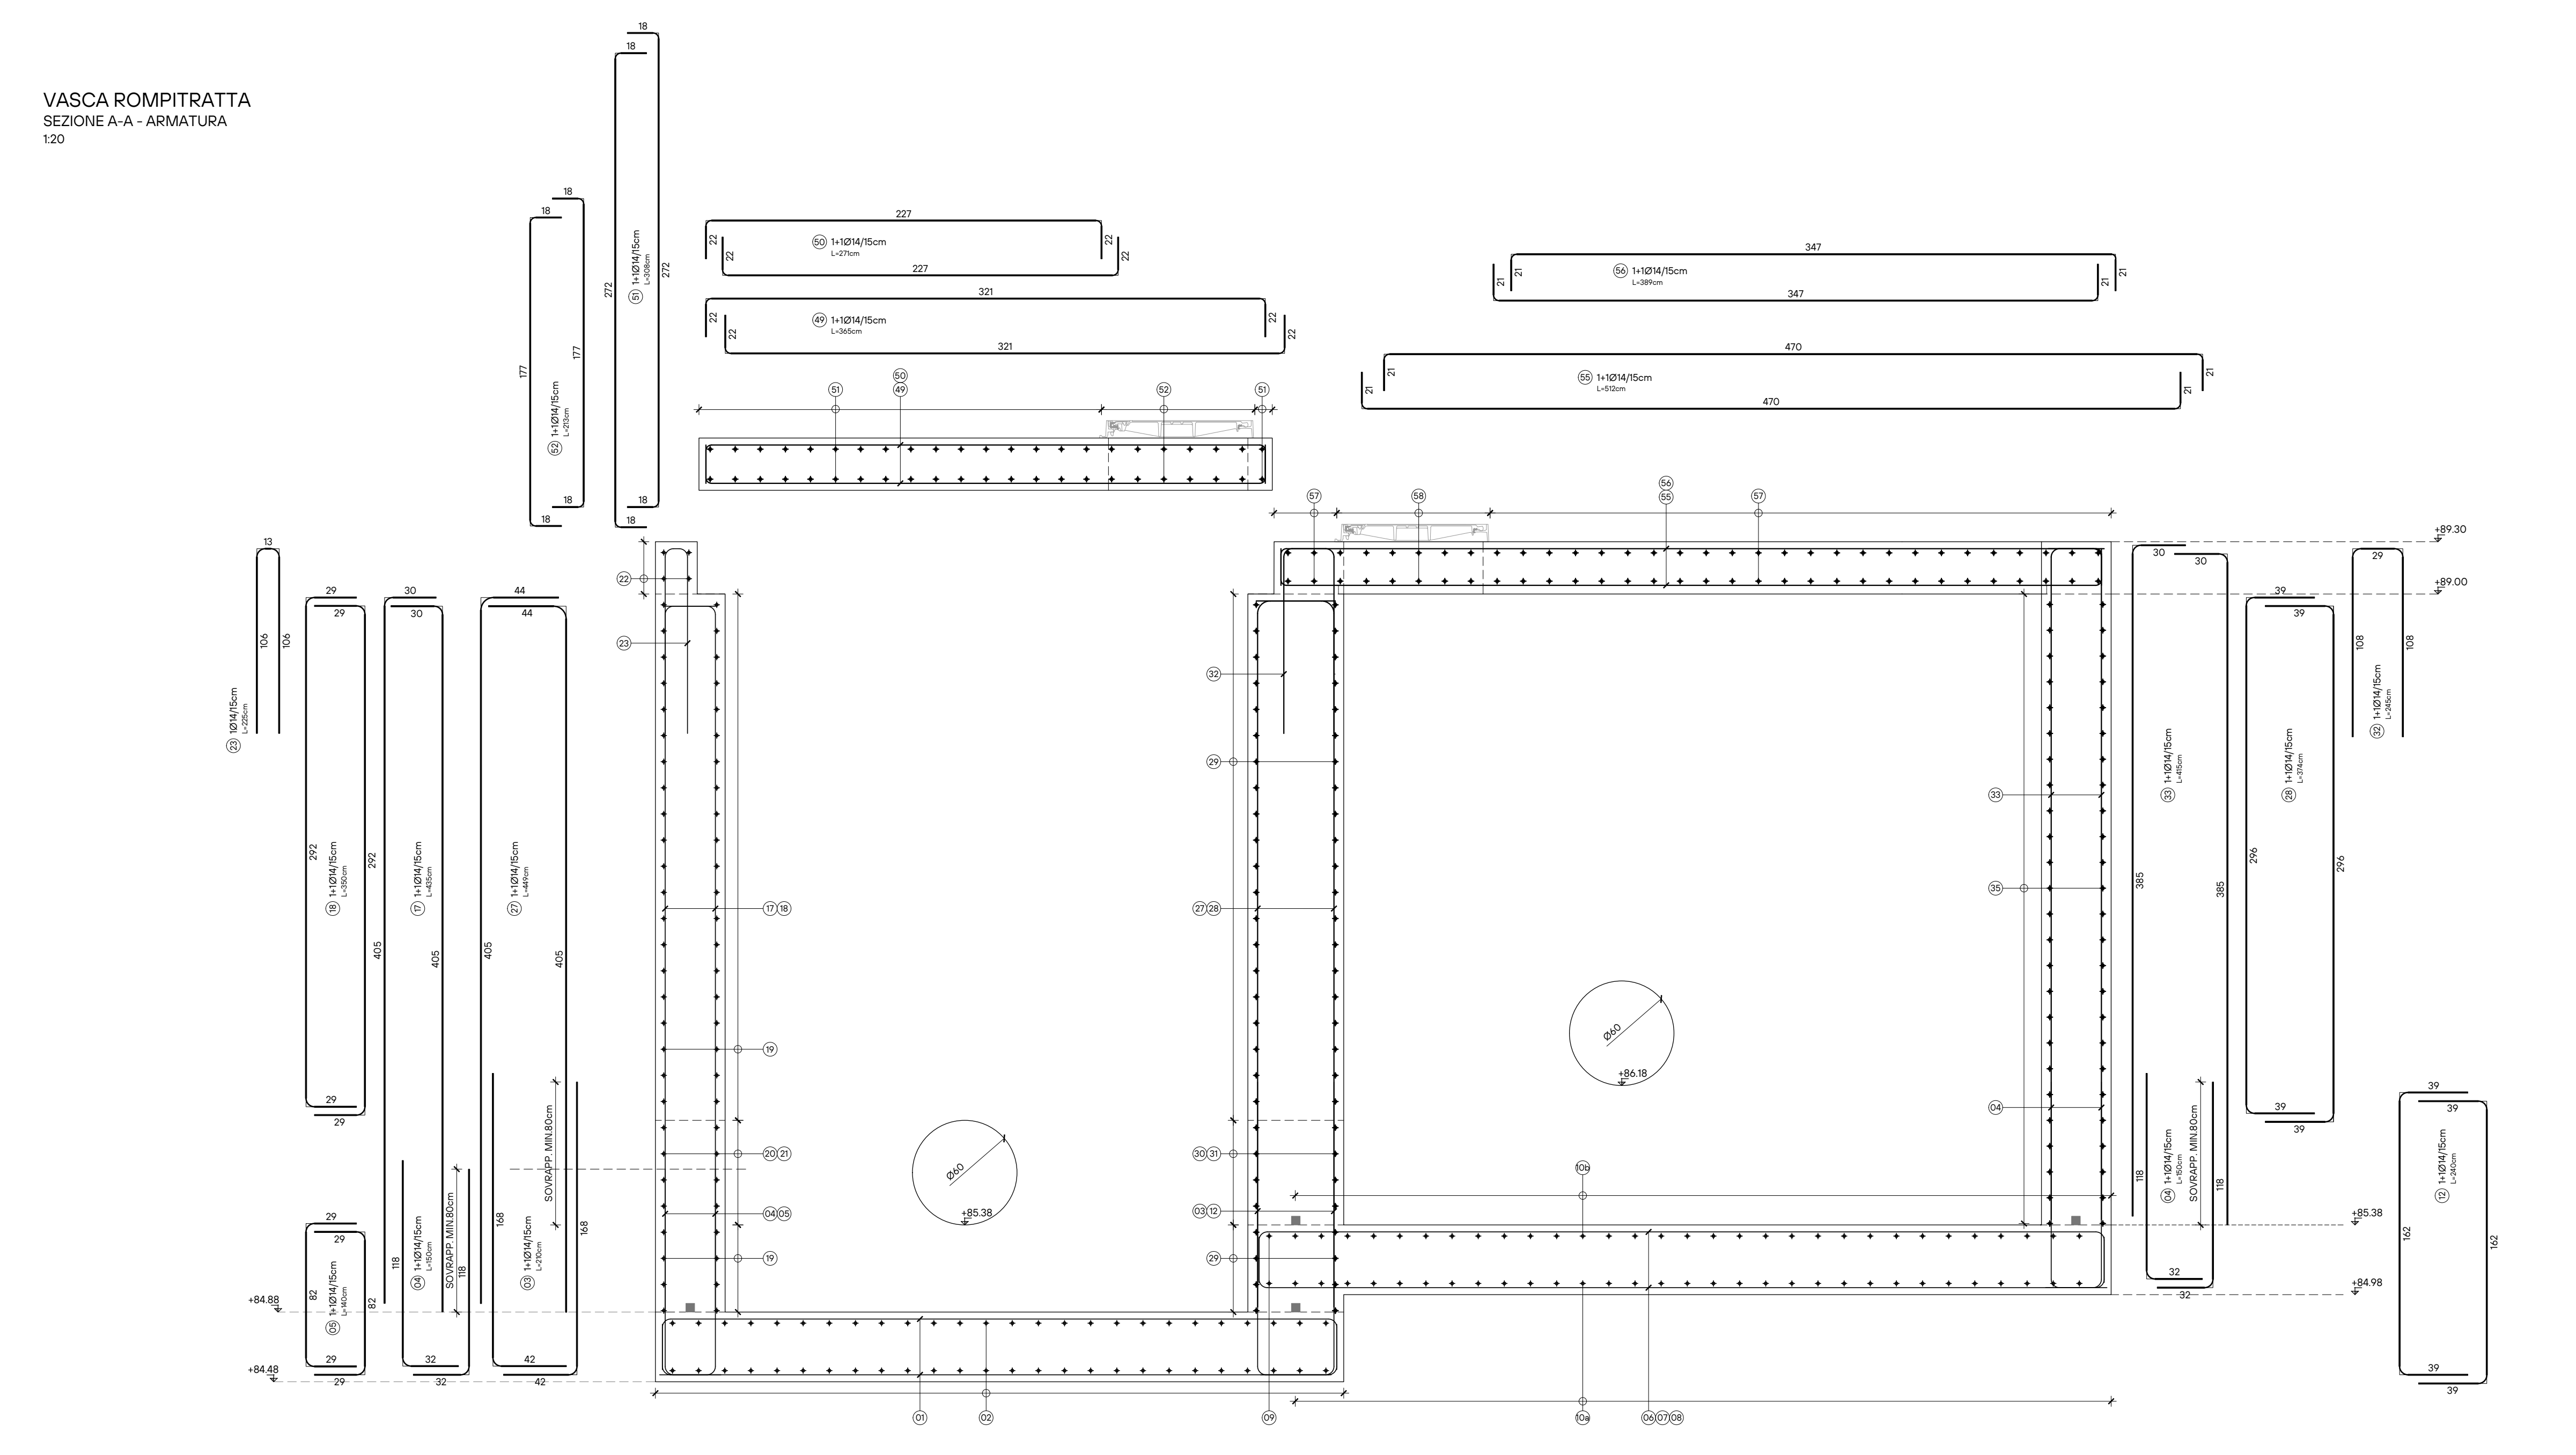

VASCA ROMPITRATTA
SEZIONE B-B - ARMATURA
1:20

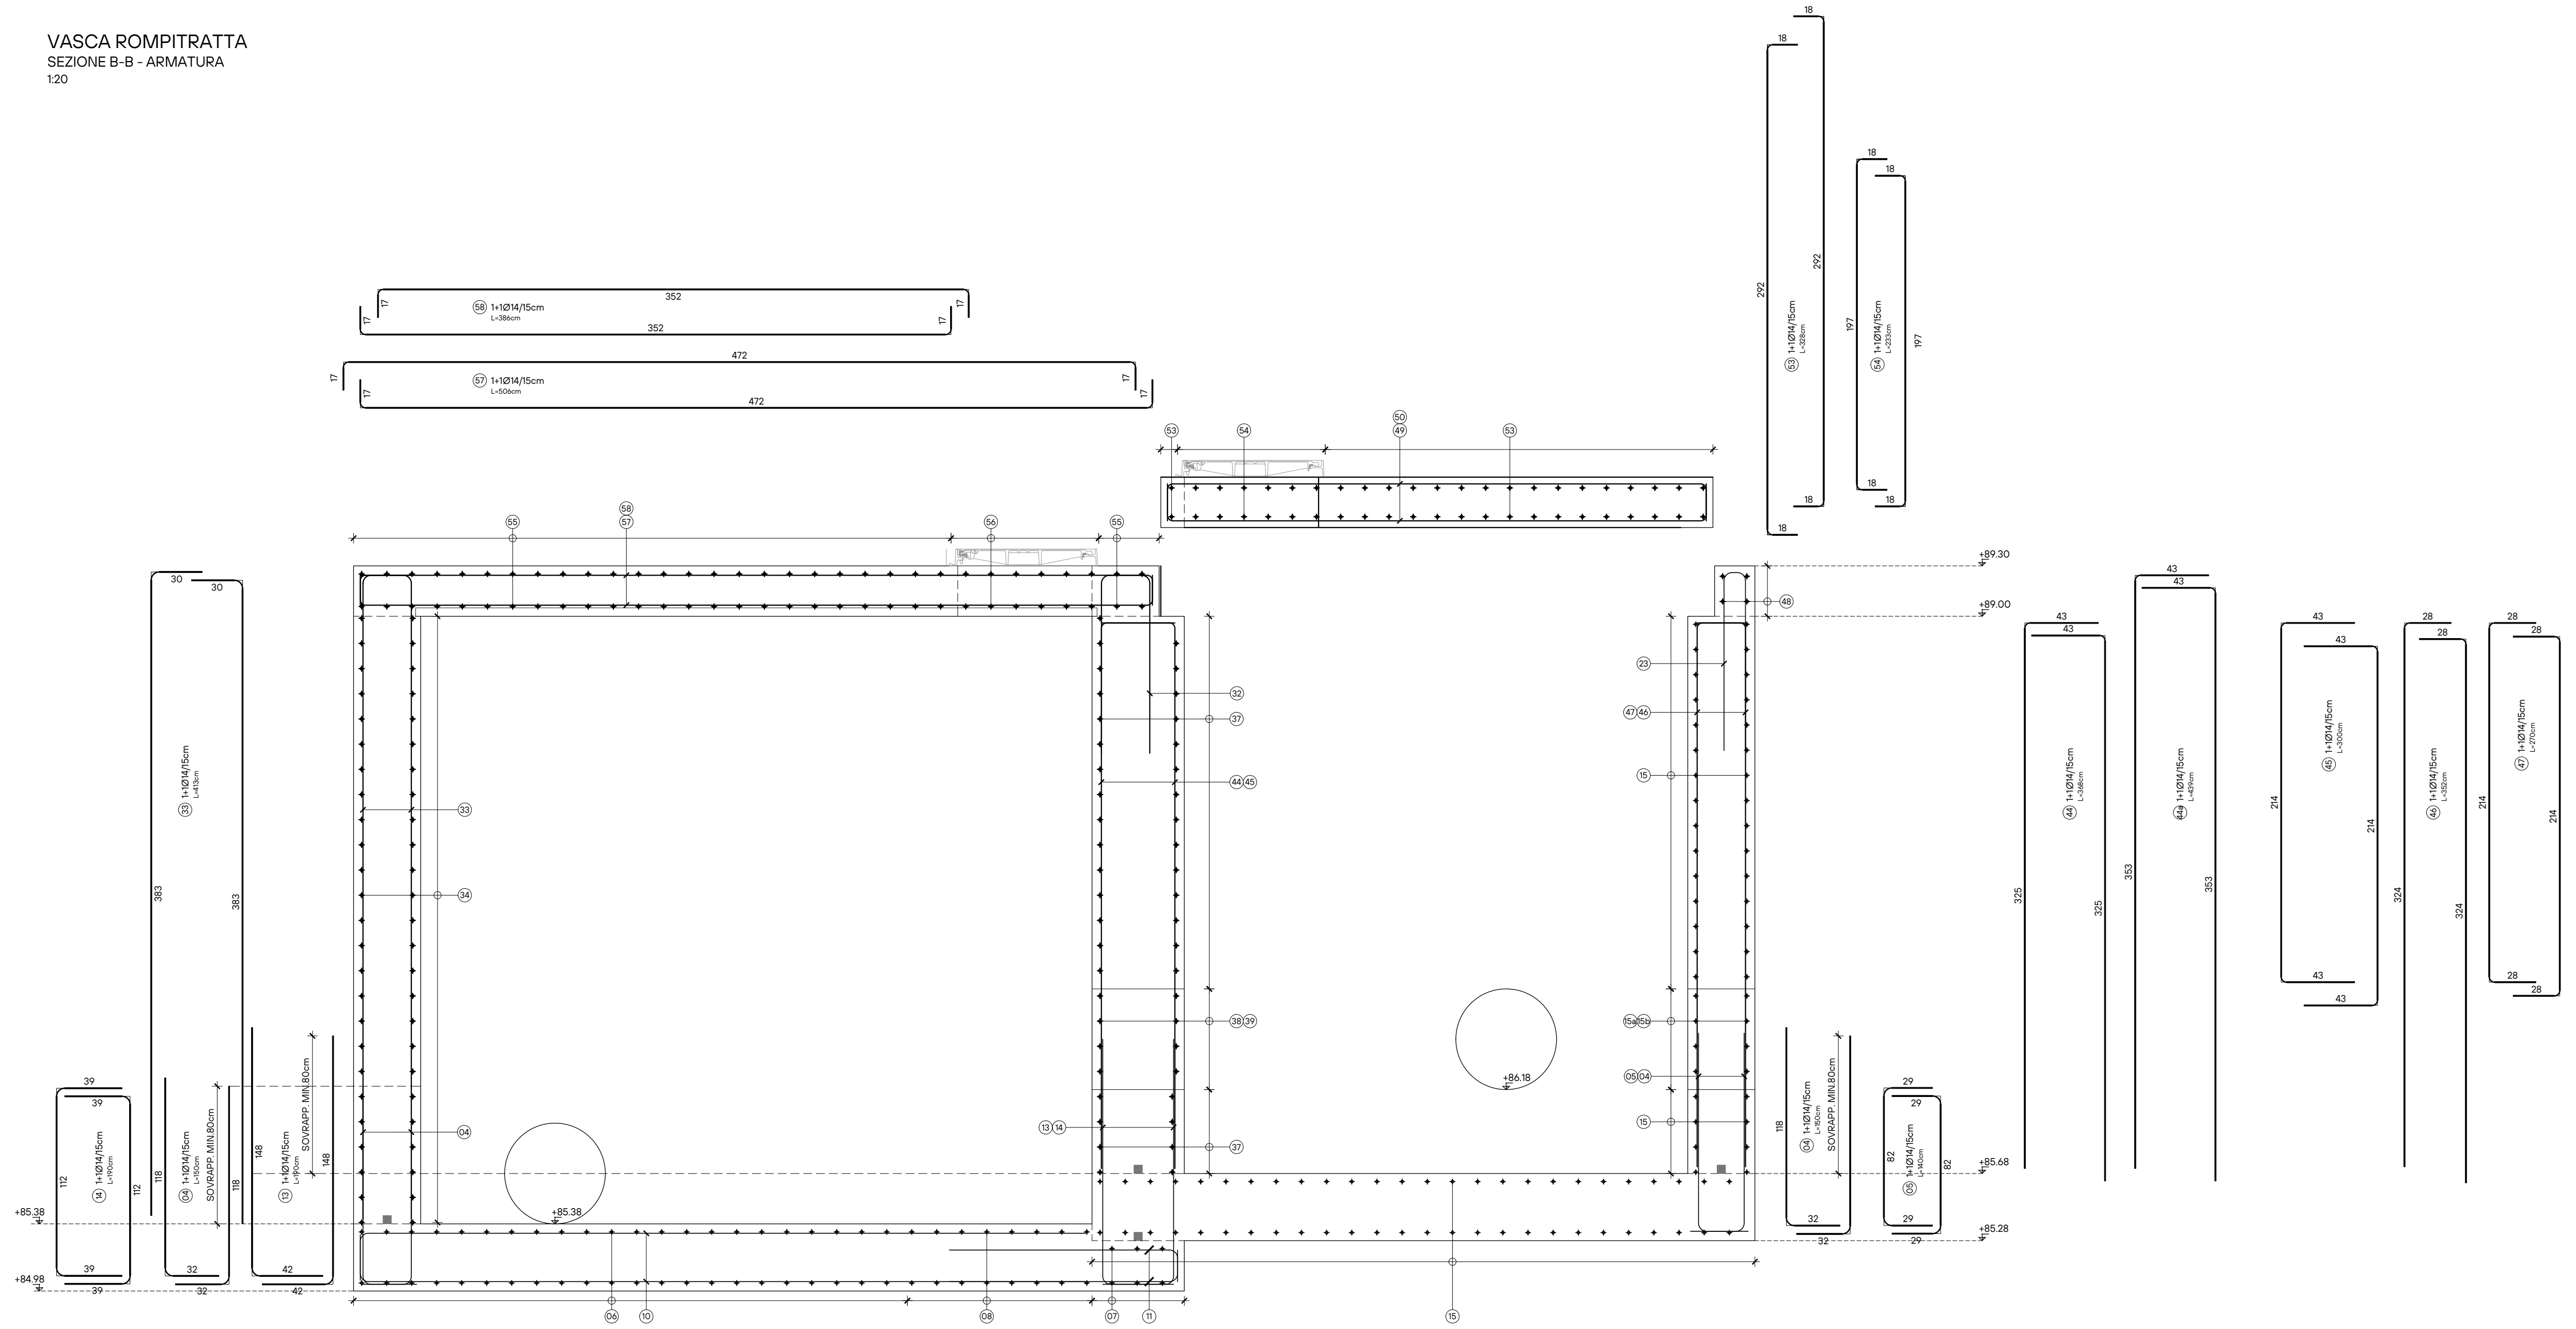

DETTAGLIO FORO CIRCOLARE
ARMATURA INTEGRATIVA
SCALA 1:20

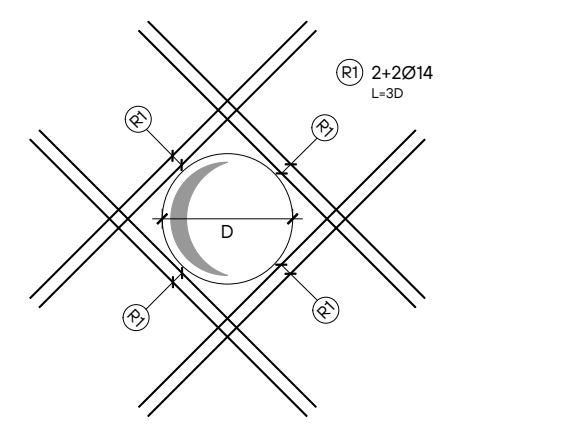

DETTAGLIO FORO RETTANGOLARE
ARMATURA INTEGRATIVA
SCALA 1:20

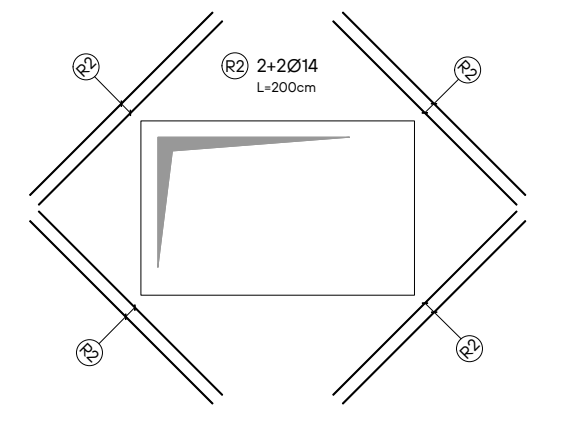

DETTAGLIO DISTANZIATORI
SOLETTA sp.40cm
SCALA 1:20

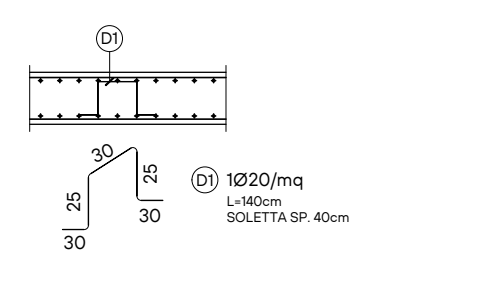

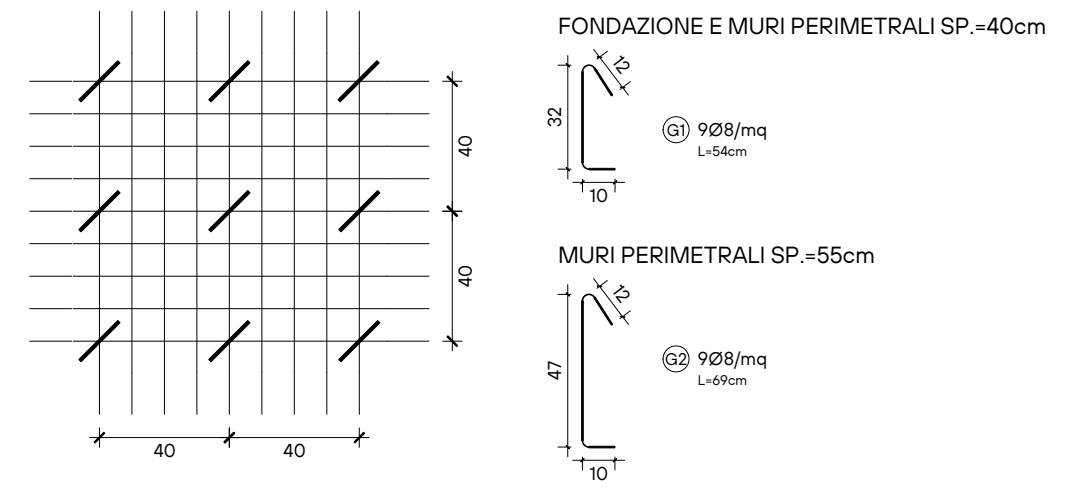

FONDAZIONE E MURI PERIMETRALI SP.=40cm

G1 9Ø8/mq
L=54cm

MURI PERIMETRALI SP.=55cm

G2 9Ø8/mq
L=69cm

NOTA:
IN CORRISPONDENZA DI EVENTUALI FORI PRESENTI:
- INTERROMPERE I FERRI DI ARMATURA BASE IN ENTRAMBE LE DIREZIONI;
- INSERIRE FORCHETTE DI CHIUSURA (POS. F1) E FERRI DI RINFORZO (cfr. DETTAGLI FORO CIRCOLARE E RETTANGOLARE)

F1 1Ø14/15cm
L=192cm

F2 1Ø14/15cm
L=204cm

TABELLA MATERIALI

ACCIAIO

ACCIAIO PER C.A.
Rif. DM 17/01/2018

TIPO B450C saldabile:

- Resistenza caratteristica a snervamento:	fyk > 450 MPa
- Resistenza caratteristica a rottura:	ftk > 540 MPa

- Collegamento di barre d'armatura post-installate (inghisaggio): Impiegare ancorante chimico epossidico ad alte prestazioni tipo Hilti HIT-RE 500 v4 o equivalente secondo indicazioni del fornitore

CALCESTRUZZO

CALCESTRUZZO MAGRO
E GETTI DI LIVELLAMENTO

- CLASSE DI RESISTENZA MINIMA:	C12/15
- CLASSE DI ESPOSIZIONE AMBIENTALE:	X0

CALCESTRUZZO PER OPERE DEFINITIVE
Rif. UNI EN 206

- CLASSE DI CONSISTENZA:	S5
- CLASSE DI ESPOSIZIONE AMBIENTALE:	XC4+XA2
- RAPPORTO MASSIMO a/c:	0.5
- CONTENUTO DI CLORURI:	Cl<0.4
- DIAMETRO MASSIMO DEGLI INERTI:	D_{max}=25mm
- CEMENTO RESISTENTE AI SOLFATI	
- CLASSE DI RESISTENZA MINIMA:	C32/40
- COPRIFERRO NOMINALE:	40 mm

AZIENDA GARDESANA SERVIZI

"INTERVENTI DI RIQUALIFICAZIONE DEL SISTEMA DI RACCOLTA DEI REFLUI NEL BACINO DEL LAGO DI GARDA - SPONDA VERONESE"
Lotto 1 - Tratto 4 - 2°Stralcio
"OPERE COLLETTORE IN PRESSIONE ED OPERE COMPLEMENTARI TRATTO PERGOLANA - ROCCA VELA - COMUNE BARDOLINO"
Lotto 8 - Tratto 4_OC
CIG: B7E3B750B2 - CUP: J33F17000010002

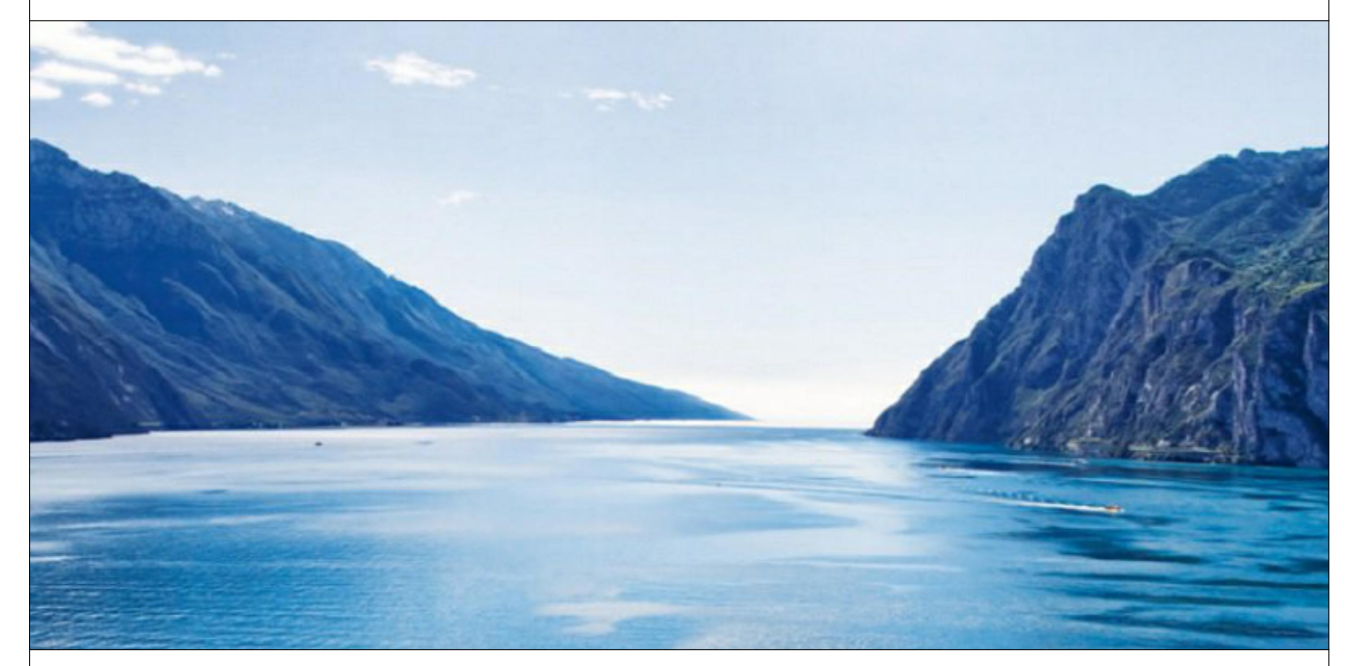

PROGETTO ESECUTIVO

PROGETTISTA E COORDINATORE SICUREZZA IN FASE DI PROGETTO:
Ing. Giovanni Battista Matteotti

COLLABORAZIONE:
Ing. Luca Petracin
Ing. Andrea Martinello
Ing. Emanuele Anderlini
Ing. Filiberto Boscolo Lisetto
Geom. Elisa Zatti

mass
INGEGNERIA E ARCHITETTURA SRL
Via Sorio 33/a, 35141 PADOVA
Tel: 049-723320 - Mail: Info@matteotti.com

ING. G.B. MATTEOTTI

RESPONSABILE UNICO DEL PROGETTO:
Dott. Ing. Carlo Alberto Voi

TITOLO	*SCALA*	*CODICE ELABORATO*
VASCA ROMPITRATTA - Opere Strutturali - Armature e dettagli	VARIE	C-14-001

N° REV	*DATA*	*DESCRIZIONE*	*ESEGUITO*	*VERIFICATO*	*APPROVATO*
00	Marzo 2026	PRIMA EMISSIONE		Ing. L. Petracin	Ing. G. B. Matteotti
01	Aprile 2026	AGGIORNAMENTO A SEGUITO DI VERIFICA		Ing. L. Petracin	Ing. G. B. Matteotti
02					
03					
04					