PARETE FILO A - ARMATURA ORIZZONTALE
SCALA 1:50

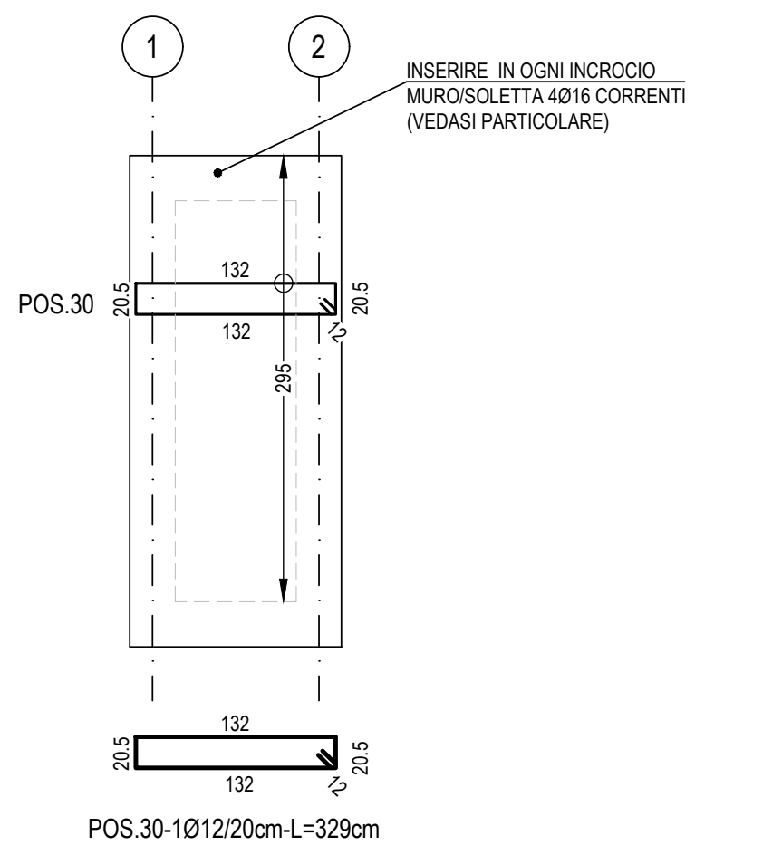
INSERIRE IN OGNI INCROCIO MURO/SOLETTA 4Ø16 CORRENTI (VEDASI PARTICOLARE)
POS.30
POS.30-1Ø12/20cm-L=329cm

PARETE FILO A - ARMATURA VERTICALE
SCALA 1:50

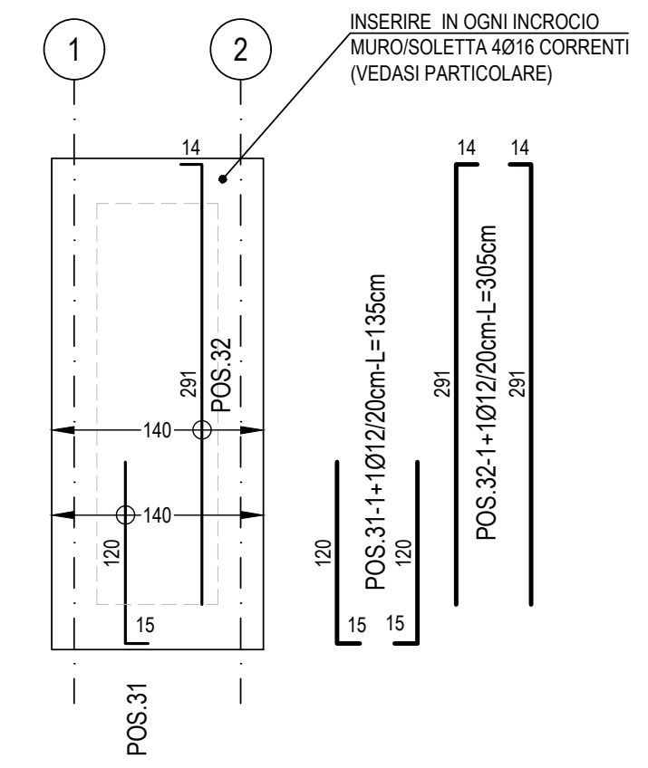
INSERIRE IN OGNI INCROCIO MURO/SOLETTA 4Ø16 CORRENTI (VEDASI PARTICOLARE)
POS.31
POS.32

PARETE FILO D - ARMATURA ORIZZONTALE
SCALA 1:50

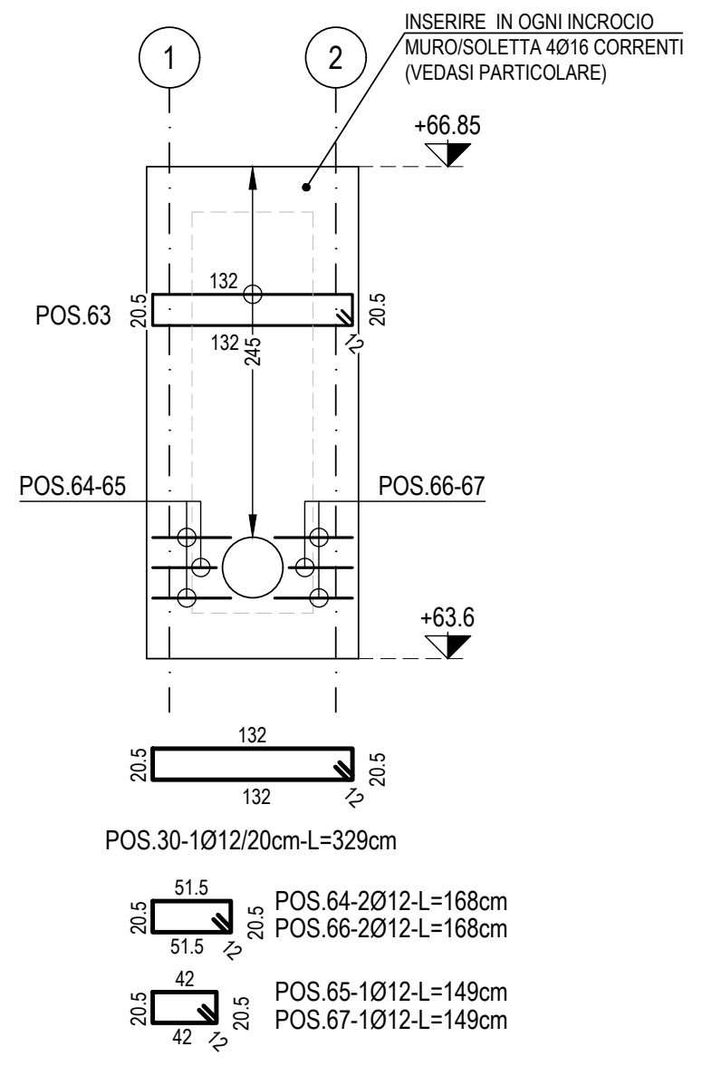

PARETE FILO D - ARMATURA VERTICALE
SCALA 1:50

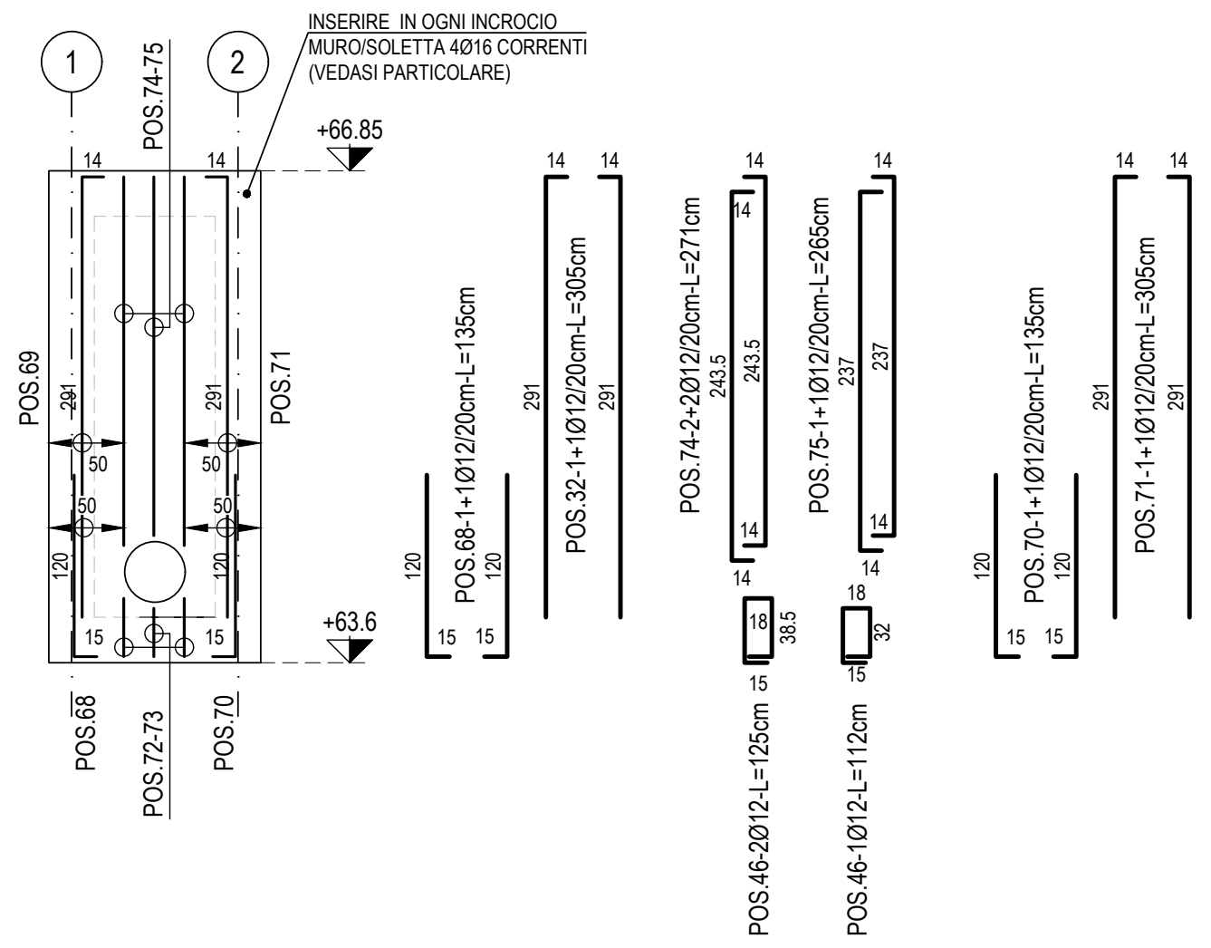
INSERIRE IN OGNI INCROCIO MURO/SOLETTA 4Ø16 CORRENTI (VEDASI PARTICOLARE)
+66.85
+63.6
POS.68
POS.69
POS.70
POS.71
POS.72-73
POS.74-75

PARETE FILO 2 - ARMATURA ORIZZONTALE
SCALA 1:50

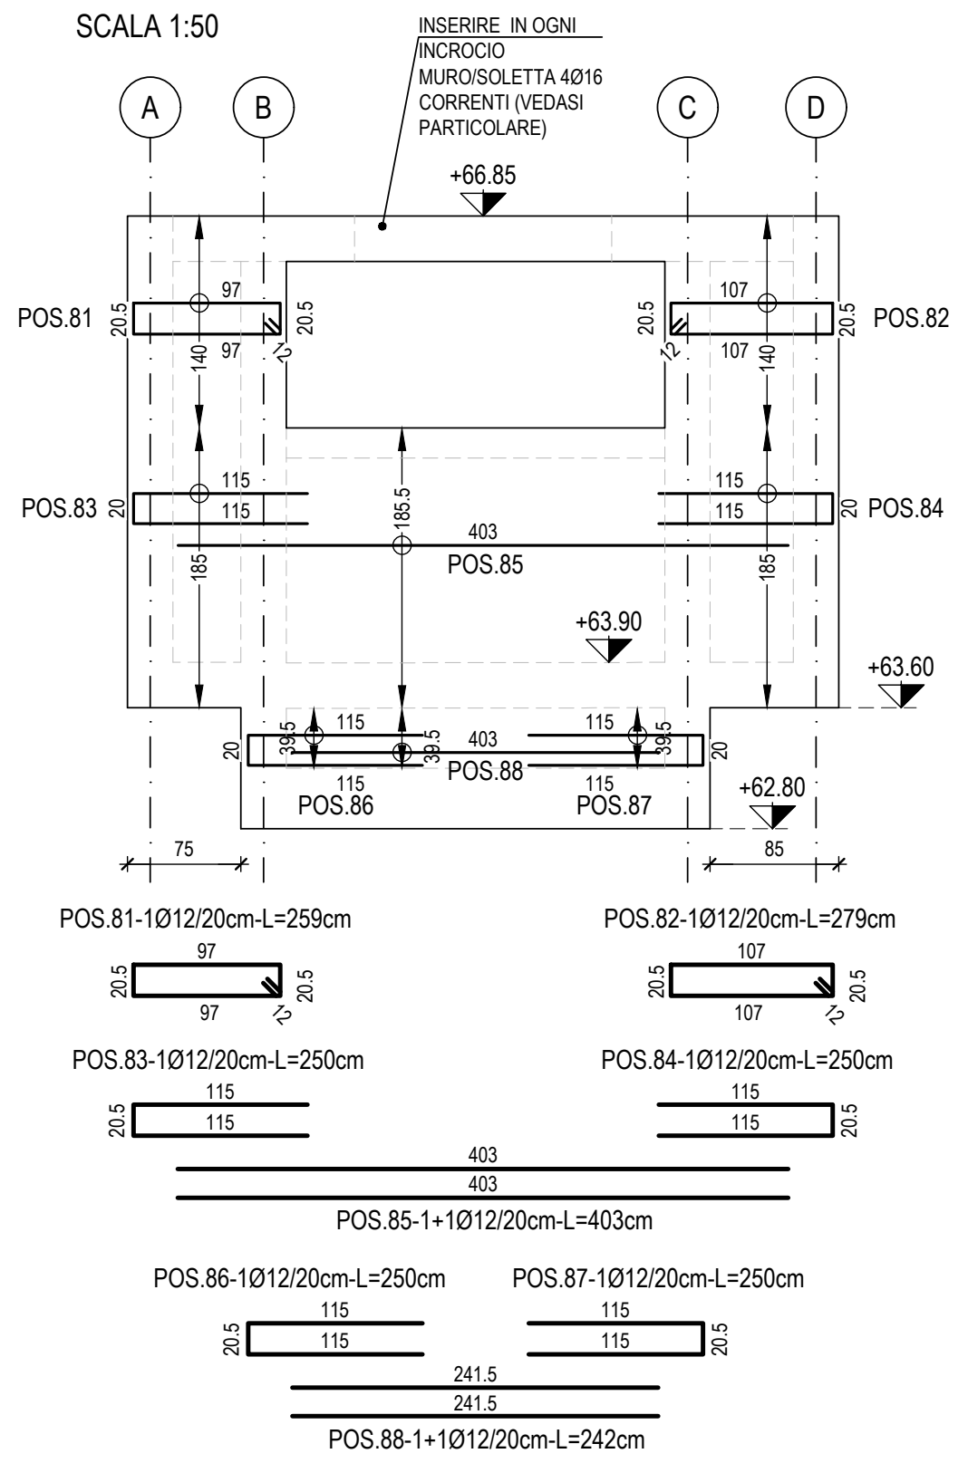

PARETE FILO 2 - ARMATURA VERTICALE
SCALA 1:50

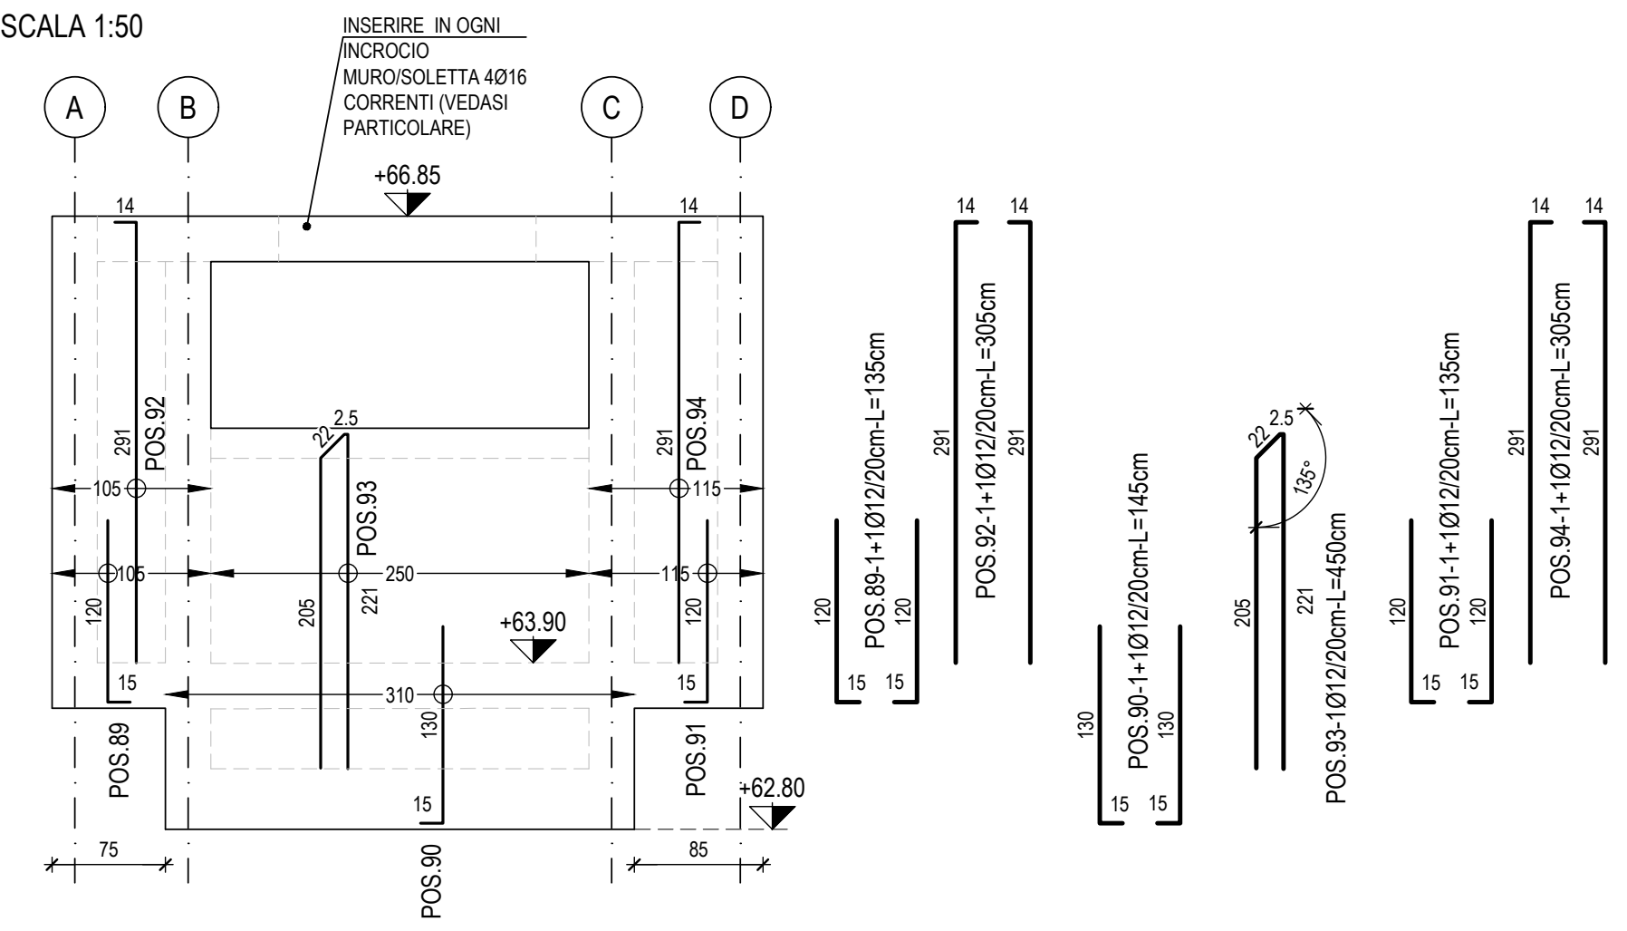
INSERIRE IN OGNI INCROCIO MURO/SOLETTA 4Ø16 CORRENTI (VEDASI PARTICOLARE)
+66.85
+63.90
+62.80
POS.89
POS.90
POS.91
POS.92
POS.93
POS.94

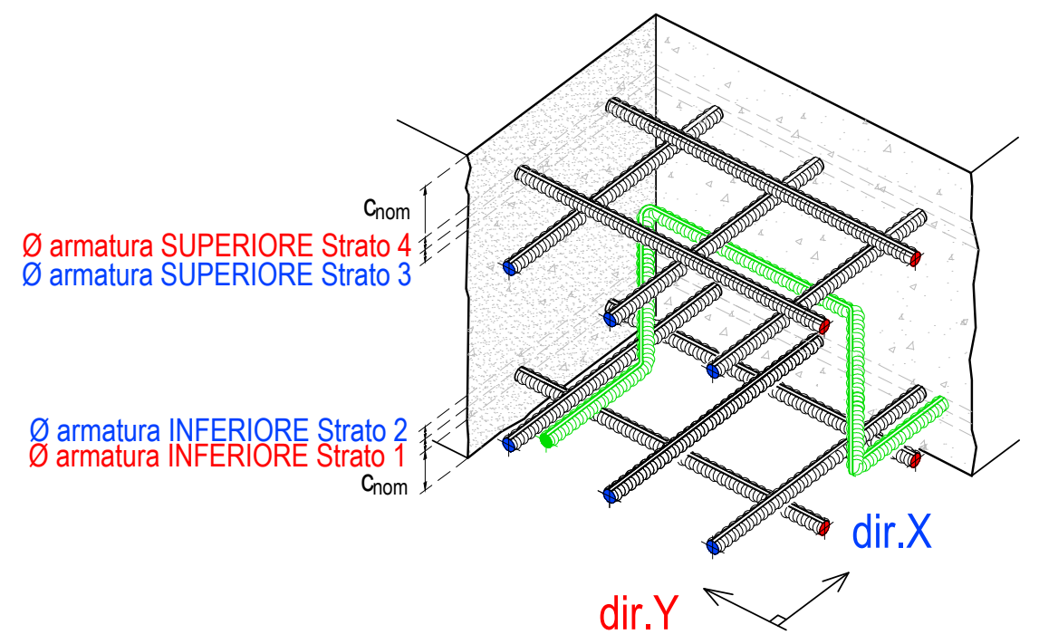
Cnom
Ø armatura SUPERIORE Strato 4
Ø armatura SUPERIORE Strato 3
Ø armatura INFERIORE Strato 2
Ø armatura INFERIORE Strato 1
Cnom
dir.X
dir.Y

PARTICOLARE
DISPOSIZIONE ARMO PARETI sp. 30cm
PIANTA SCALA 1:25

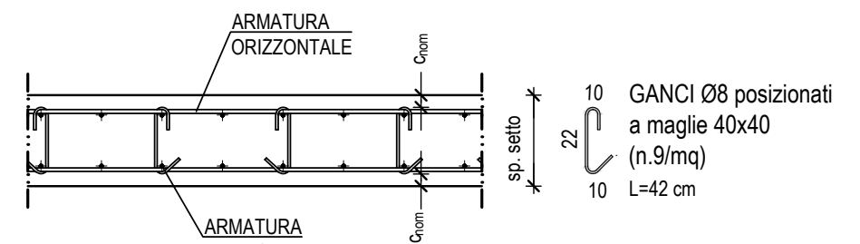

copriferro misurato sul gancio 4 cm

ARMATURA orizz. Ø12/20, vert. Ø12/20 (su entrambe le facce)

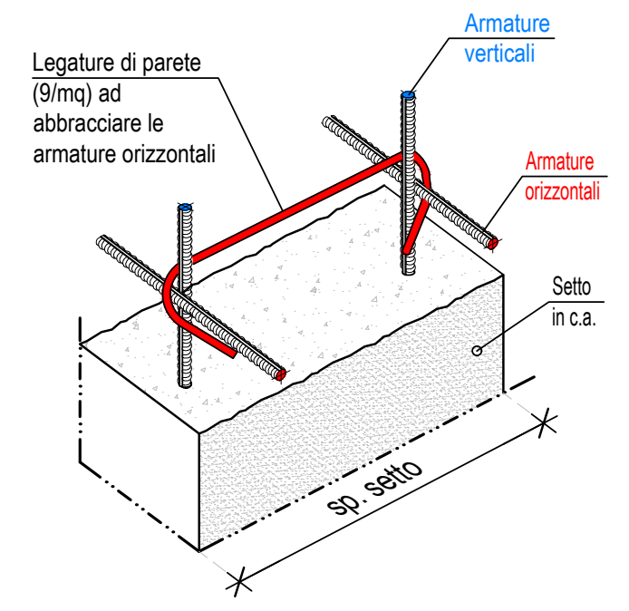
Legature di parete (9/mq) ad abbracciare le armature orizzontali
Armature verticali
Armature orizzontali
Setto in c.a.
sp. setto

PARETE FILO B - ARMATURA ORIZZONTALE
SCALA 1:50

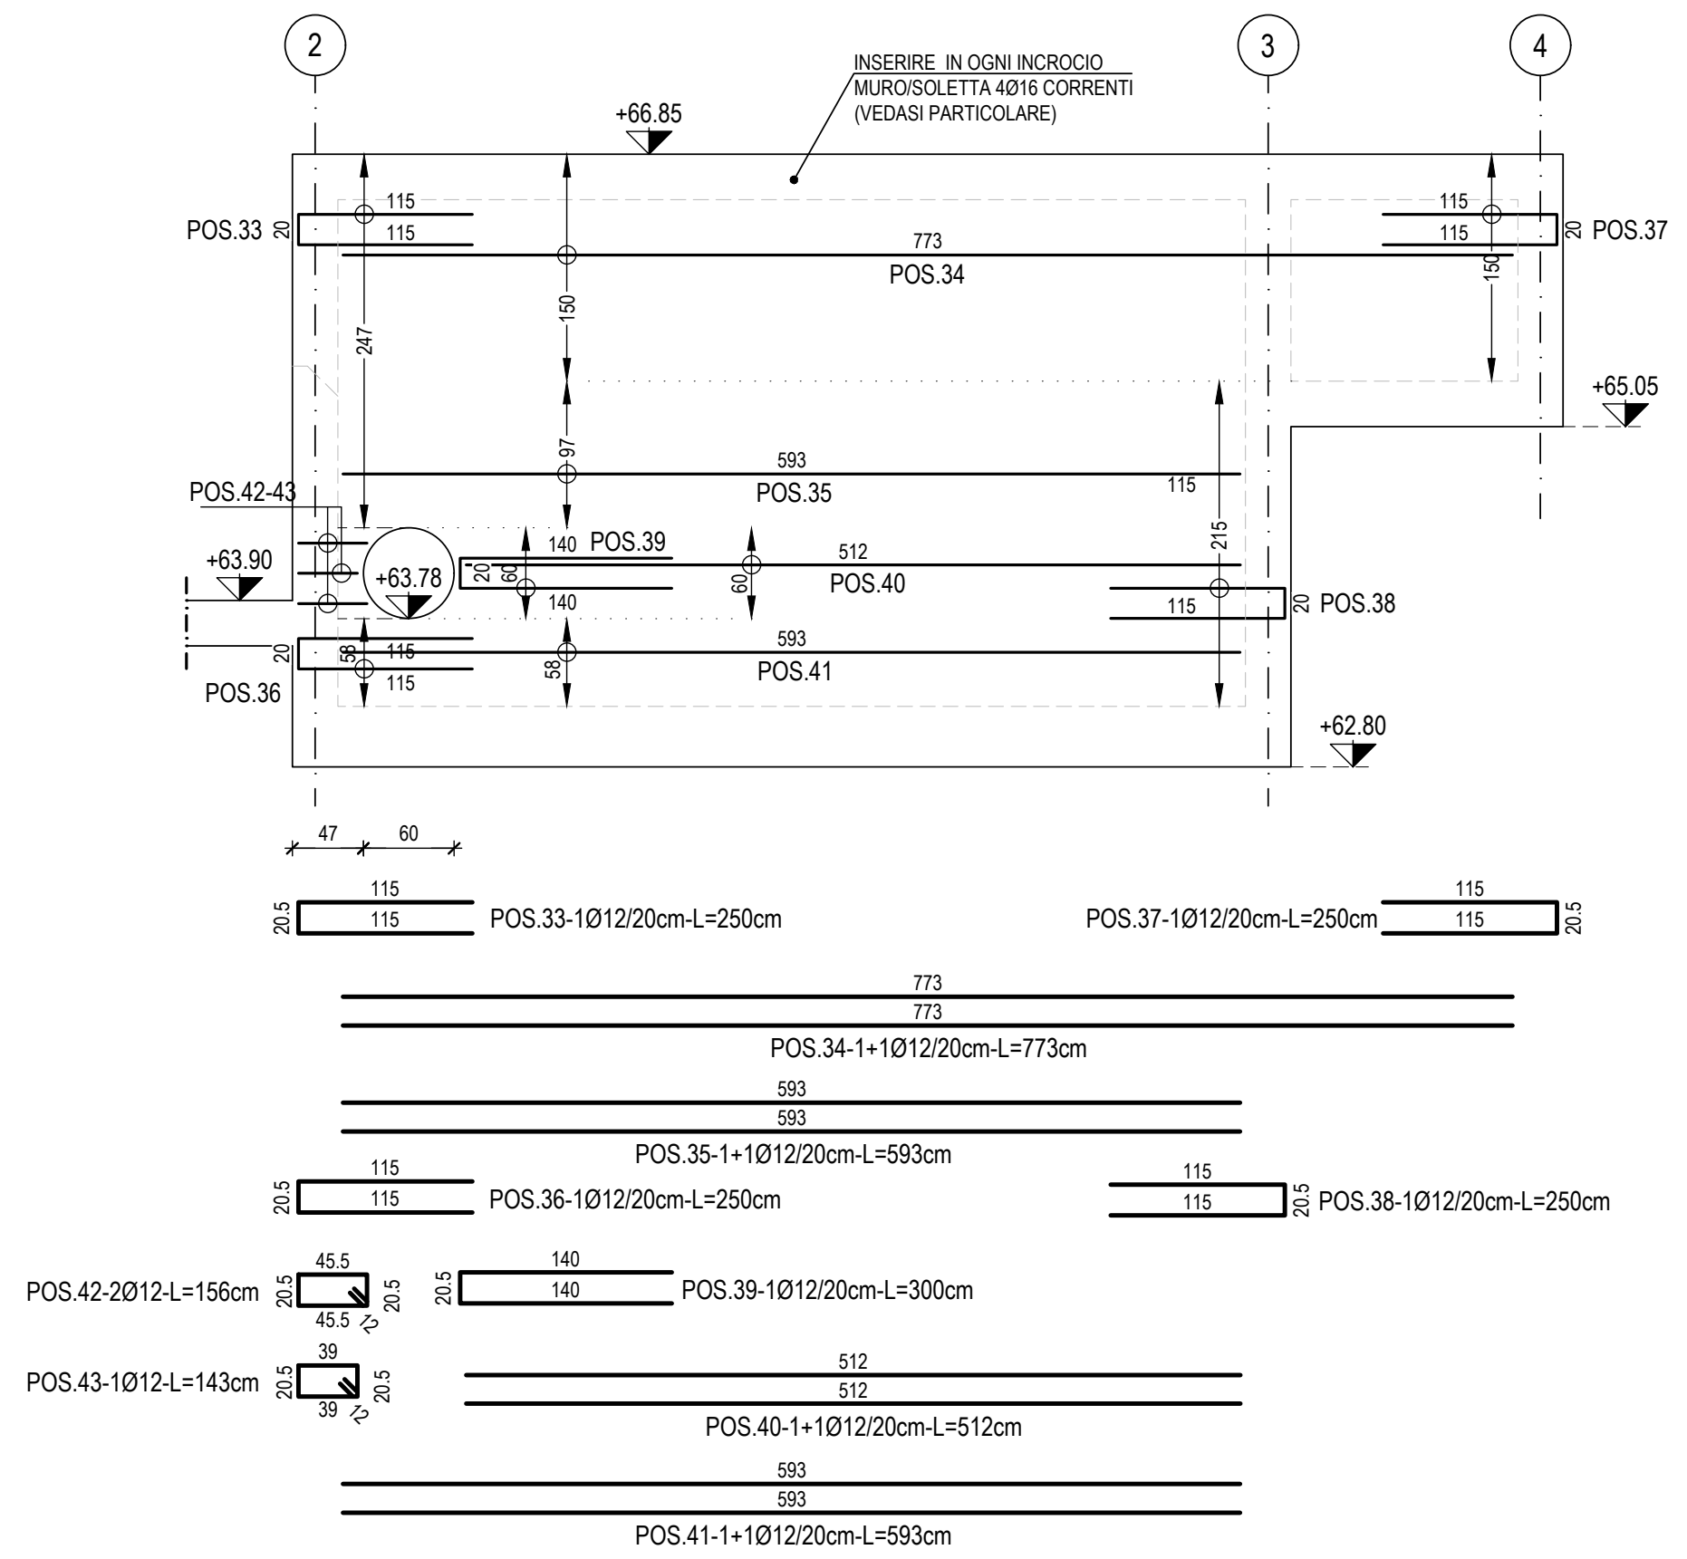

PARETE FILO B - ARMATURA VERTICALE
SCALA 1:50

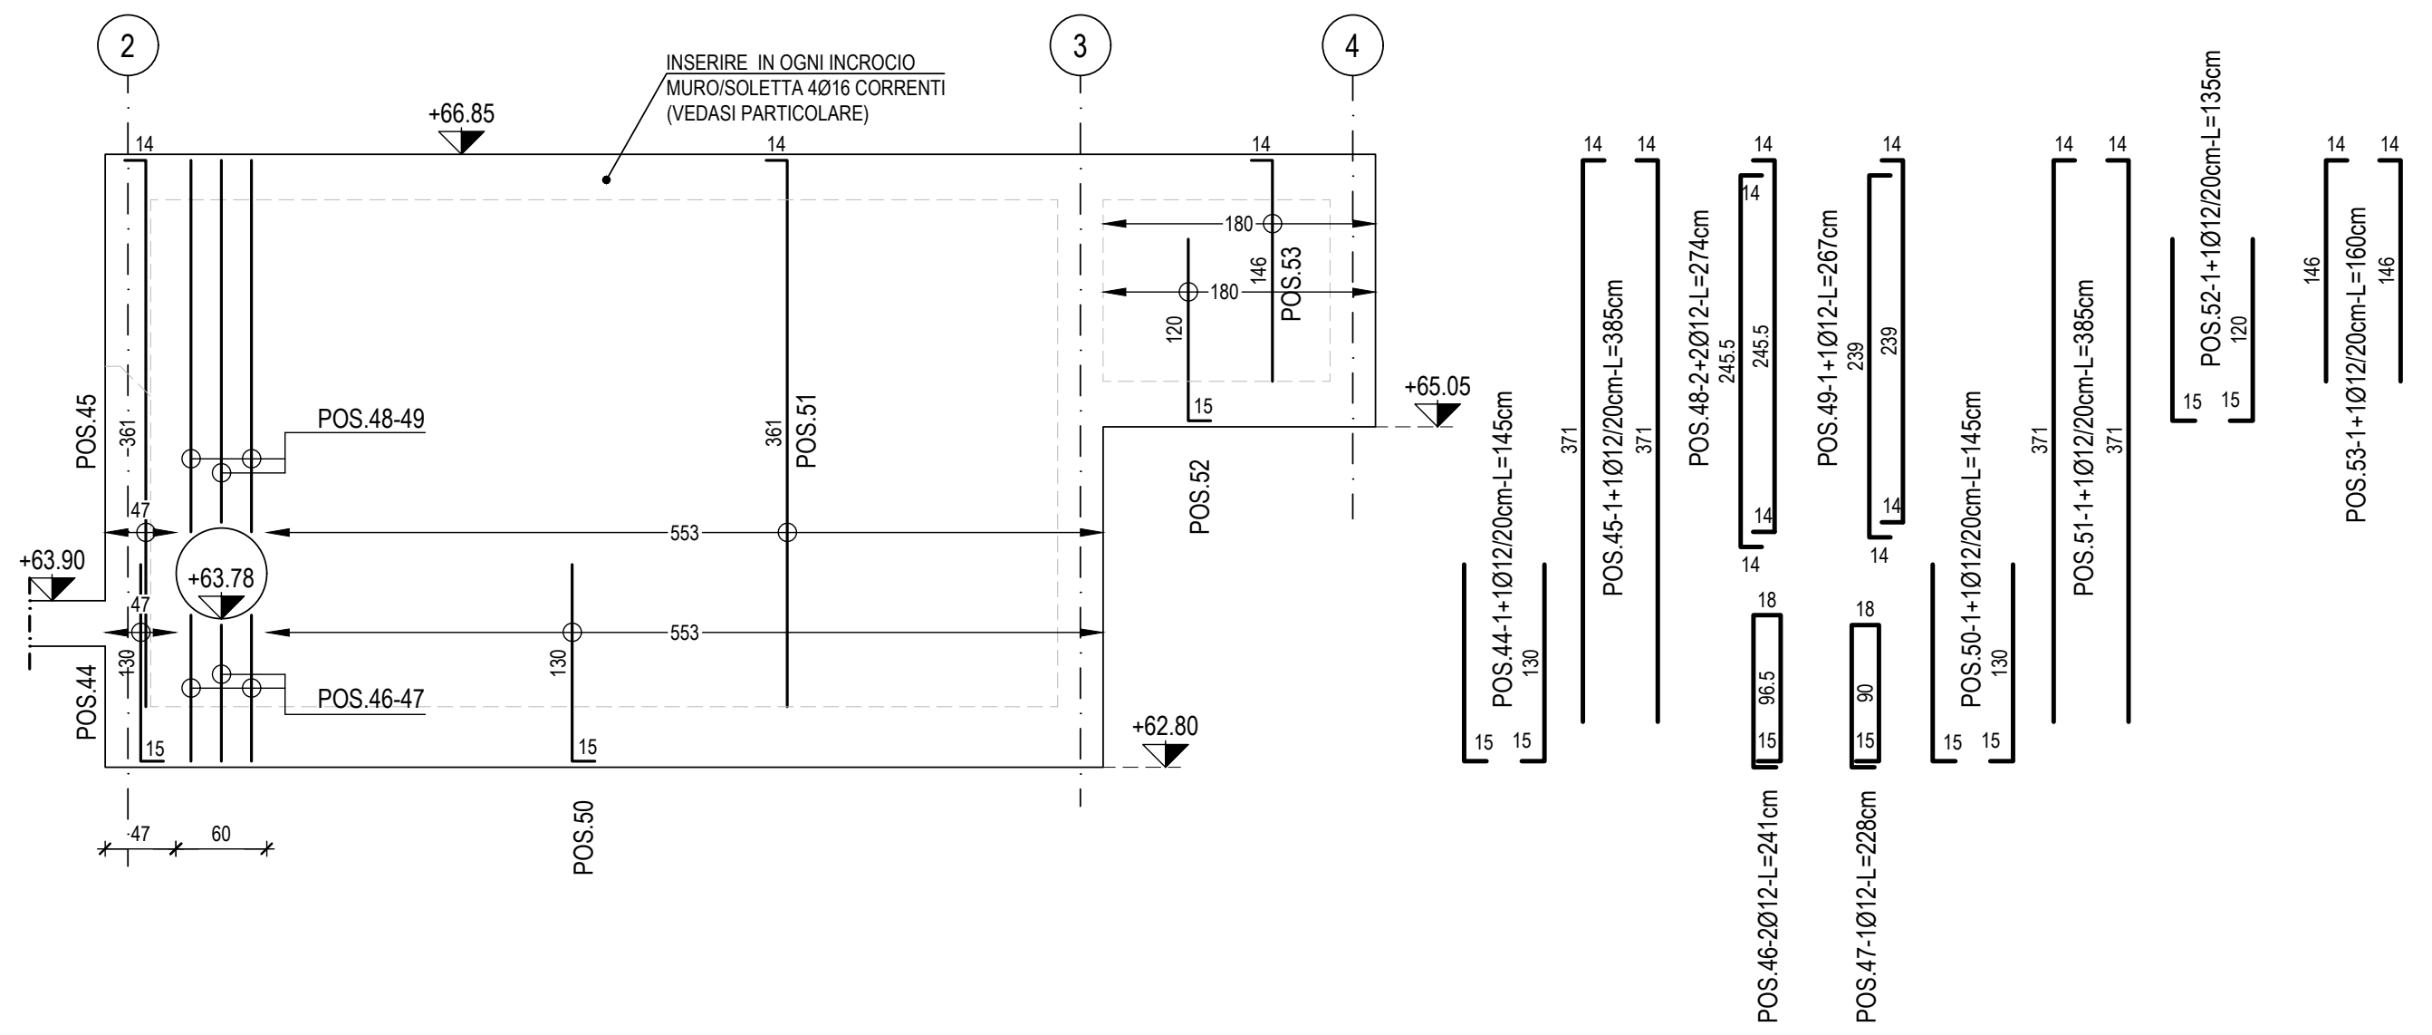

PARETE FILO 3 - ARMATURA ORIZZONTALE
SCALA 1:50

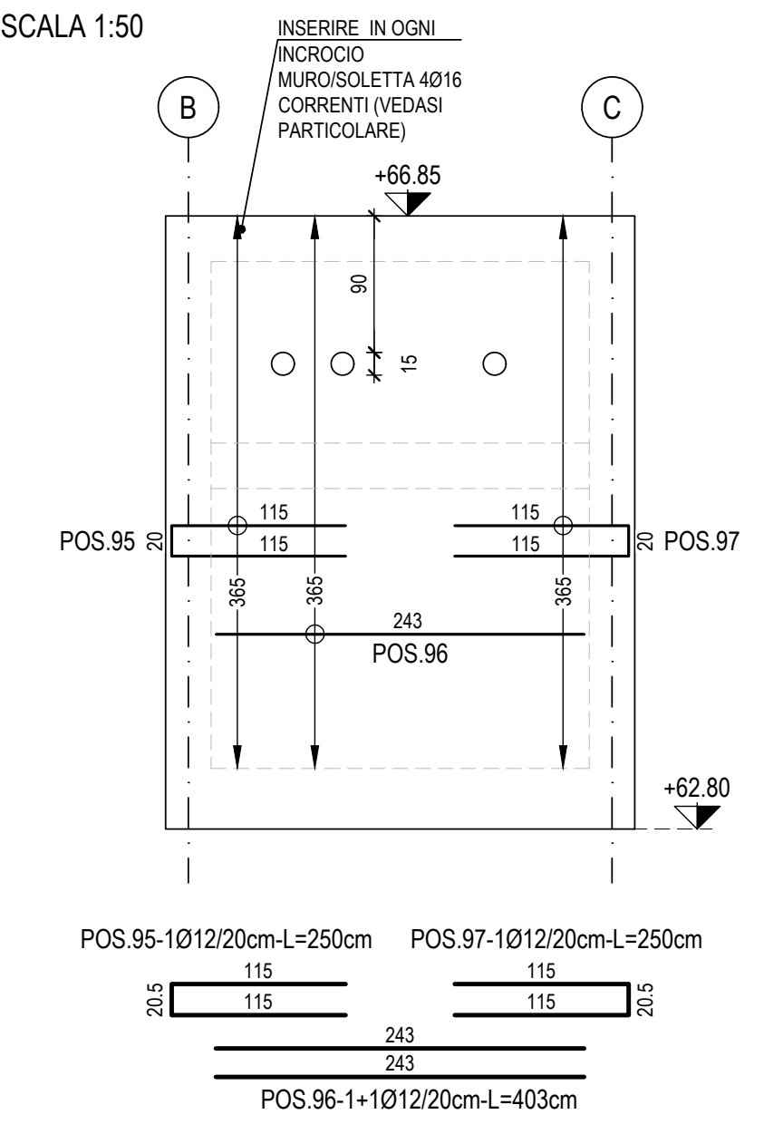
INSERIRE IN OGNI INCROCIO MURO/SOLETTA 4Ø16 CORRENTI (VEDASI PARTICOLARE)
+66.85
+62.80
POS.95
POS.96
POS.97
POS.95-1Ø12/20cm-L=250cm
POS.97-1Ø12/20cm-L=250cm
POS.96-1+1Ø12/20cm-L=403cm

PARETE FILO 3 - ARMATURA VERTICALE
SCALA 1:50

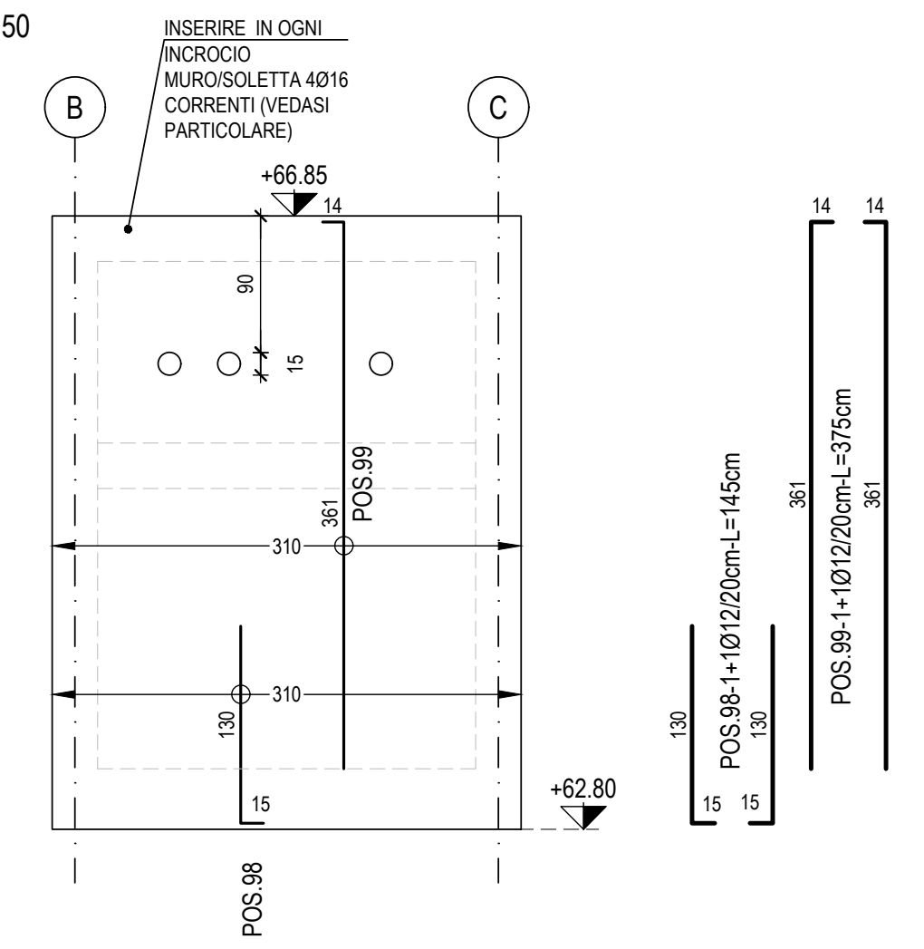
INSERIRE IN OGNI INCROCIO MURO/SOLETTA 4Ø16 CORRENTI (VEDASI PARTICOLARE)
+66.85
+62.80
POS.98
POS.99

PARETE FILO C - ARMATURA ORIZZONTALE
SCALA 1:50

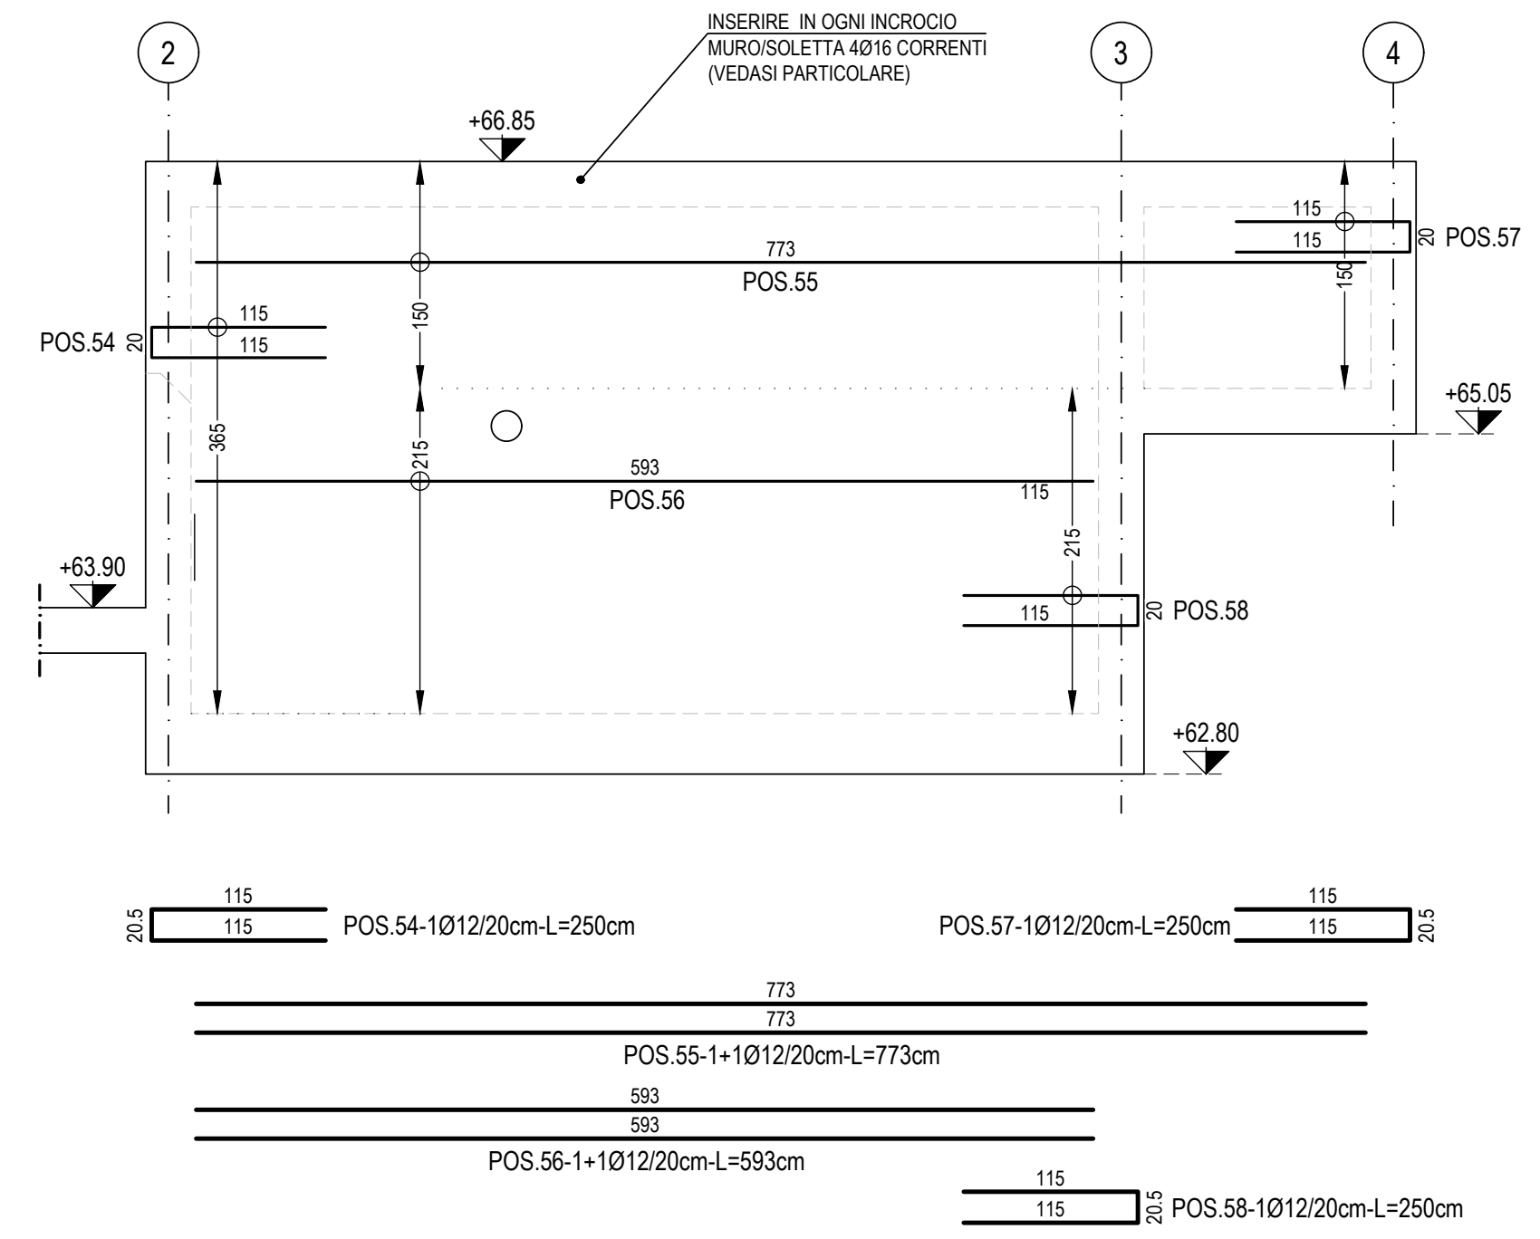

PARETE FILO C - ARMATURA VERTICALE
SCALA 1:50

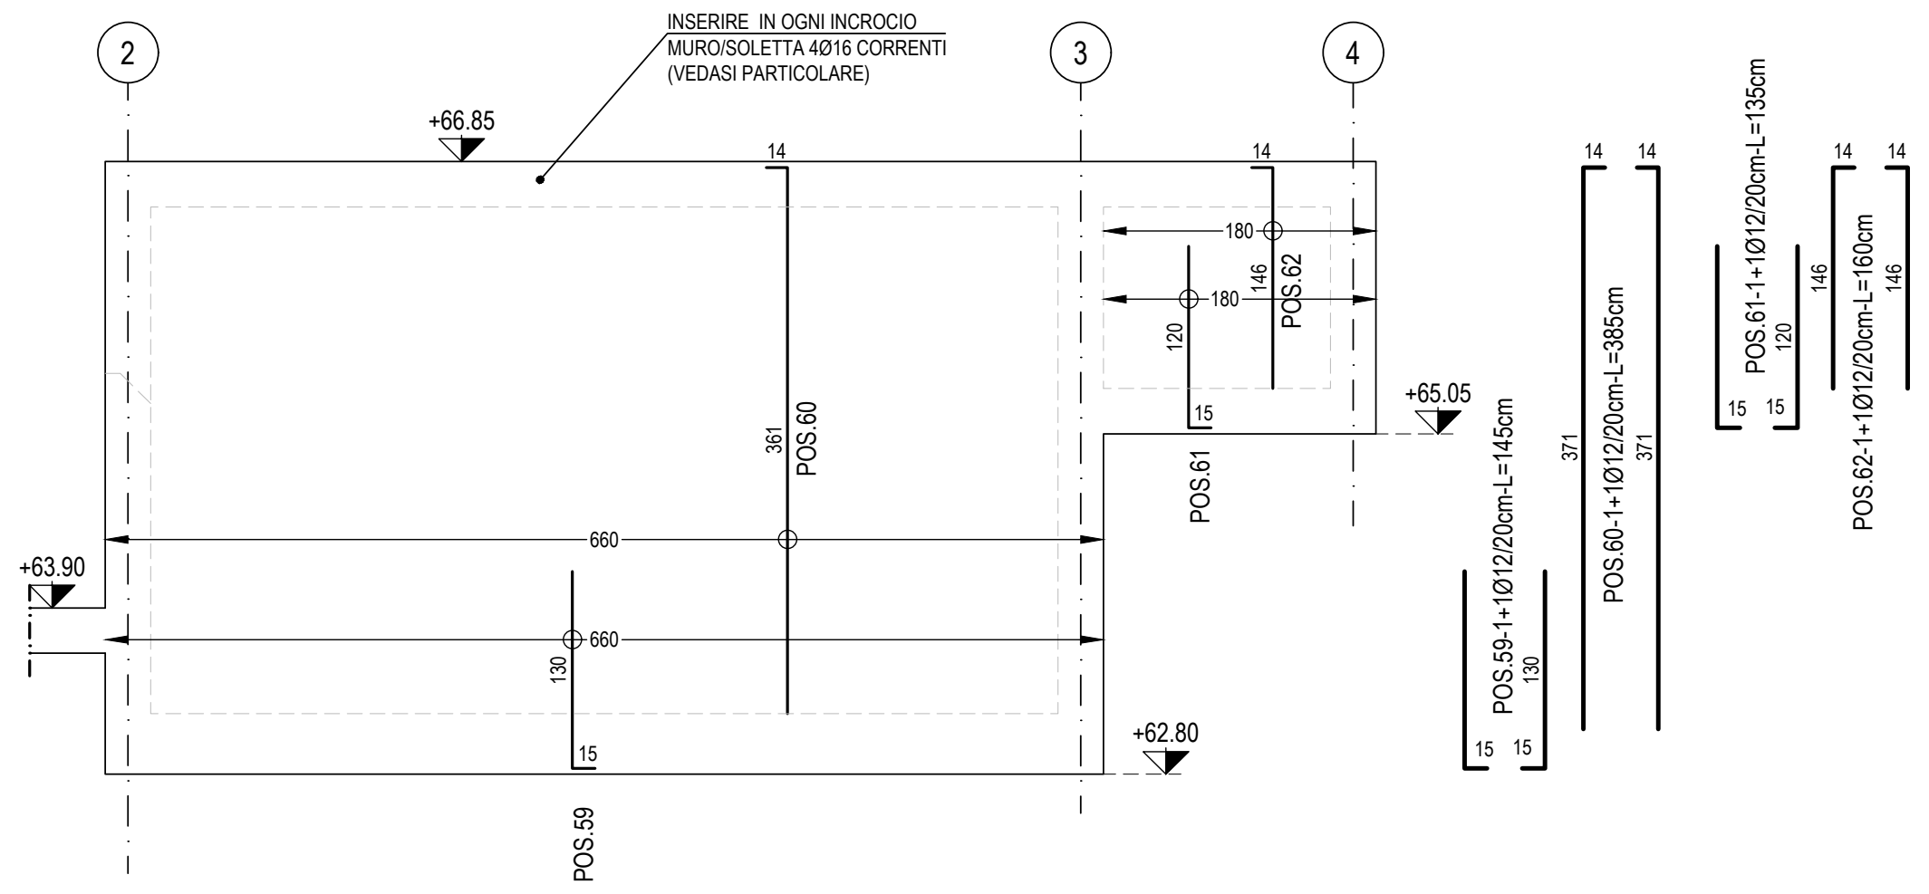
INSERIRE IN OGNI INCROCIO MURO/SOLETTA 4Ø16 CORRENTI (VEDASI PARTICOLARE)
+66.85
+65.05
+63.90
+62.80
POS.59
POS.60
POS.61
POS.62

PARETE FILO 4 - ARMATURA ORIZZONTALE
SCALA 1:50

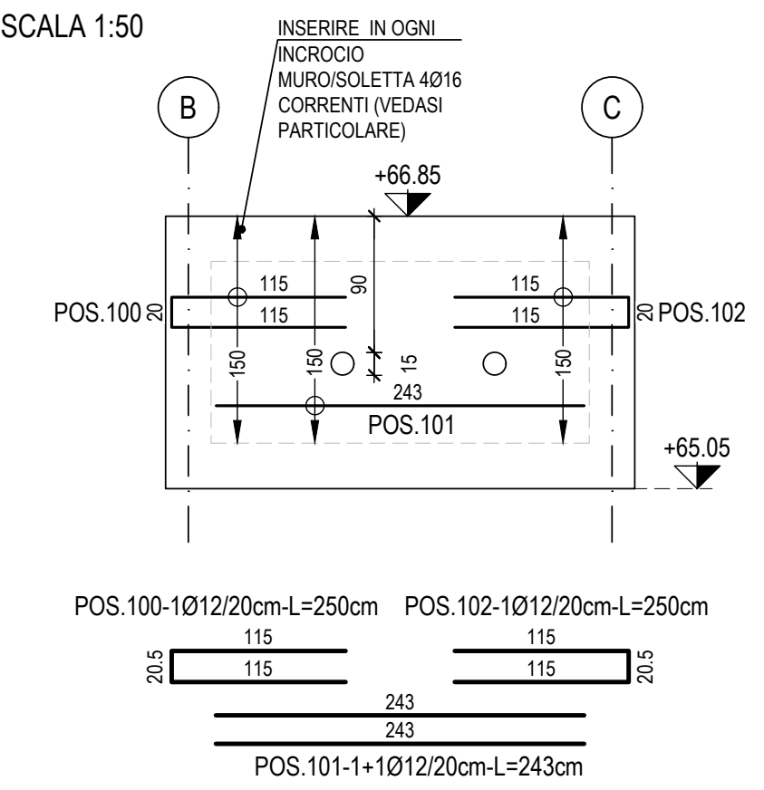
INSERIRE IN OGNI INCROCIO MURO/SOLETTA 4Ø16 CORRENTI (VEDASI PARTICOLARE)
+66.85
+65.05
POS.100
POS.101
POS.102
POS.100-1Ø12/20cm-L=250cm
POS.102-1Ø12/20cm-L=250cm
POS.101-1+1Ø12/20cm-L=243cm

PARETE FILO 4 - ARMATURA VERTICALE
SCALA 1:50

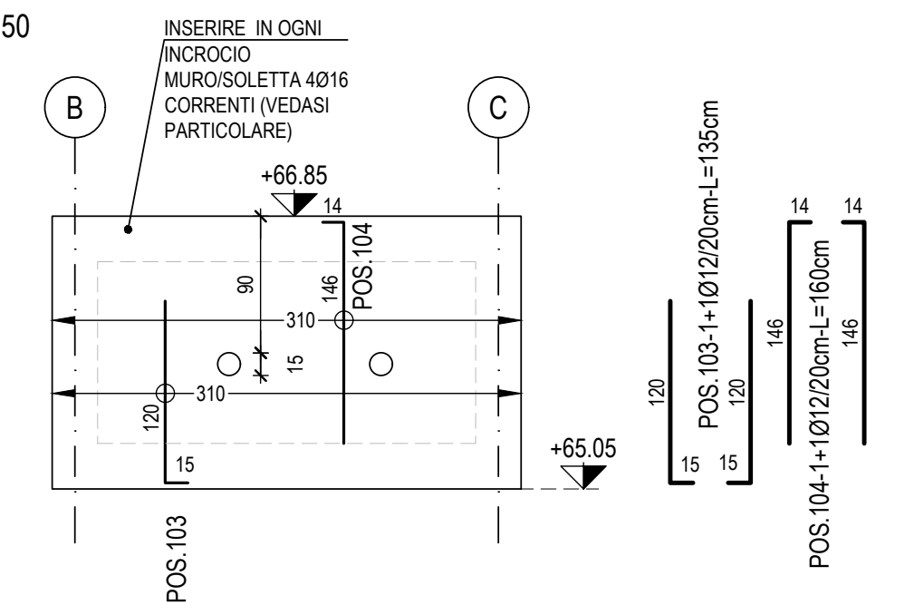
INSERIRE IN OGNI INCROCIO MURO/SOLETTA 4Ø16 CORRENTI (VEDASI PARTICOLARE)
+66.85
+65.05
POS.103
POS.104

PARETE FILO 1 - ARMATURA ORIZZONTALE
SCALA 1:50

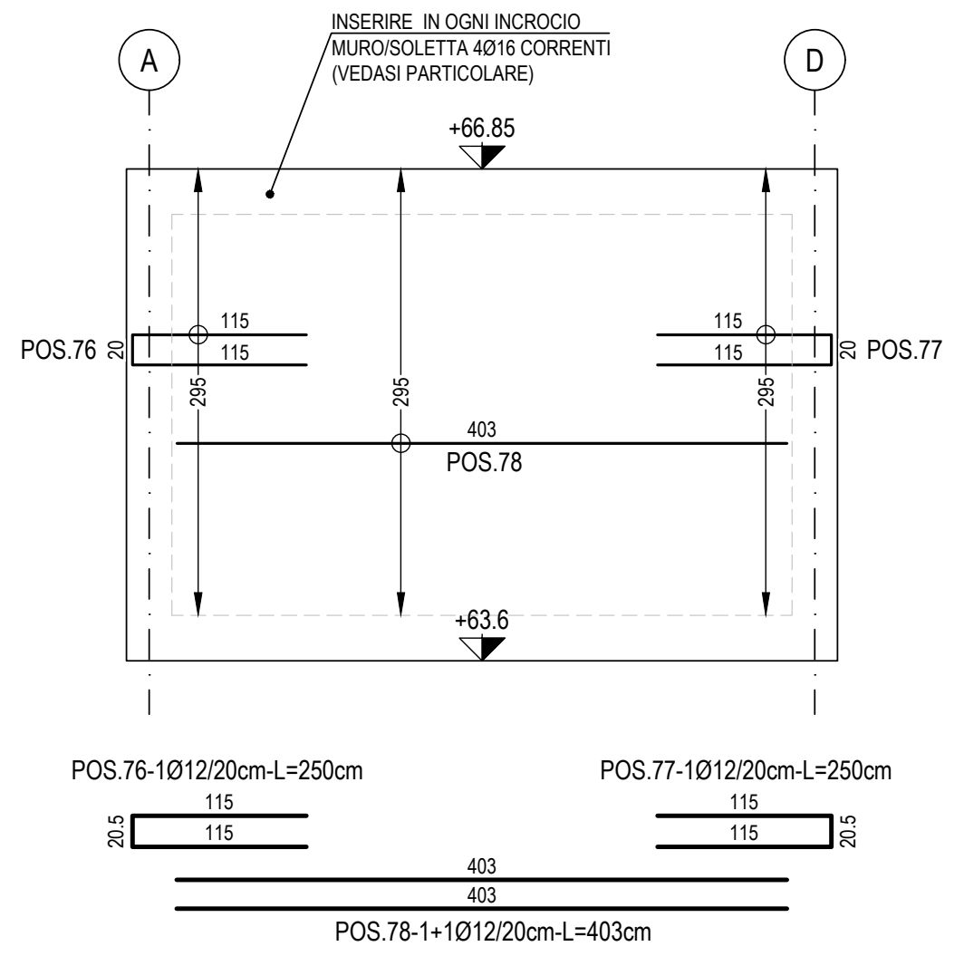
INSERIRE IN OGNI INCROCIO MURO/SOLETTA 4Ø16 CORRENTI (VEDASI PARTICOLARE)
+66.85
+63.6
POS.76
POS.77
POS.78
POS.76-1Ø12/20cm-L=250cm
POS.77-1Ø12/20cm-L=250cm
POS.78-1+1Ø12/20cm-L=403cm

PARETE FILO 1 - ARMATURA VERTICALE
SCALA 1:50

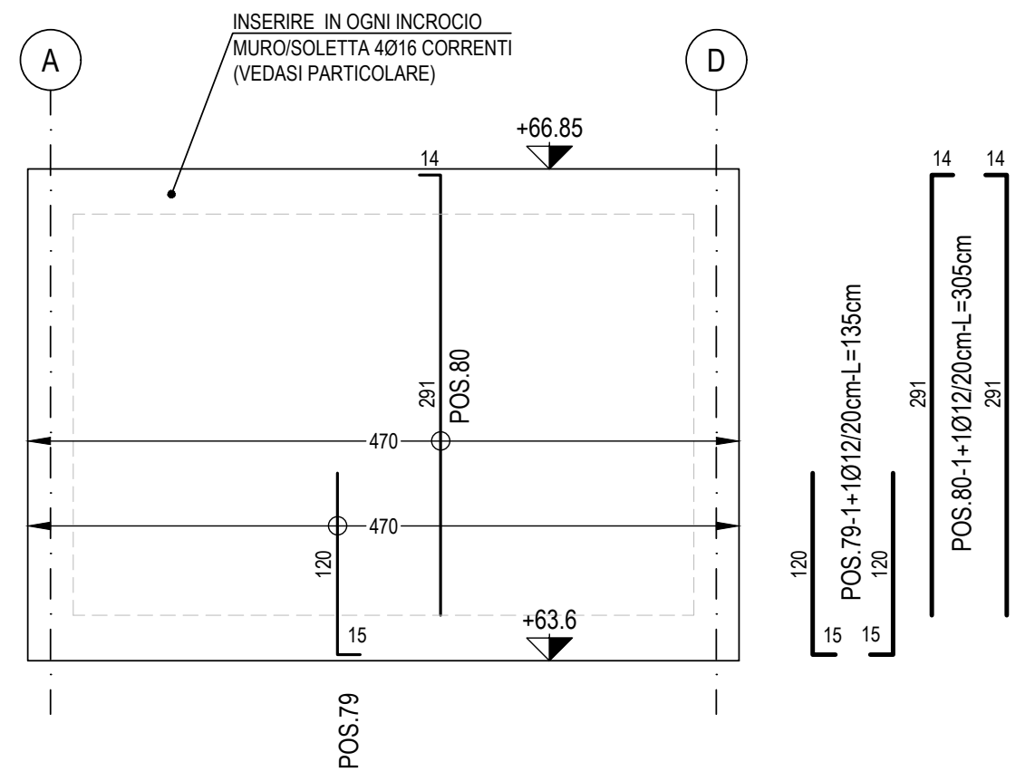
INSERIRE IN OGNI INCROCIO MURO/SOLETTA 4Ø16 CORRENTI (VEDASI PARTICOLARE)
+66.85
+63.6
POS.79
POS.80

ARMATURA INTEGRATIVA FORI RETTANGOLARI
SCALA 1:25

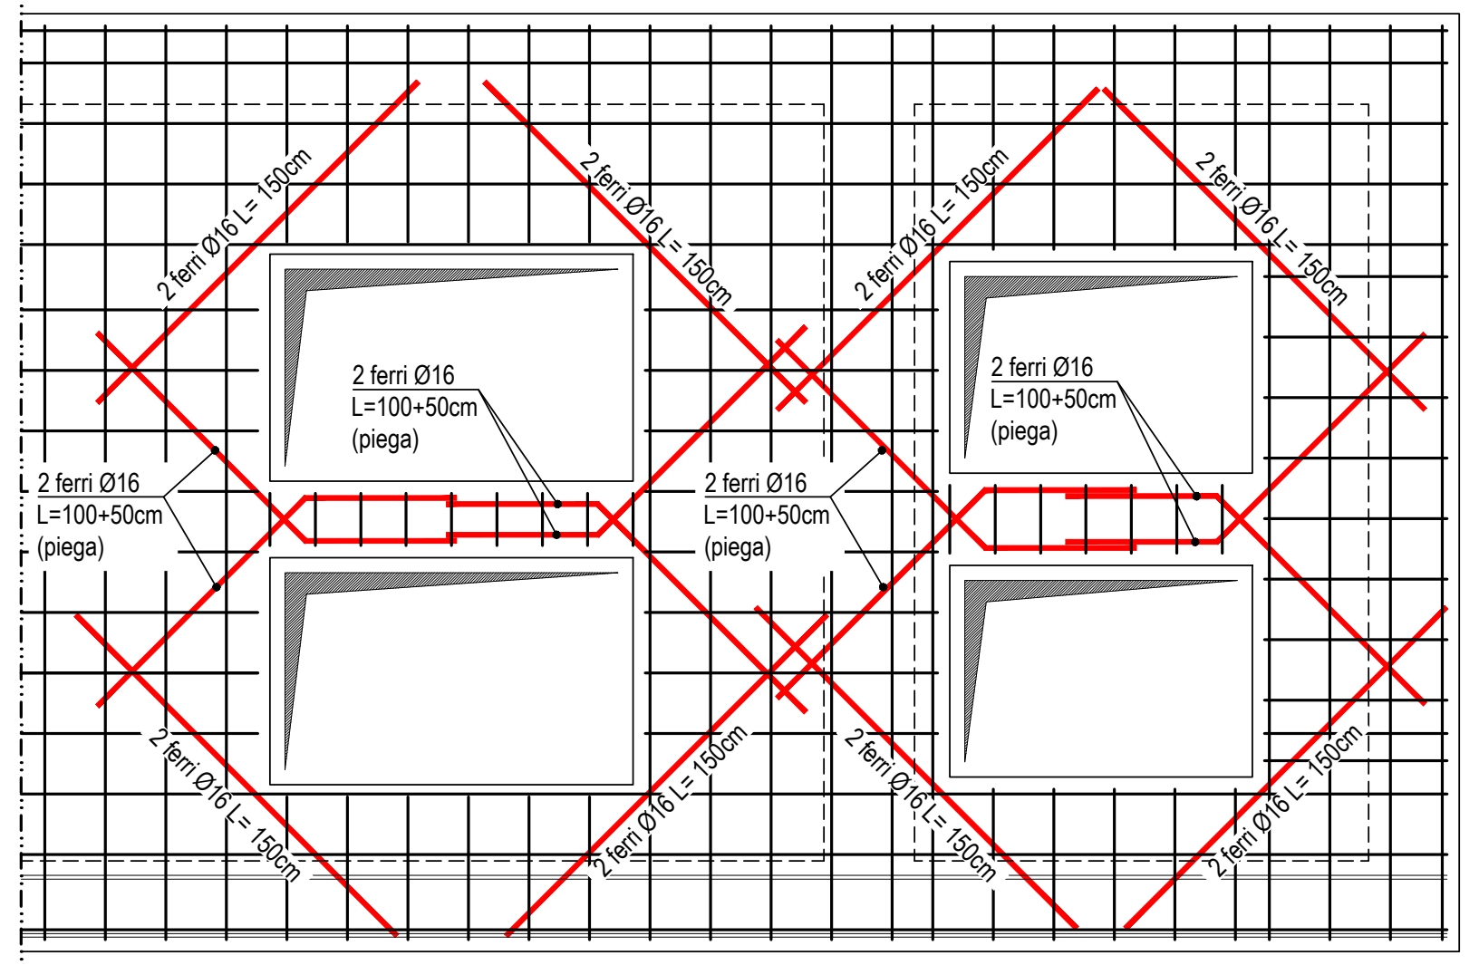

NOTA
- POSIZIONARE LE ARMATURE INTEGRATIVE PER BORDO FORO ALL'INTERNO DEGLI STRATI PRINCIPALI;
- POSIZIONARE ARMNATURA INTEGRATIVA ANCHE SU FORI CIRCOLARI
- ADATTARE LE MISURE DEI FERRI IN FUNZIONE DI BORDI O APERTURE ADIACENTI.

PARTICOLARE - ESEMPIO TIPOLOGICO INCROCIO MURO-SOLETTA
SEZIONE VERTICALE
SCALA 1:10

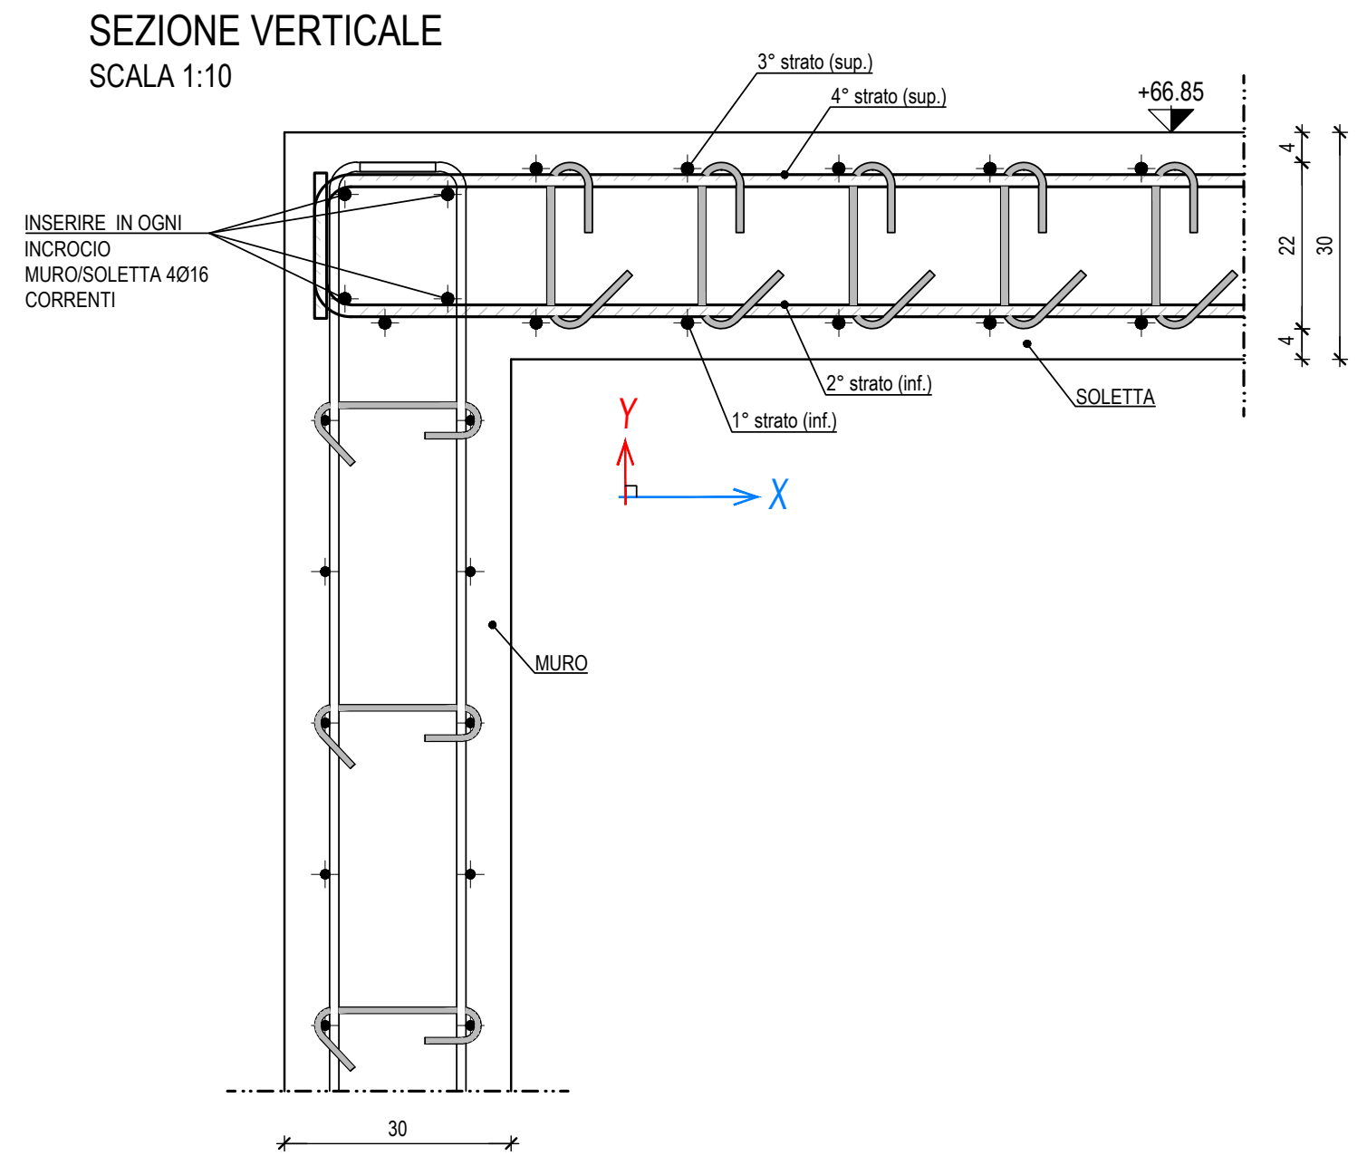

CARICHI DI PROGETTO

	TIPOLOGIA	CARICHI PERMANENTI	CARICHI ACCIDENTALI
SOLETTA DI CHIUSURA	ACCIDENTALE DISTRIBUITO ACCIDENTALE CONCENTRATO	- -	9.00 kN/mq 150 kN/ruota
	PERMANENTE PORTATO NEVE	2.00 kN/mq -	- kN/mq 0.80 kN/mq

PRESCRIZIONI SUI MATERIALI IN OPERA

CALCESTRUZZI PER: PLATEA, MURI, SOLETTE E TRAVI	
VITA NOMINALE DELL'OPERA:	50 anni
CLASSE DI RESISTENZA MINIMA:	C32/40
CLASSE DI ESPOSIZIONE (UNI EN 206 / UNI 11104):	XC4+XA2
CLASSE DI CONSISTENZA (UNI EN 206 / UNI 11104):	S4
MASSIMO RAPPORTO A/C (UNI EN 206 / UNI 11104):	0.50
CONTENUTO MINIMO DI CEMENTO (UNI EN 206 / UNI 11104):	340 kg/mc
DIMENSIONE NOMINALE MAX INERTI:	20 mm

ACCIAIO PER CALCESTRUZZO ARMATO
- ACCIAIO IN BARRE AD ADERENZA MIGL. TIPO B450C CONTROLLATO IN STABILIMENTO

COPRIFERRI (se non espressamente indicato negli elaborati)
- COPRIFERRO NOMINALE PER PLATEA, MURI E SOLETTE: 40mm
- COPRIFERRO NOMINALE PER TRAVI: 45mm

LEGENDA

▭	ELEMENTI DI PROGETTO ARCHITETTONICO
▨	MURATURE PORTANTI IN LATERIZIO SEZIONATE
═	MURATURE NON STRUTTURALI
▩	ELEMENTI IN LEGNO SEZIONATI
▩	ELEMENTI IN C.A. SEZIONATI
▒	ELEMENTI IN C.A. SOTTOSTANTI AL SOLAIO CONSIDERATO
☒ ○	IMPIANTI (TUBAZIONI SERVIZI IGIENICI, ECC)
±0.00 ⊕ ±0.00 ▽	QUOTE ALTIMETRICHE AL FINITO IN PIANTA/SEZIONE
±0.00 ◒ ±0.00 ▼	QUOTE ALTIMETRICHE AL GREZZO IN PIANTA/SEZIONE
▨	ELEMENTI IN MURATURA SEZIONATI
▭	ELEMENTI VISTI IN PROSPETTO
▨	ELEMENTI IN ACCIAIO SEZIONATI
▭	TRAVI E CORDOLI
◢	FORI SU SOLAIO
-··-··-	LINEE DI INTERRUZIONE DISEGNO

PIEGATURE ARMATURA

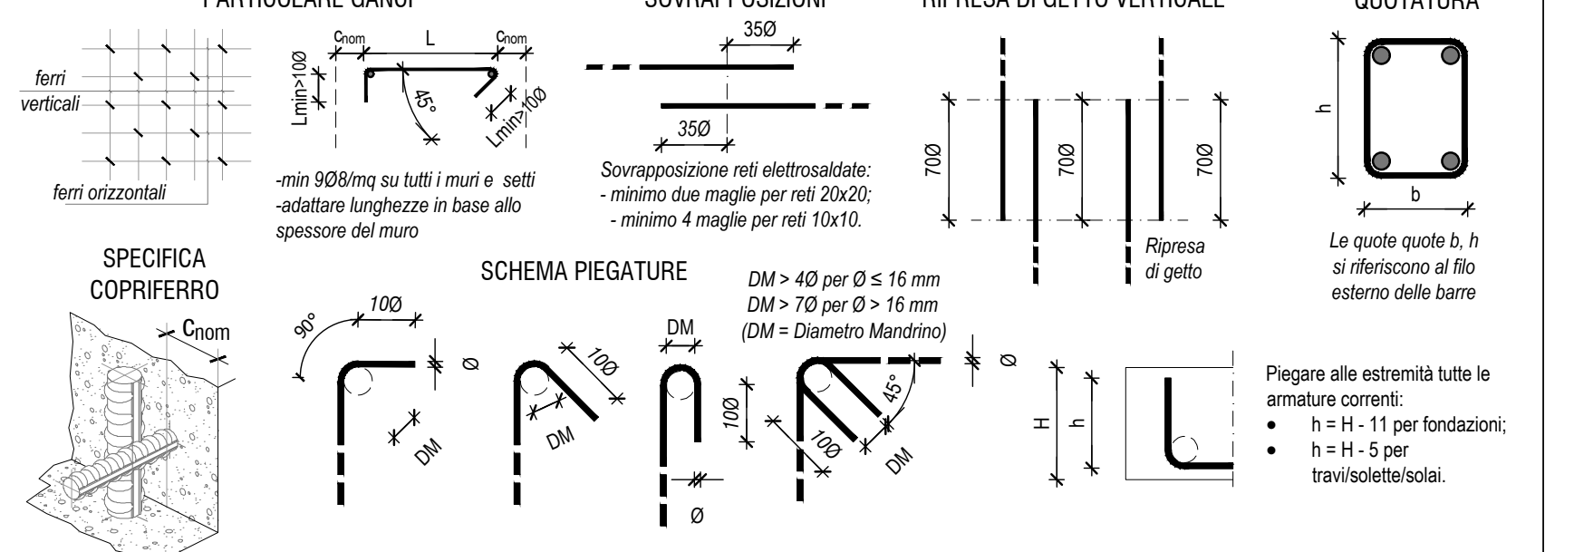
PARTICOLARE GANCI

-min 9Ø8/mq su tutti i muri e setti
-adattare lunghezze in base allo spessore del muro

PARTICOLARE SOVRAPPOSIZIONI

Sovrapposizione reti elettrosaldate:
- minimo due maglie per reti 20x20;
- minimo 4 maglie per reti 10x10.

PARTICOLARE RIPRESA DI GETTO VERTICALE

SPECIFICA QUOTATURA

Le quote quote b, h si riferiscono al filo esterno delle barre

SPECIFICA COPRIFERRO

SCHEMA PIEGATURE

DM > 4Ø per Ø ≤ 16 mm
DM > 7Ø per Ø > 16 mm
(DM = Diametro Mandrino)

Piegare alle estremità tutte le armature correnti:
- h = H - 11 per fondazioni;
- h = H - 5 per travi/solette/solai.

NORMATIVA: D.M. 17/01/2018 (Norme Tecniche per le costruzioni)
AZIONE SISMICA - IDENTIFICAZIONE DEL SITO E PARAMETRI DI CALCOLO

LOCALITA'	BARDOLINO (VR)
LONGITUDINE (WGS84)	10,7125
LATITUDINE (WGS84)	45,5630
VITA NOMINALE V_N	50 anni
CLASSE D'USO	II - C_U = 1,0
CATEGORIA TOPOGRAFICA	T1
CATEGORIA SOTTOSUOLO	Tipo C

NORMATIVA DI RIFERIMENTO:
- D.M. 17/01/2018 (Norme Tecniche per le costruzioni);
- C.Min. del 21 Gennaio 2019;
- UNI EN 1990 - “Criteri generali di progettazione strutturale”;
- UNI EN 1991 - “Azioni sulle strutture”;
- UNI EN 1992 - “Progettazione delle strutture in calcestruzzo”;
- UNI EN 1993 - “Eurocodice 3 - Progettazione delle strutture in acciaio”;
- UNI EN 1997 - “Progettazione geotecnica”;
- UNI EN 1998 - “Progettazione delle strutture per la resistenza sismica”;
- L. 5 Novembre 1971 n. 1086;
- REGOLAMENTO 305/2011-REGOLAMENTO 2024/3110;
- UNI EN 206:2021;
- UNI 11104:2025

NOTE :
- PER MAGGIORI INFORMAZIONI SI RIMANDA ALLA RELAZIONE DI CALCOLO E RELATIVE SPECIFICHE TECNICHE;
- L'ANALISI DEI CARICHI UTILIZZATA PER IL DIMENSIONAMENTO DELLE STRUTTURE E' CONTENUTA NELLA RELAZIONE DI CALCOLO. VERIFICARE LA CORRISPONDENZA TRA I CARICHI PERMANENTI PREVISTI NELLA RELAZIONE E LE FINITURE RIPORTATE NEGLI ELABORATI ARCHITETTONICI;
- EVENTUALI FORI DI PASSAGGIO IMPIANTI SULLE STRUTTURE PORTANTI DEVONO ESSERE PREVENTIVAMENTE COMUNICATI ED AUTORIZZATI DALLA D.L. DELLE OPERE STRUTTURALI.
- GLI ESECUTIVI STRUTTURALI SONO DA LEGGERSI UNITAMENTE A QUELLI ARCHITETTONICI ED IMPIANTISTICI. EVENTUALI DIFFERENZE PRESENTI TRA GLI ELABORATI DELLE VARIE DISCIPLINE DEVONO ESSERE COMUNICATE TEMPESTIVAMENTE AL DIRETTORE DEI LAVORI. I PROGETTISTI NON SONO RESPONSABILI DI TUTTE LE MODIFICHE APPORTATE SUCCESSIVAMENTE ALLA CONSEGNA UFFICIALE DEL PROGETTO ESECUTIVO CHE NON HANNO OTTENUTO IL RELATIVO BENESTARE

AZIENDA GARDESANA SERVIZI

ags azienda gardesana servizi

"INTERVENTI DI RIQUALIFICAZIONE DEL SISTEMA DI RACCOLTA DEI REFLUI NEL BACINO DEL LAGO DI GARDA - SPONDA VERONESE"
Lotto 1 - Tratto 4 - 2°Stralcio
"OPERE COLLETTORE IN PRESSIONE ED OPERE COMPLEMENTARI TRATTO PERGOLANA - ROCCA VELA - COMUNE BARDOLINO"
Lotto 8 - Tratto 4_OC
CIG: B7E3B750B2 - CUP: J33F17000010002

PROGETTO ESECUTIVO

PROGETTISTA E COORDINATORE SICUREZZA IN FASE DI PROGETTO:
Ing. Giovanni Battista Matteotti

COLLABORAZIONE:
Ing. Luca Petracin
Ing. Andrea Martinello
Ing. Emanuele Anderlini
Ing. Filiberto Boscolo Lisetto
Geom. Elisa Zatti

mass
INGEGNERIA E ARCHITETTURA SRL
Via Sorio 33/a, 35141 PADOVA
Tel: 049-723320 - Mail: Info@matteotti.com

ING. G.B. MATTEOTTI

RESPONSABILE UNICO DEL PROGETTO:
Dott. Ing. Carlo Alberto Voi

TITOLO	*SCALA*	*CODICE ELABORATO*
OPERE STRUTTURALI - NUOVO IMPIANTO DI SOLLEVAMENTO DI ROCCA VELA - tav. 2/2	1:50 - 1:25 - 1:10	C-02-000

N° REV	*DATA*	*DESCRIZIONE*	*ESEGUITO*	*VERIFICATO*	*APPROVATO*
00	Marzo 2026	PRIMA EMISSIONE	Ing. M. Dal Bò	Ing. L. Petracin	Ing. G. B. Matteotti
01					
02					
03					
04					