


IMPIANTO DI SOLLEVAMENTO DI SAN SEVERO
PIANTA MURI – CARPENTERIA
SCALA 1:50

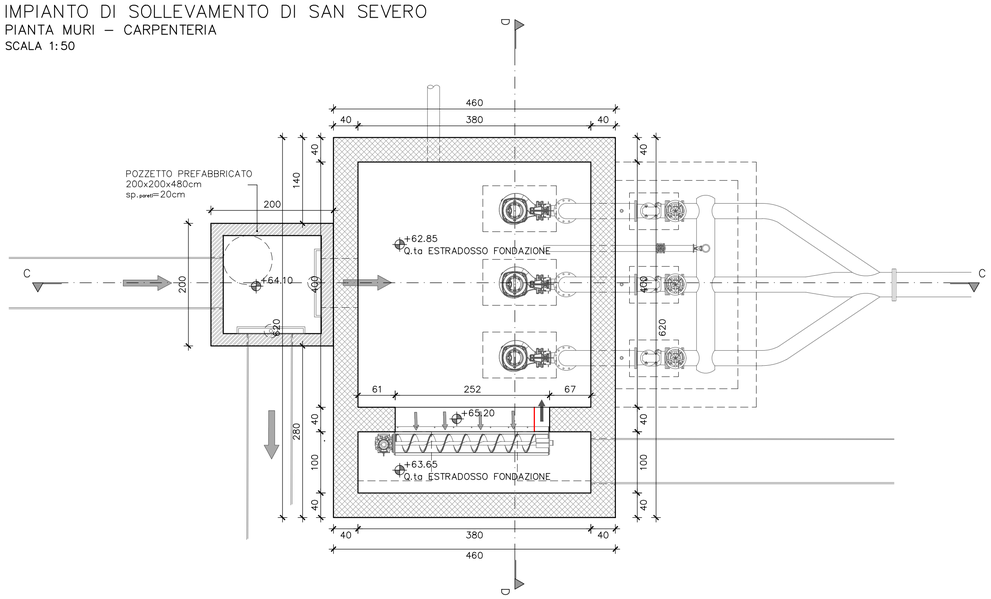

IMPIANTO DI SOLLEVAMENTO DI SAN SEVERO
PIANTA COPERTURA – CARPENTERIA
SCALA 1:50

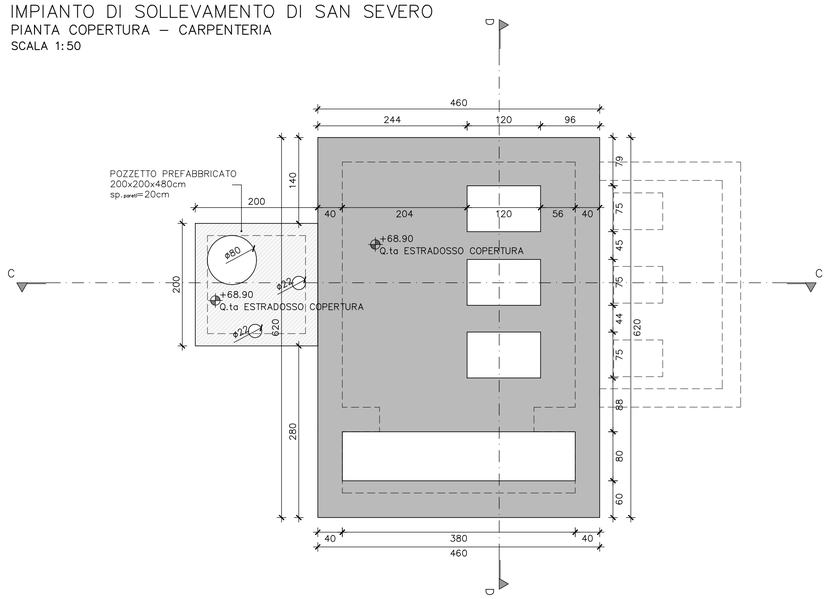

IMPIANTO DI SOLLEVAMENTO DI SAN SEVERO
SEZIONE C–C – CARPENTERIA
SCALA 1:50

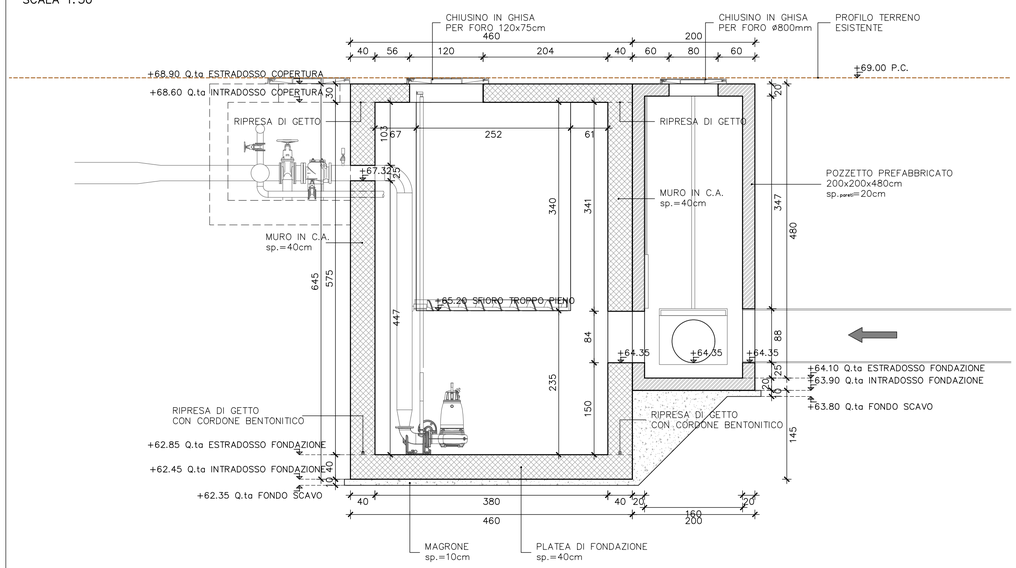

IMPIANTO DI SOLLEVAMENTO DI SAN SEVERO
SEZIONE D–D – CARPENTERIA
SCALA 1:50

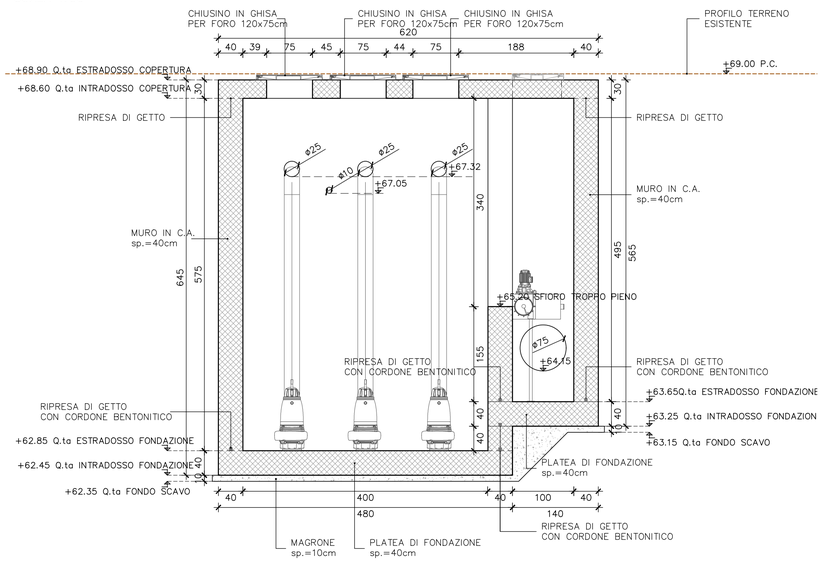


TABELLA MATERIALI

ACCIAIO

ACCIAIO PER CARPENTERIA METALLICA
(travi di ripartizione, puntelli, piastrame, etc...)

TIPO S355 (t≤40mm):
- Resistenza caratteristica a snervamento fyk: > 355 MPa
- Resistenza caratteristica a rottura: ftk > 510 MPa

ACCIAIO PER PALANCOLE

TIPO S355GP (t≤40mm):
- Resistenza caratteristica a snervamento fyk: > 355 MPa
- Resistenza caratteristica a rottura: ftk > 480 MPa

ACCIAIO PER C.A.
Rif. DM 17/01/2018

TIPO B450C saldabile:
- Resistenza caratteristica a snervamento fyk: > 450 MPa
- Resistenza caratteristica a rottura: ftk > 540 MPa

*Collegamento di barre d'armatura post-installate (inghisaggio):
Impiegare ancorante chimico epossidico ad alte prestazioni tipo Hilti HIT-RE 500 v4 o equivalente secondo indicazioni del fornitore

CALCESTRUZZO

CALCESTRUZZO MAGRO
E GETTI DI LIVELLAMENTO

- CLASSE DI RESISTENZA MINIMA: C12/15
- CLASSE DI ESPOSIZIONE AMBIENTALE: X0

CALCESTRUZZO PER OPERE DEFINITIVE
Rif. UNI EN 206

- CLASSE DI CONSISTENZA: S5
- CLASSE DI ESPOSIZIONE AMBIENTALE: XC4+XA2
- RAPPORTO MASSIMO a/c: 0.5
- CONTENUTO DI CLORURI: Cl<0.4
- DIAMETRO MASSIMO DEGLI INERTI: D_{max}=25mm
- CEMENTO RESISTENTE AI SOLFATI
- CLASSE DI RESISTENZA MINIMA: C32/40
- COPRIFERRO NOMINALE: 40 mm


SALDATURE

*TUTTE LE SALDATURE A CORDONE D'ANGOLO DOVRANNO AVERE SPESSORE DI GOLA MAGGIORE O UGUALE A 0,7 VOLTE LO SPESSORE MINIMO DA SALDARE.

*PER LA SALDATURA AD ARCO MANUALE DEVONO ESSERE IMPIEGATI ELOTTRODI RIVESTITI OMOLOGATI SECONDO UNI EN ISO 2560, SECONDO QUANTO PREVISTO AL 11.3.4.5 DELLE NTC 2018.


*SALDATURE DI PRIMA CLASSE PER GIUNTO A T A COMPLETA PENETRAZIONE (Dove non diversamente indicato)

PER TUTTE LE FLANGE
S1≥S2
H=0.7xS2
G=1.3xS2

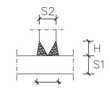

*SALDATURE A CORDONE D'ANGOLO
(Dove non diversamente indicato)

S1≥S2
H=S2
G=0.7xS2

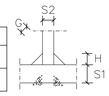

AZIENDA GARDESANA SERVIZI ags azienda gardesana servizi

"INTERVENTI DI RIQUALIFICAZIONE DEL SISTEMA DI RACCOLTA DEI REFLUI NEL BACINO DEL LAGO DI GARDA - SPONDA VERONESE"
Lotto 1 - Tratto 4 - 2°Stralcio
"OPERE COLLETTORE IN PRESSIONE ED OPERE COMPLEMENTARI TRATTO PERGOLANA - ROCCA VELA - COMUNE BARDOLINO"
Lotto 8 - Tratto 4_OC
CIG: B7E3B750B2 - CUP: J33F17000010002



PROGETTO ESECUTIVO

PROGETTISTA E COORDINATORE SICUREZZA IN FASE DI PROGETTO:
Ing. Giovanni Battista Matteotti

COLLABORAZIONE:
Ing. Luca Petracin
Ing. Andrea Martinello
Ing. Emanuele Anderlini
Ing. Filiberto Boscolo Lisetto
Geom. Elisa Zatti

mass INGEGNERIA E ARCHITETTURA SRL
Via Sorio 30/a, 35141 PADOVA
Tel. 049-723320 - Mail: Info@mattеotti.com

RESPONSABILE UNICO DEL PROGETTO:
Dott. Ing. Carlo Alberto Voi

TITOLO	*SCALA*	*CODICE ELABORATO*
NUOVO IMPIANTO DI SOLLEVAMENTO DI SAN SEVERO - Opere Strutturali - Carpenterie, piante e sezioni	1:50	C-3-002

N° REV	*DATA*	*DESCRIZIONE*	*ESEGUITO*	*VERIFICATO*	*APPROVATO*
00	Marzo 2026	PRIMA EMISSIONE		Ing. L. Petracin	Ing. G. B. Matteotti
01	Aprile 2026	AGGIORNAMENTO A SEGUITO DI VERIFICA		Ing. L. Petracin	Ing. G. B. Matteotti
02	Luglio 2026	AGGIORNAMENTO POST VERIFICA AGS		Ing. L. Petracin	Ing. G. B. Matteotti
03					
04					