## IMPIANTO DI SOLLEVAMENTO SAN SEVERO
PIANTA PLATEE E RIPRESE PARETI – ARMATURA
1:20

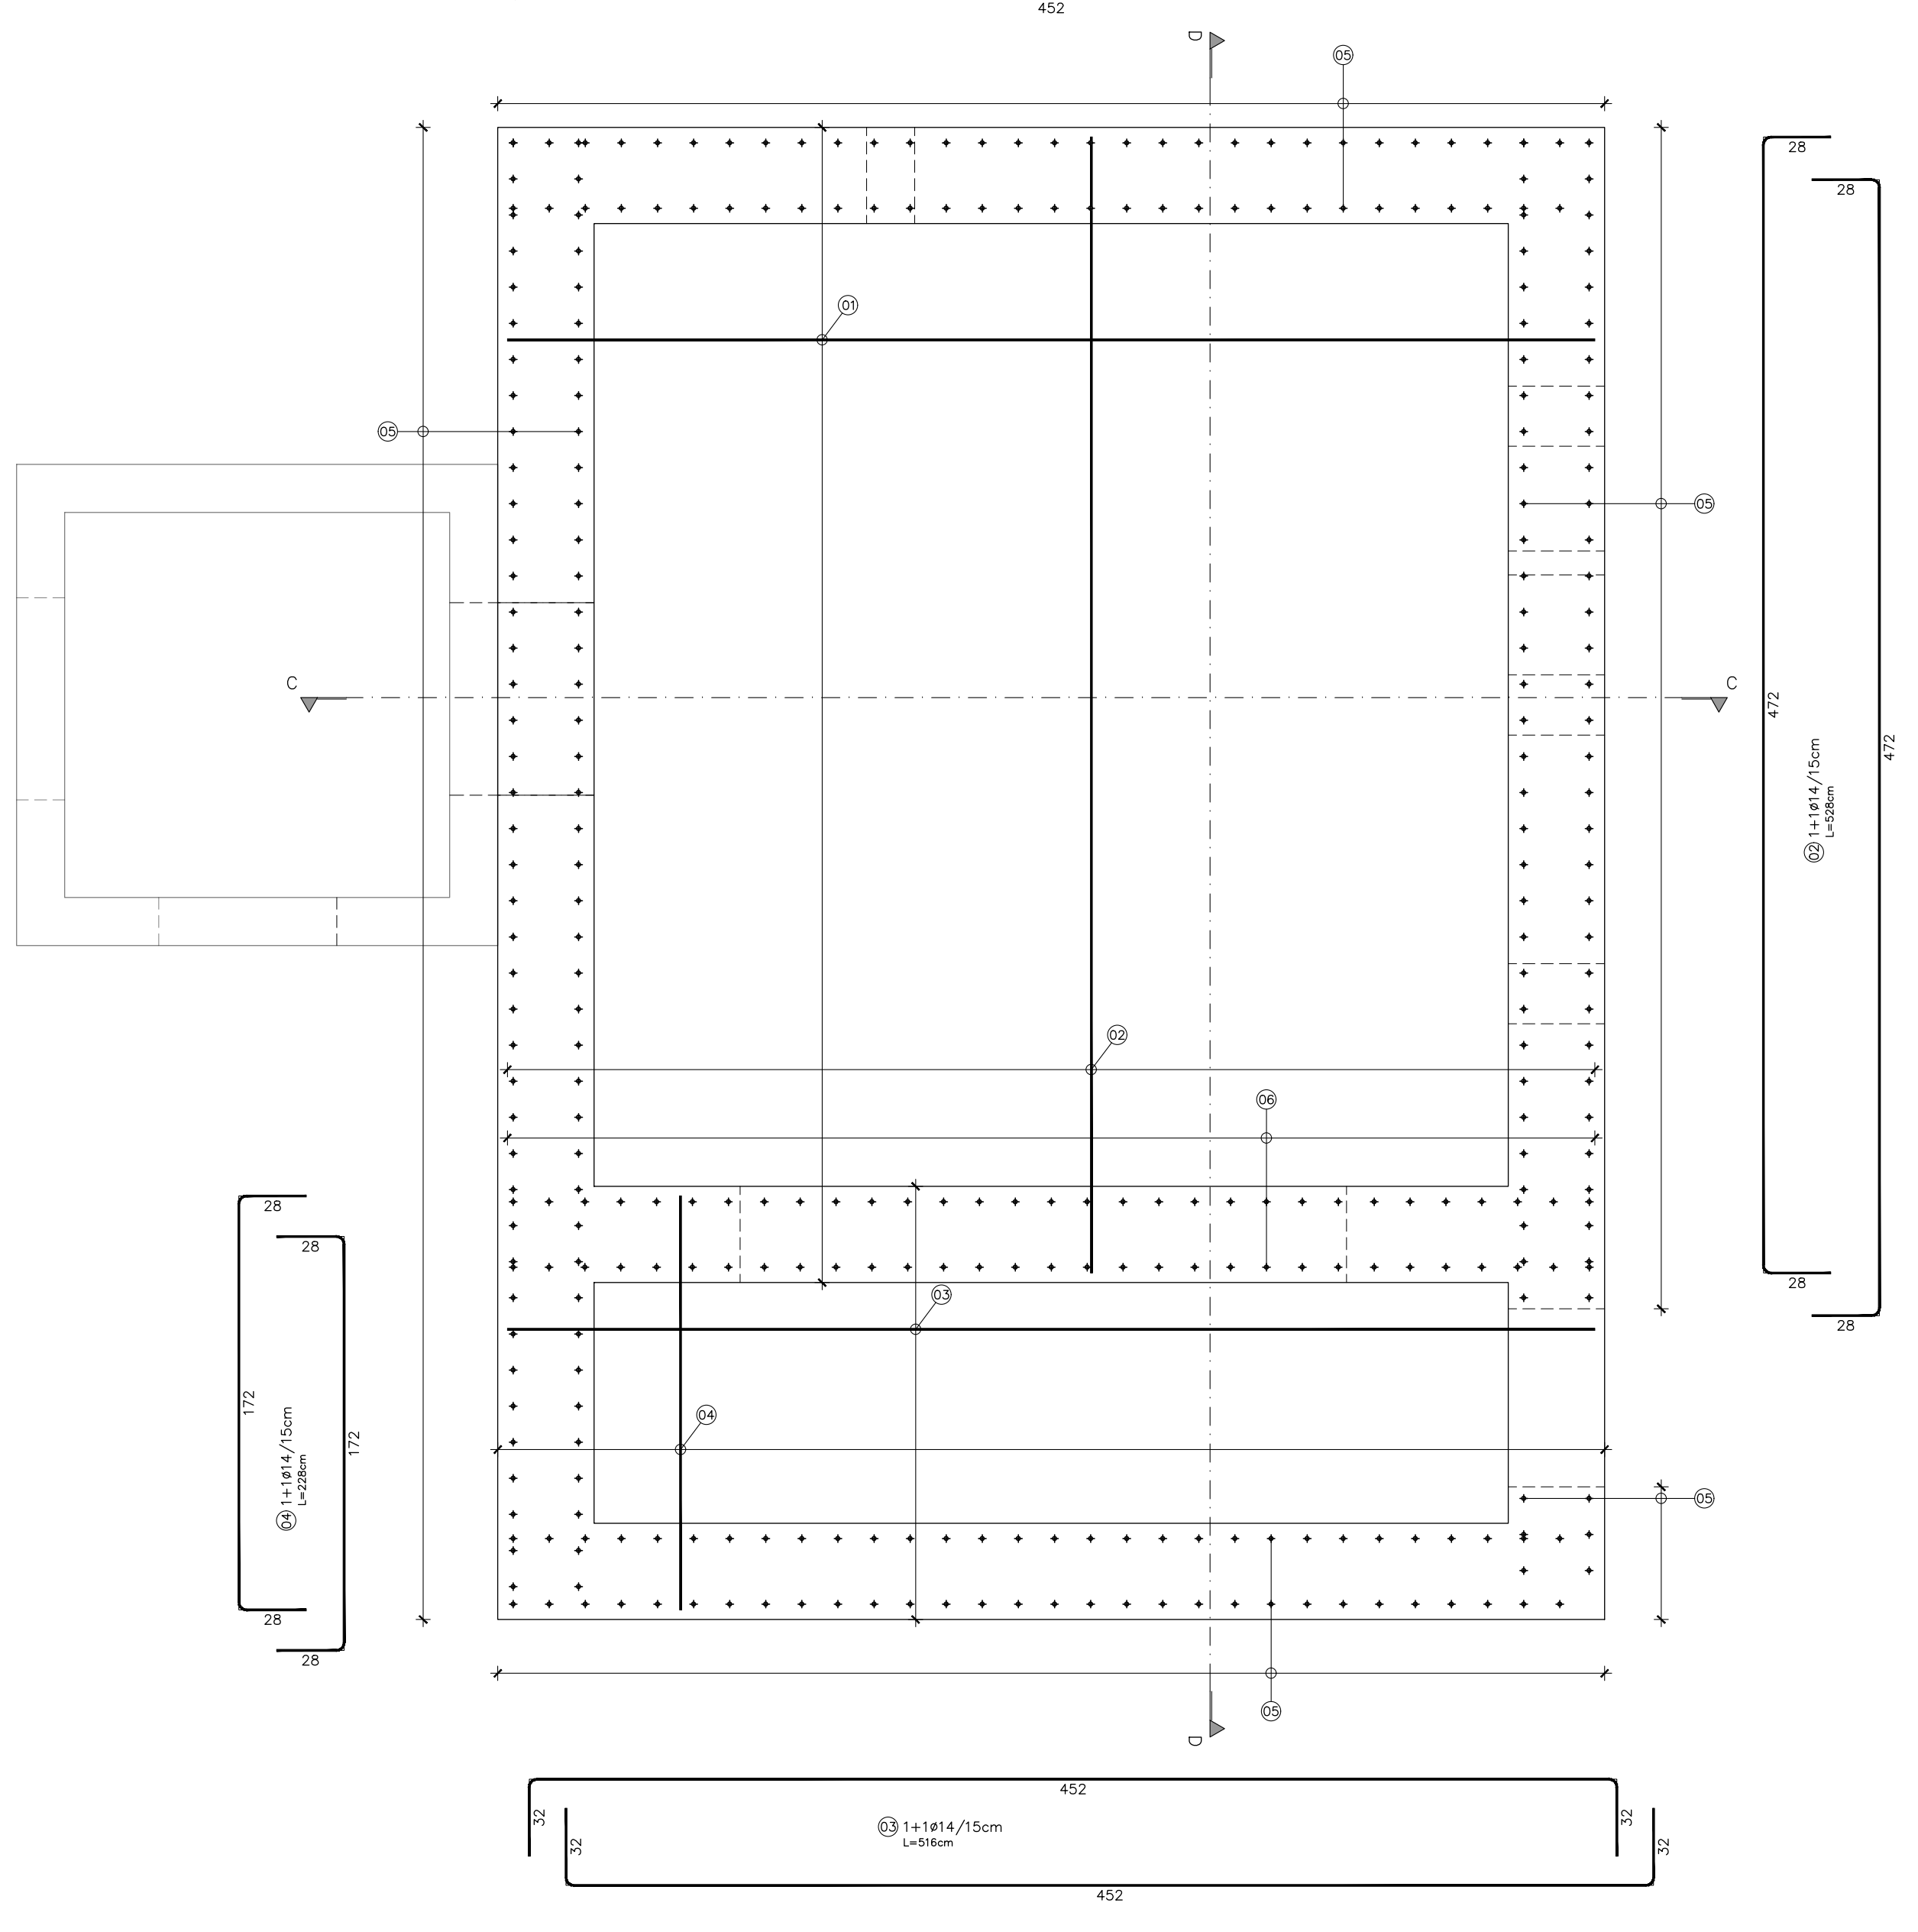

## IMPIANTO DI SOLLEVAMENTO SAN SEVERO
PIANTA MURI– ARMATURA
1:20

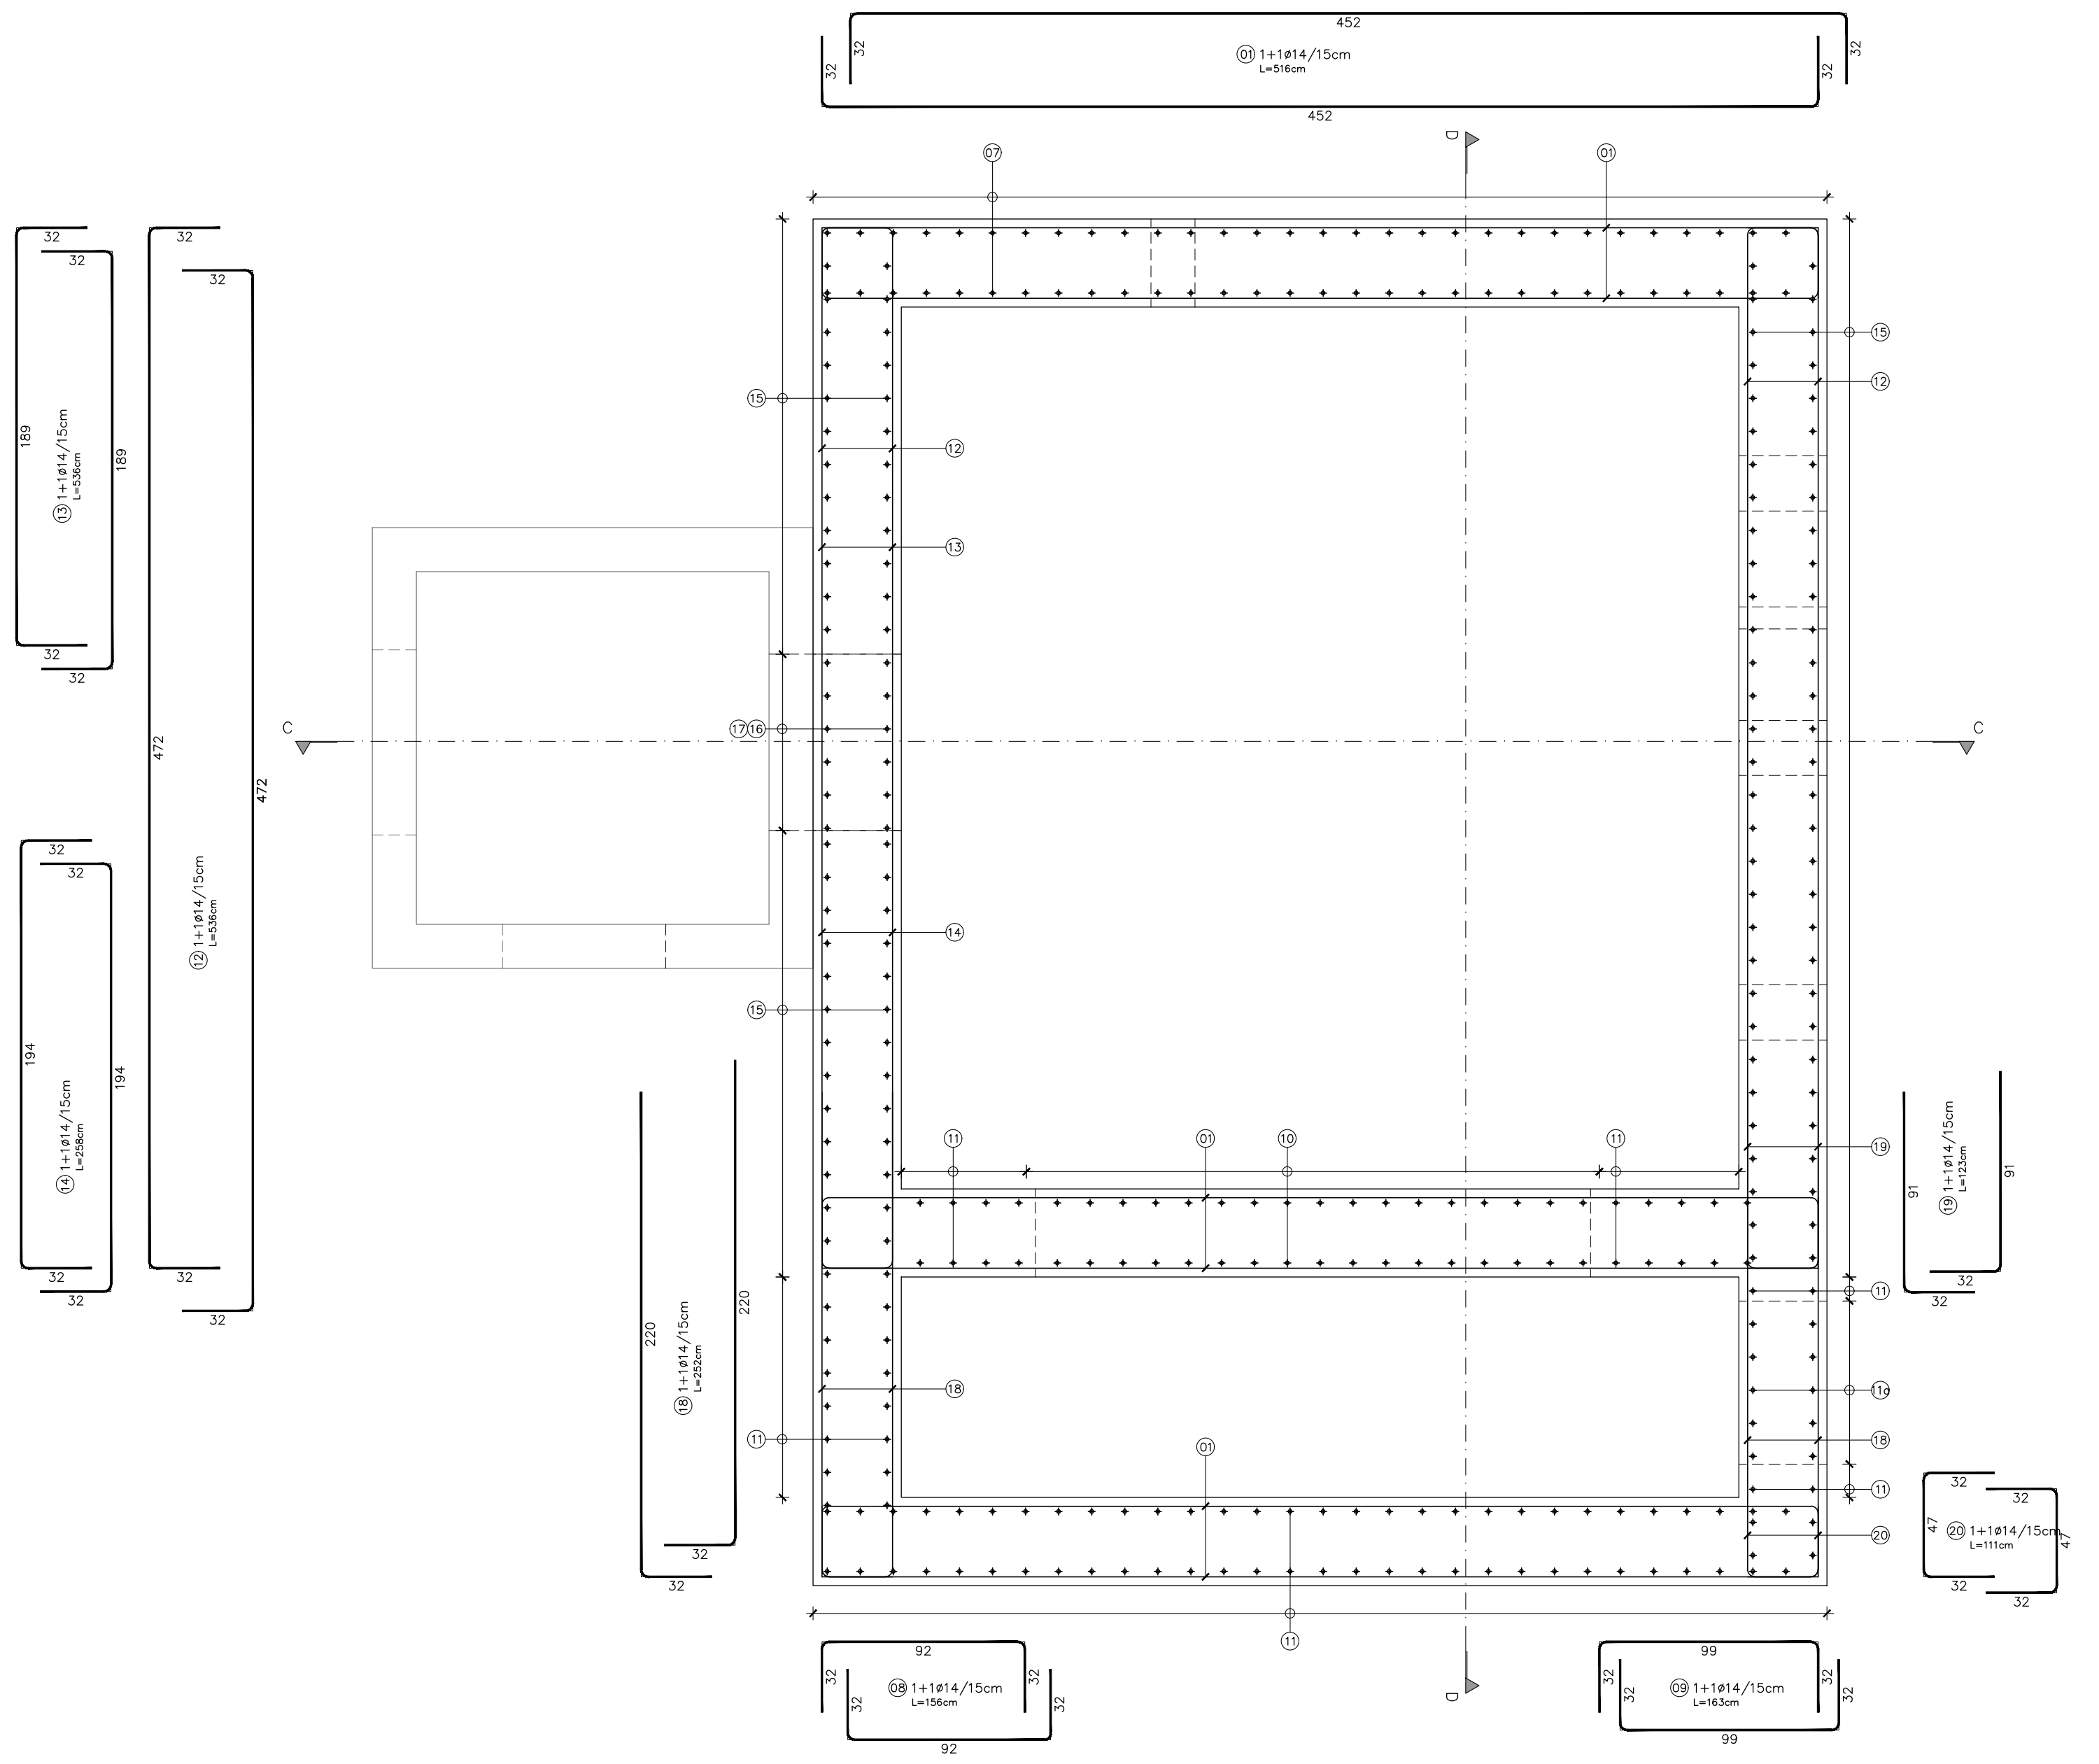

## IMPIANTO DI SOLLEVAMENTO SAN SEVERO
PIANTA COPERTURA– ARMATURA
1:20

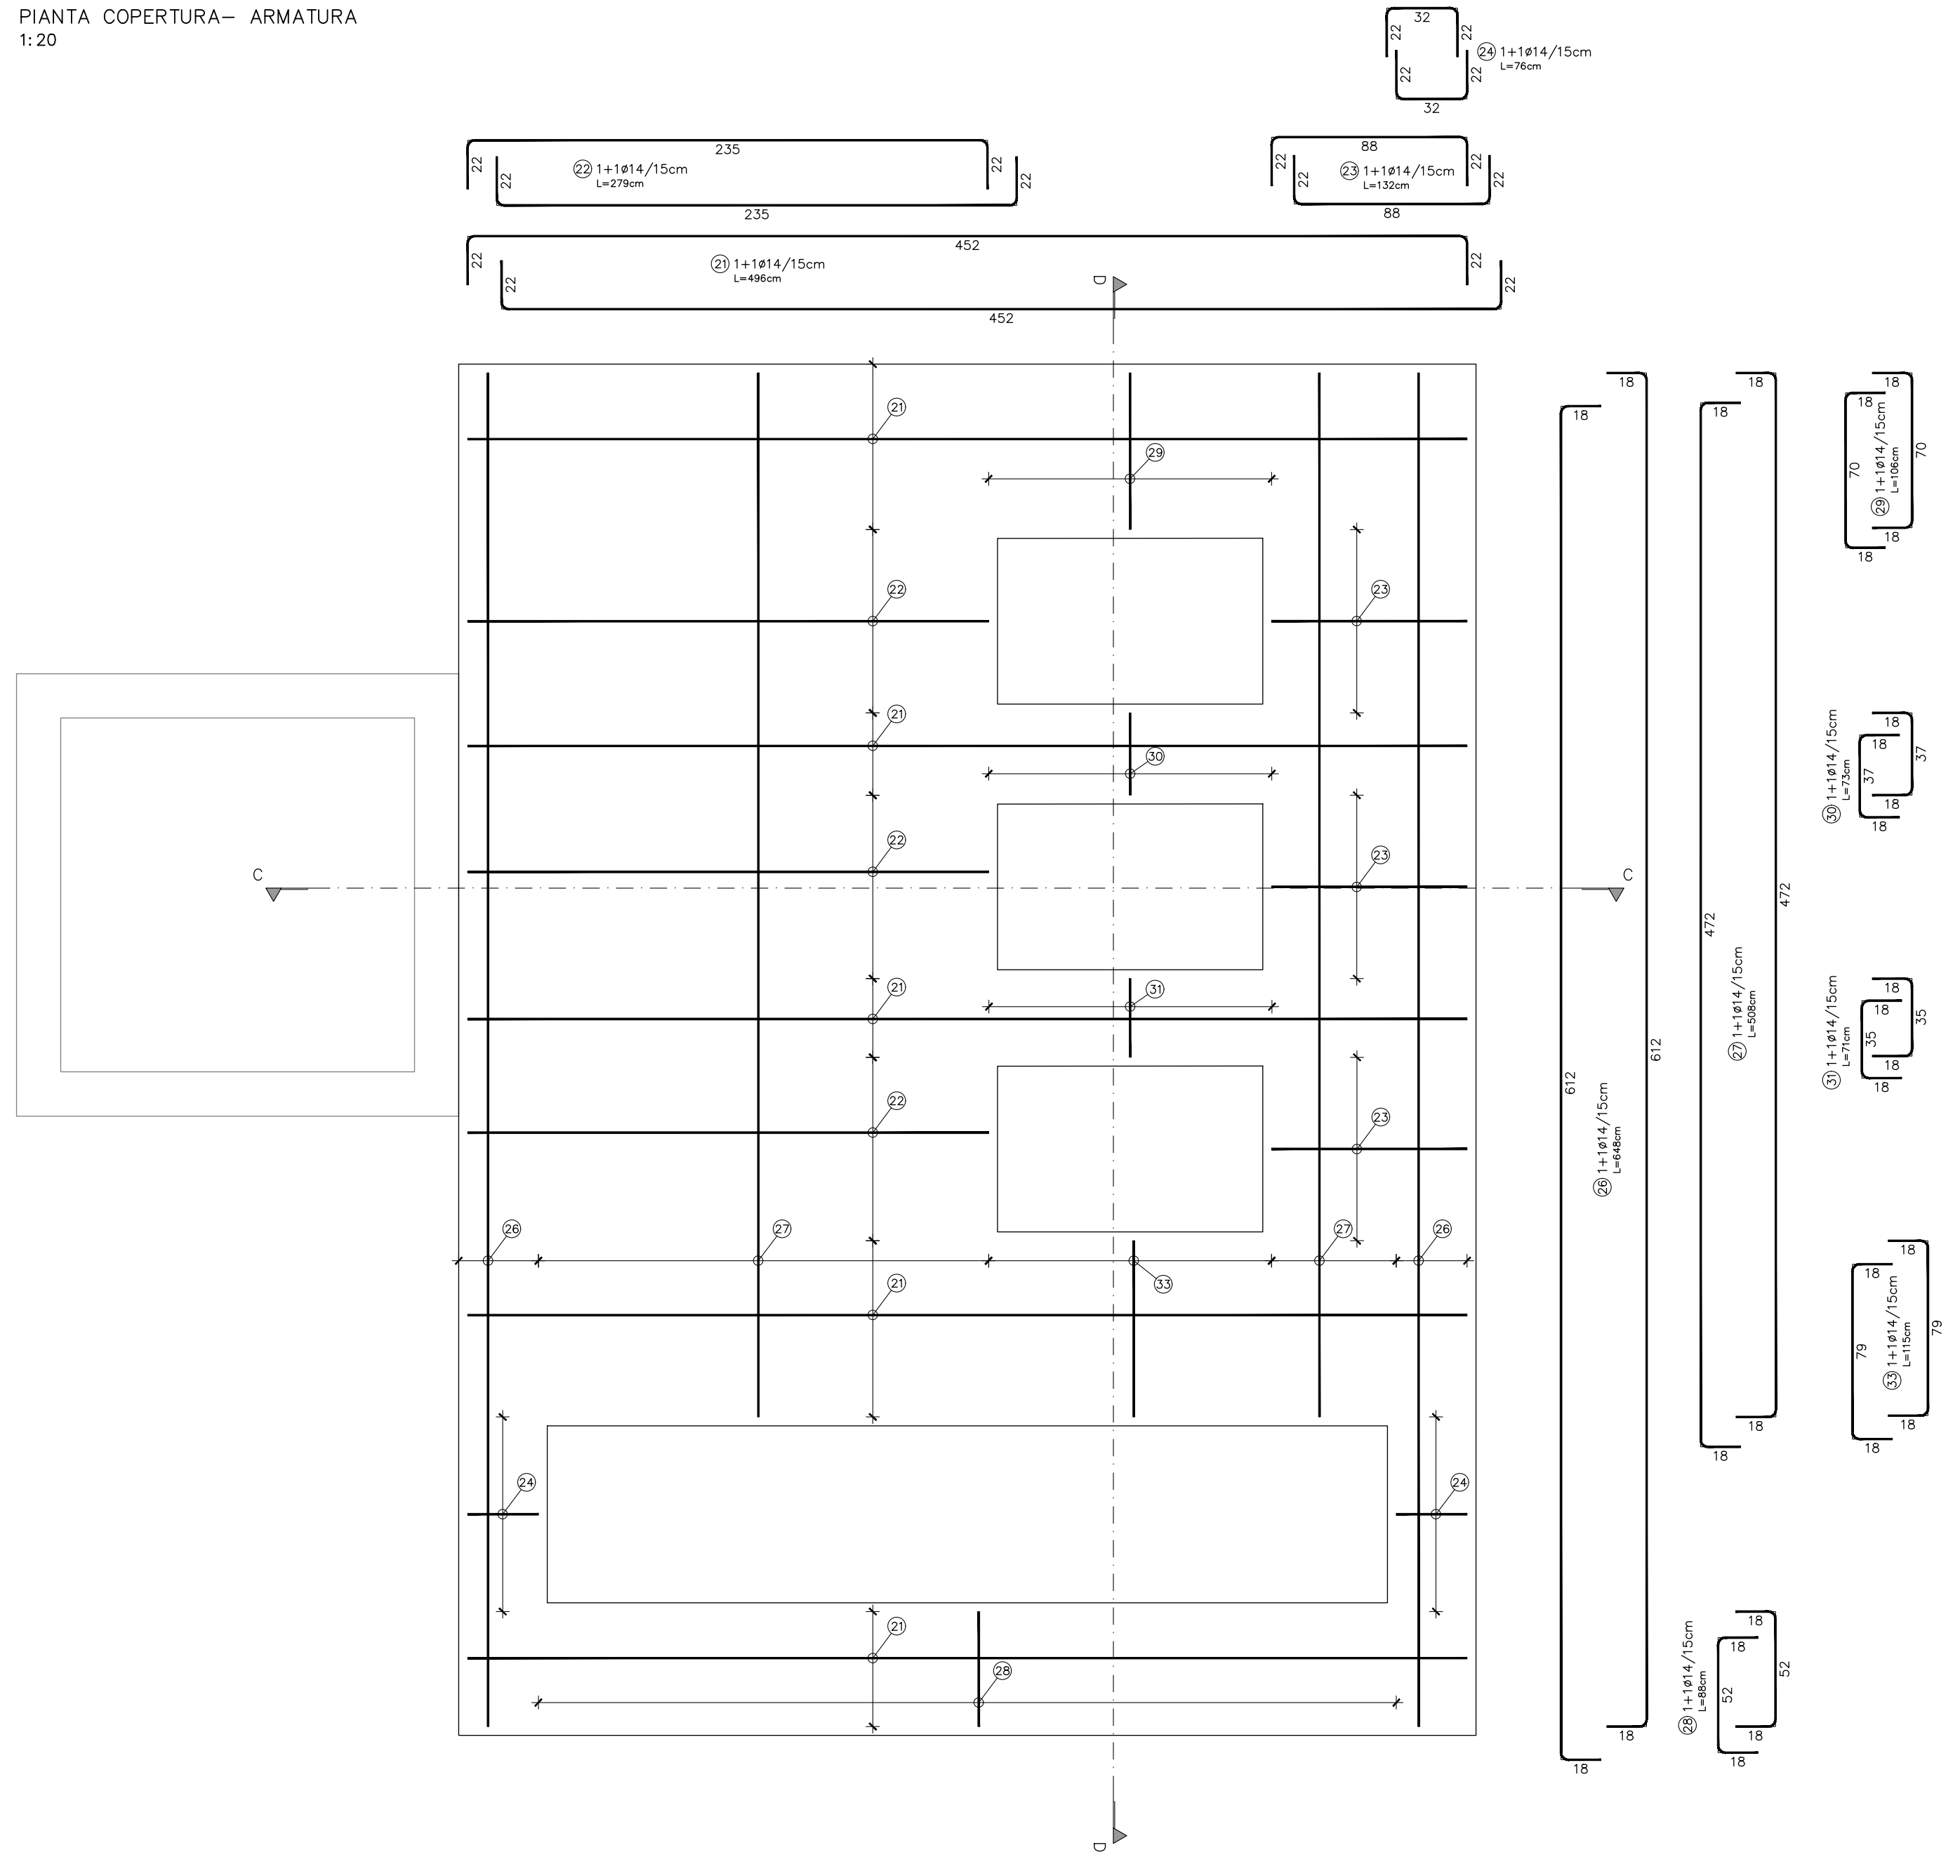

## IMPIANTO DI SOLLEVAMENTO SAN SEVERO
SEZIONE C–C – ARMATURA
1:20

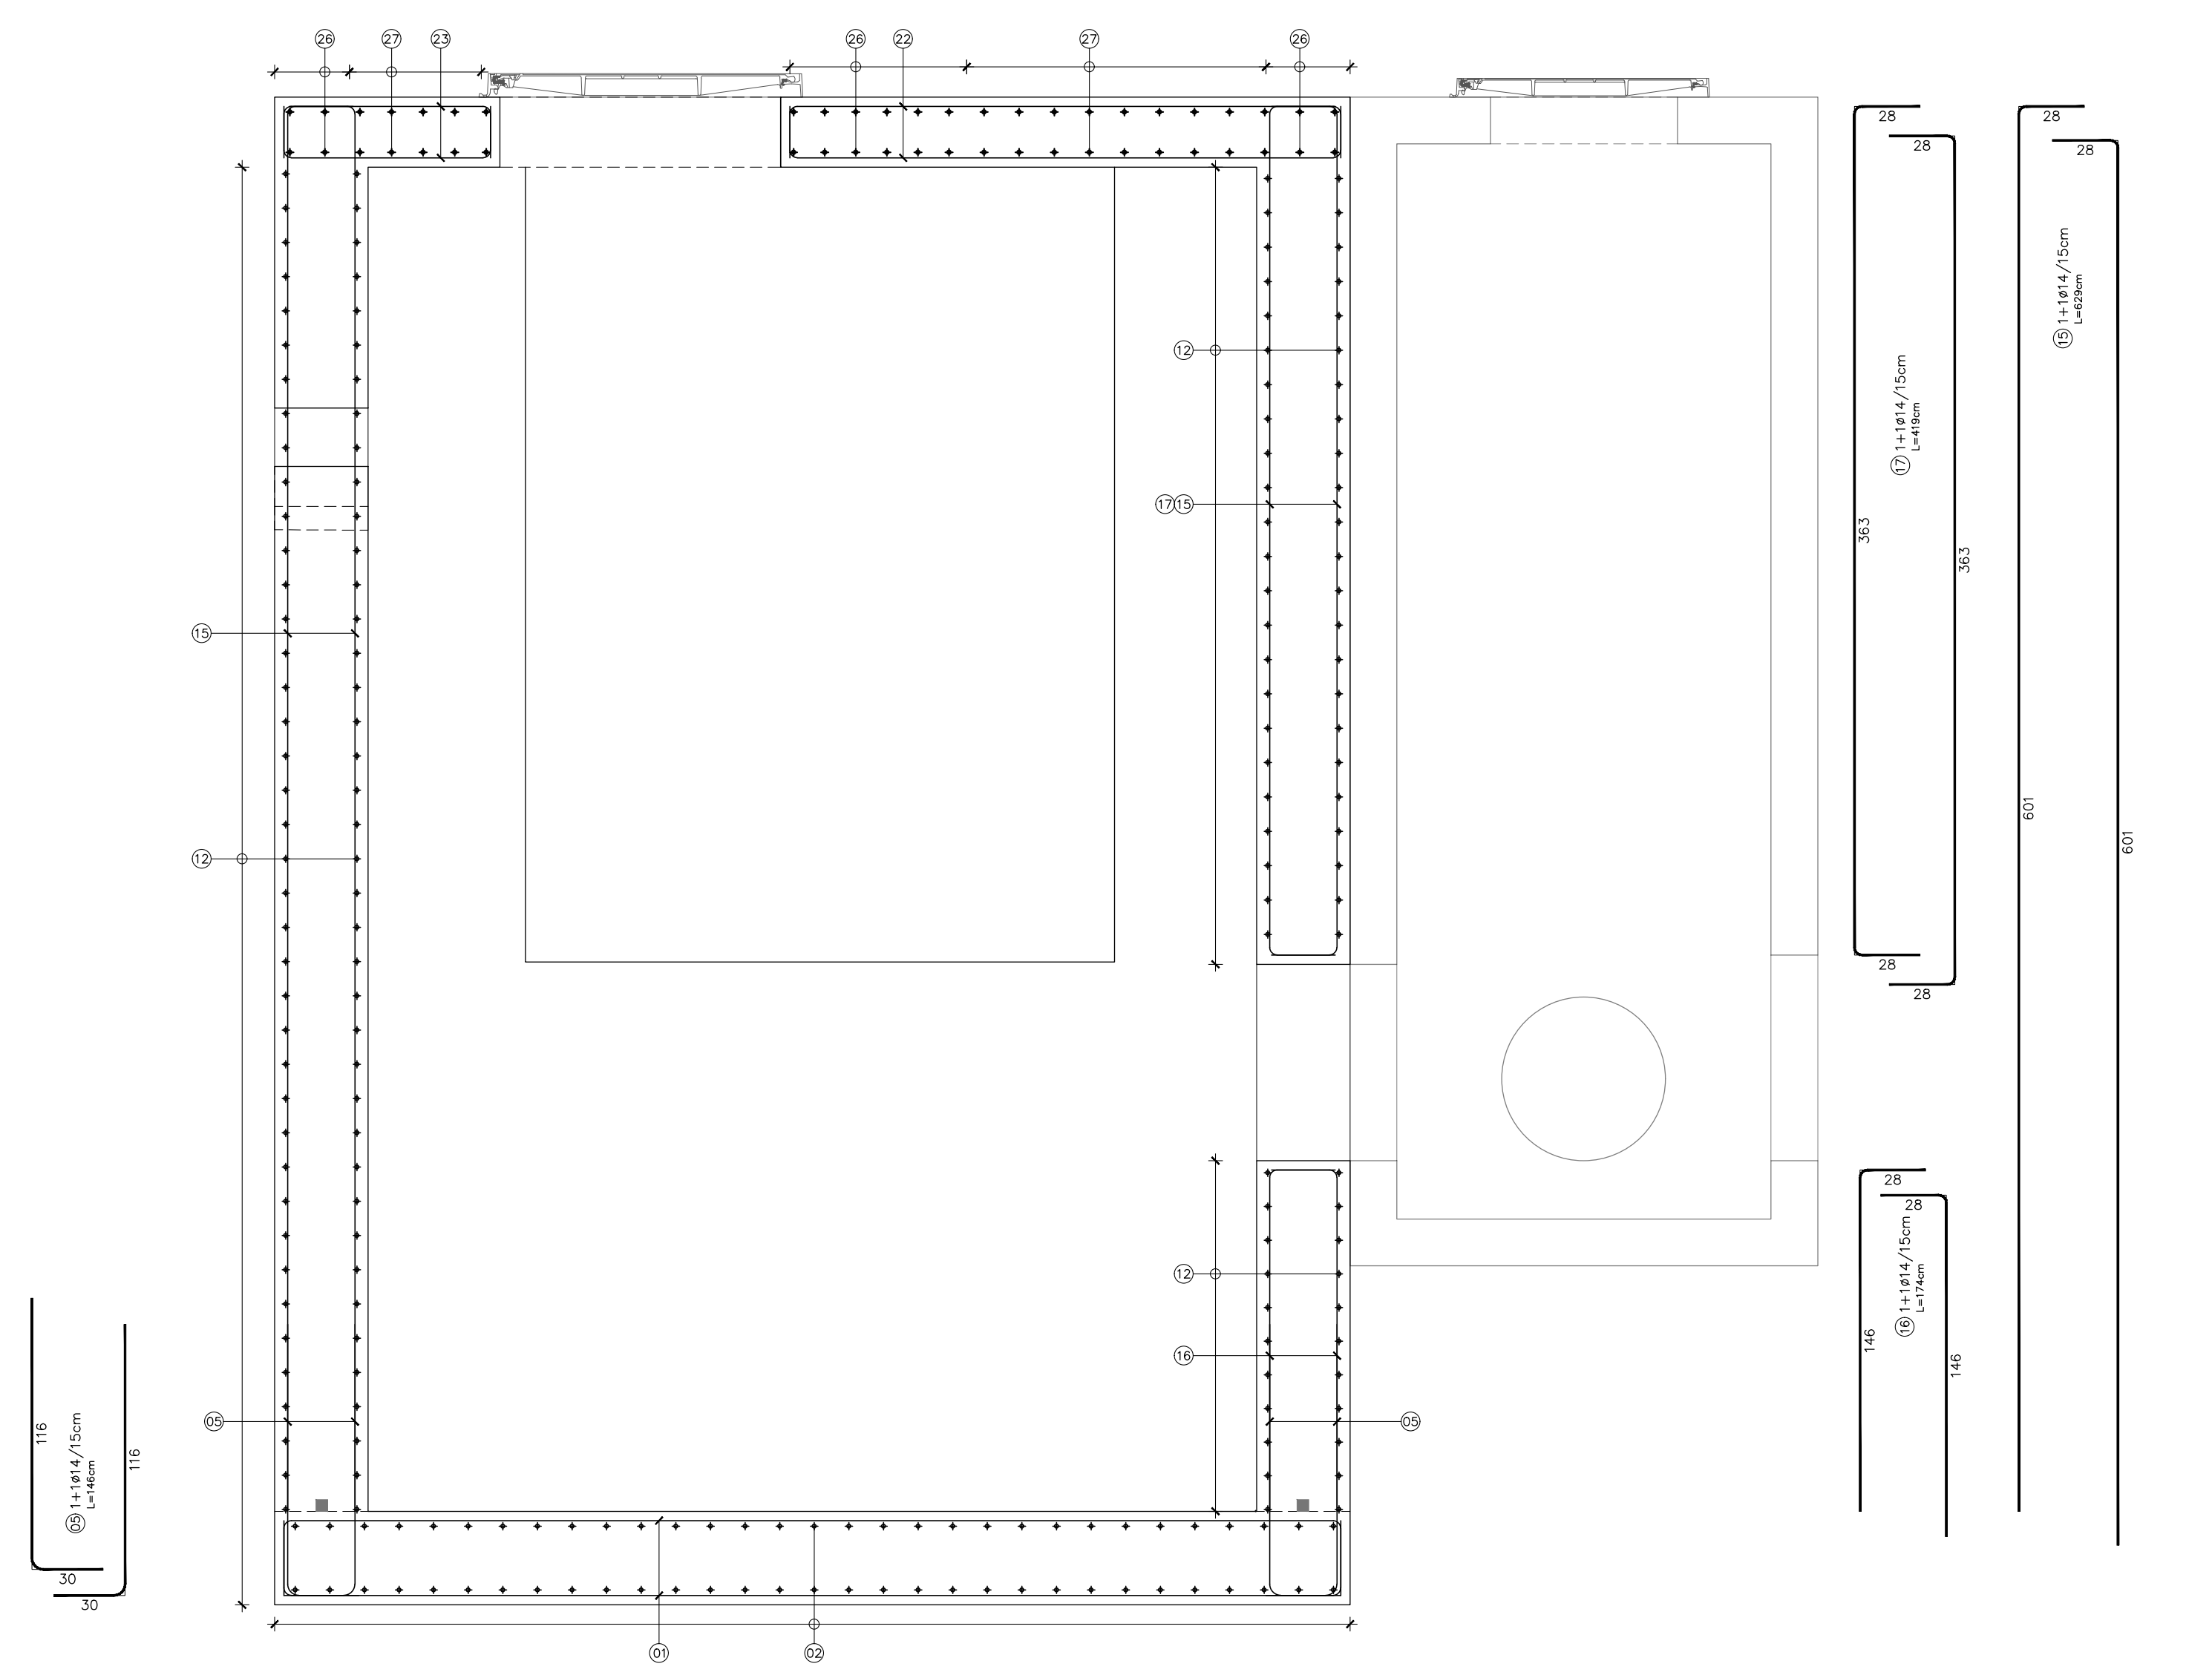

## IMPIANTO DI SOLLEVAMENTO SAN SEVERO
SEZIONE D–D – ARMATURA
1:20

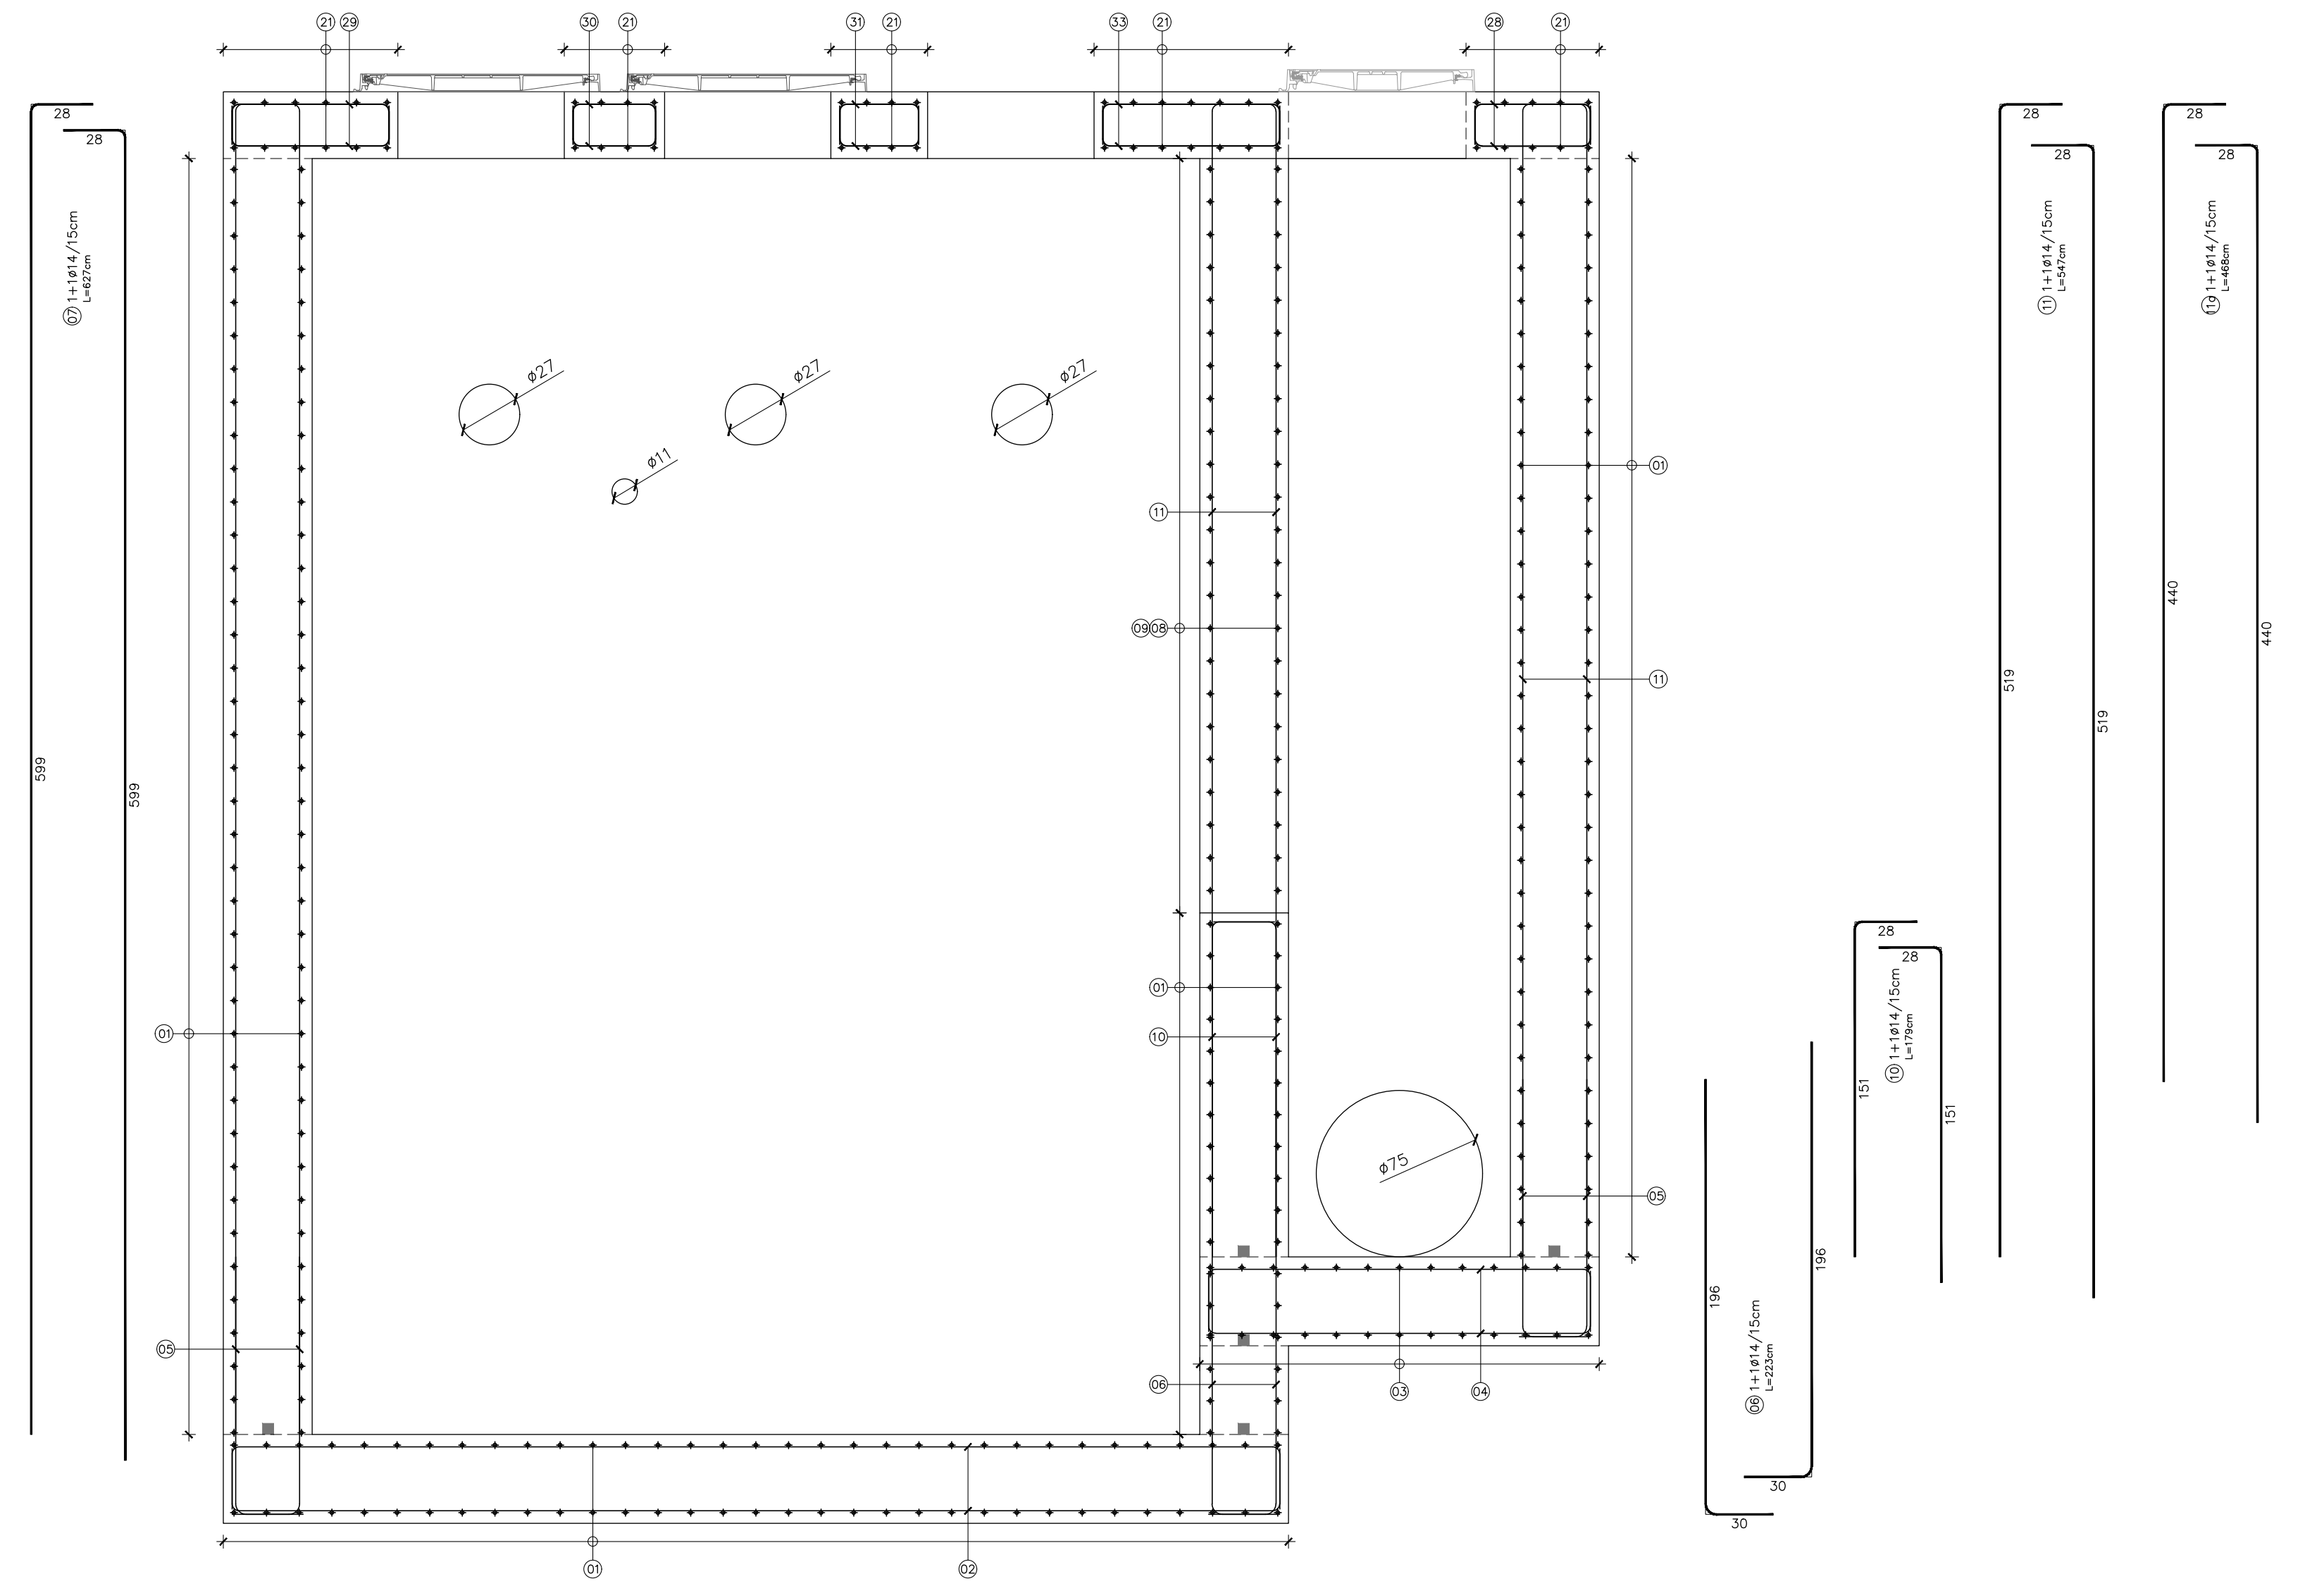

## DETTAGLIO FORO CIRCOLARE
ARMATURA INTEGRATIVA
SCALA 1:50

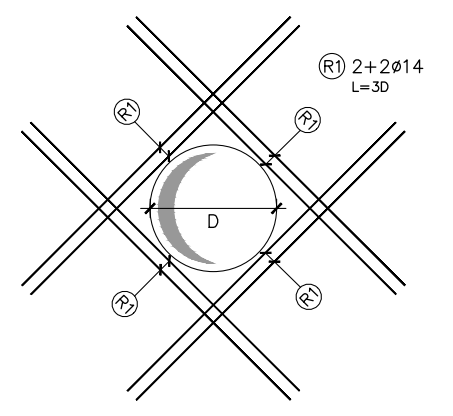

## DETTAGLIO FORO RETTANGOLARE
ARMATURA INTEGRATIVA
SCALA 1:50

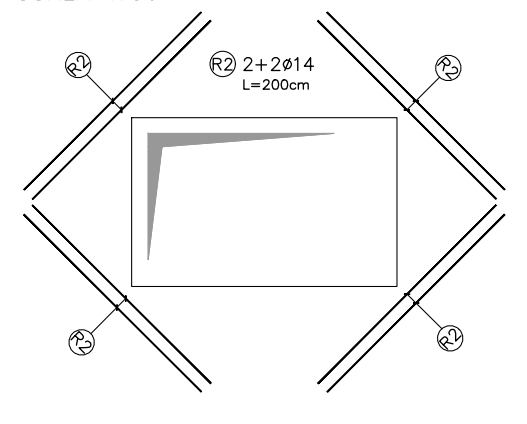

NOTA:
IN CORRISPONDENZA DI EVENTUALI FORI PRESENTI:
- INTERROMPERE I FERRI DI ARMATURA BASE IN ENTRAMBE LE DIREZIONI;
- INSERIRE FORCHETTE DI CHIUSURA (POS. F1) E FERRI DI RINFORZO (cfr. DETTAGLI FORO CIRCOLARE E RETTANGOLARE)

80 / 32 / 80 F1 1ø14/15cm L=192cm

## DETTAGLIO DISTANZIATORI
SOLETTA sp.40cm
SCALA 1:50

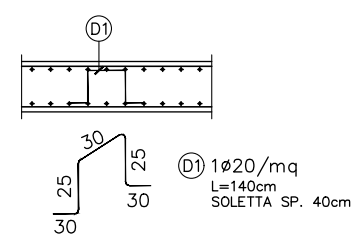

## DETTAGLIO ARMATURA A TAGLIO
SCHEMA DISPOSIZIONE
SCALA 1:20

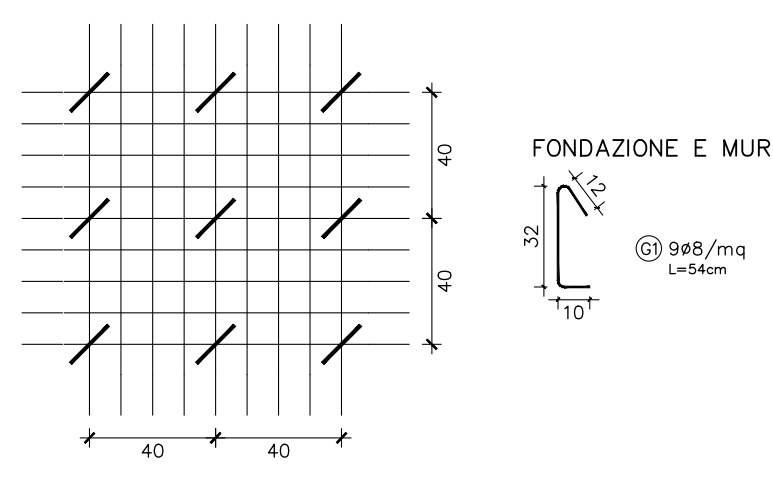

## TABELLA MATERIALI

### ACCIAIO

**ACCIAIO PER CARPENTERIA METALLICA**
(travi di ripartizione, puntelli, piastrame, etc...)

TIPO S355 (t≤40mm):
- Resistenza caratteristica a snervamento: fyk > 355 MPa
- Resistenza caratteristica a rottura: ftk > 510 MPa

**ACCIAIO PER PALANCOLE**

TIPO S355GP (t≤40mm):
- Resistenza caratteristica a snervamento: fyk > 355 MPa
- Resistenza caratteristica a rottura: ftk > 480 MPa

**ACCIAIO PER C.A.**
Rif. DM 17/01/2018

TIPO B450C saldabile:
- Resistenza caratteristica a snervamento: fyk > 450 MPa
- Resistenza caratteristica a rottura: ftk > 540 MPa

- Collegamento di barre d'armatura post–installate (inghisaggio):
Impiegare ancorante chimico epossidico ad alte prestazioni tipo Hilti HIT–RE 500 v4 o equivalente secondo indicazioni del fornitore

### CALCESTRUZZO

**CALCESTRUZZO MAGRO**
E GETTI DI LIVELLAMENTO

- CLASSE DI RESISTENZA MINIMA: C12/15
- CLASSE DI ESPOSIZIONE AMBIENTALE: X0

**CALCESTRUZZO PER OPERE DEFINITIVE**
Rif. UNI EN 206

- CLASSE DI CONSISTENZA: S5
- CLASSE DI ESPOSIZIONE AMBIENTALE: XC4+XA2
- RAPPORTO MASSIMO a/c: 0.5
- CONTENUTO DI CLORURI: Cl<0.4
- DIAMETRO MASSIMO DEGLI INERTI: $D_{max}$=25mm
- CEMENTO RESISTENTE AI SOLFATI
- CLASSE DI RESISTENZA MINIMA: C32/40
- COPRIFERRO NOMINALE: 40 mm

## SALDATURE

- TUTTE LE SALDATURE A CORDONE D'ANGOLO DOVRANNO AVERE SPESSORE DI GOLA MAGGIORE O UGUALE A 0,7 VOLTE LO SPESSORE MINIMO DA SALDARE.
- PER LA SALDATURA AD ARCO MANUALE DEVONO ESSERE IMPIEGATI ELOTTRODI RIVESTITI OMOLOGATI SECONDO UNI EN ISO 2560, SECONDO QUANTO PREVISTO AL 11.3.4.5 DELLE NTC 2018.
- SALDATURE DI PRIMA CLASSE PER GIUNTO A T A COMPLETA PENETRAZIONE (Dove non diversamente indicato)

| PER TUTTE LE FLANGE |
|---|
| S1≥S2 |
| H=0.7xS2 |
| G=1.3xS2 |

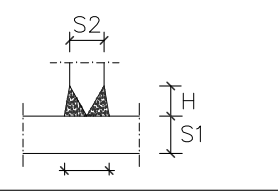

- SALDATURE A CORDONE D'ANGOLO (Dove non diversamente indicato)

| |
|---|
| S1≥S2 |
| H=S2 |
| G=0.7xS2 |

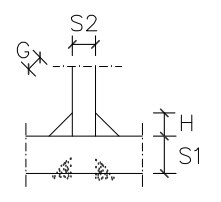

AZIENDA GARDESANA SERVIZI

"INTERVENTI DI RIQUALIFICAZIONE DEL SISTEMA DI RACCOLTA DEI REFLUI NEL BACINO DEL LAGO DI GARDA - SPONDA VERONESE"
Lotto 1 - Tratto 4 - 2°Stralcio
"OPERE COLLETTORE IN PRESSIONE ED OPERE COMPLEMENTARI TRATTO PERGOLANA - ROCCA VELA - COMUNE BARDOLINO"
Lotto 8 - Tratto 4_OC
CIG: B7E3B750B2 - CUP: J33F17000010002

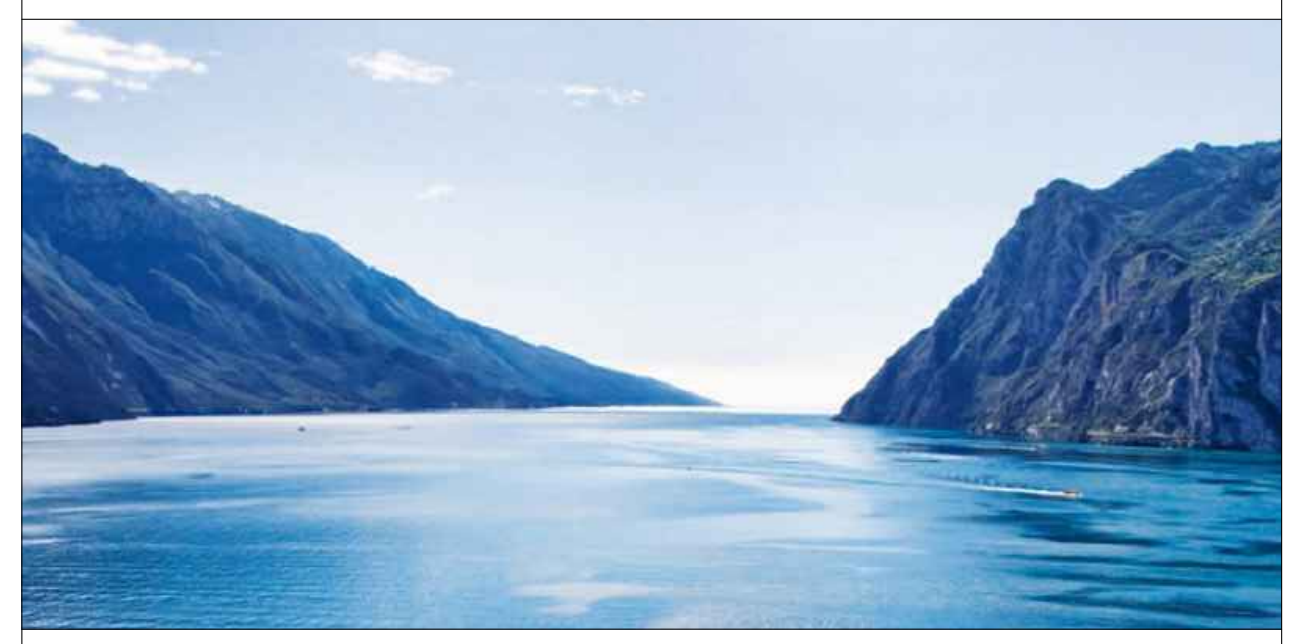

## PROGETTO ESECUTIVO

PROGETTISTA E COORDINATORE SICUREZZA IN FASE DI PROGETTO:
Ing. Giovanni Battista Matteotti

COLLABORAZIONE:
Ing. Luca Petracin
Ing. Andrea Martinello
Ing. Emanuele Anderlini
Ing. Filiberto Boscolo Lisetto
Geom. Elisa Zatti

mass
INGEGNERIA E ARCHITETTURA SRL
Via Sorio 33/a, 35141 PADOVA
Tel: 049-723320 - Mail: Info@matteotti.com

ING. G.B. MATTEOTTI

RESPONSABILE UNICO DEL PROGETTO:
Dott. Ing. Carlo Alberto Voi

| TITOLO | | | SCALA | CODICE ELABORATO | |
|---|---|---|---|---|---|
| VASCA ROMPITRATTA -<br>Opere Strutturali - Armature e dettagli | | | VARIE | C-4-002 | |
| N° REV | DATA | DESCRIZIONE | ESEGUITO | VERIFICATO | APPROVATO |
| 00 | Marzo 2026 | PRIMA EMISSIONE | | Ing. L. Petracin | Ing. G. B. Matteotti |
| 01 | Aprile 2026 | AGGIORNAMENTO A SEGUITO DI VERIFICA | | Ing. L. Petracin | Ing. G. B. Matteotti |
| 02 | Luglio 2026 | AGGIORNAMENTO POST VERIFICA AGS | | Ing. L. Petracin | Ing. G. B. Matteotti |
| 03 | | | | | |
| 04 | | | | | |