


IMPIANTO DI SOLLEVAMENTO DI SAN SEVERO
PIANTA OPERE PROVVISIONALI
SCALA 1:50

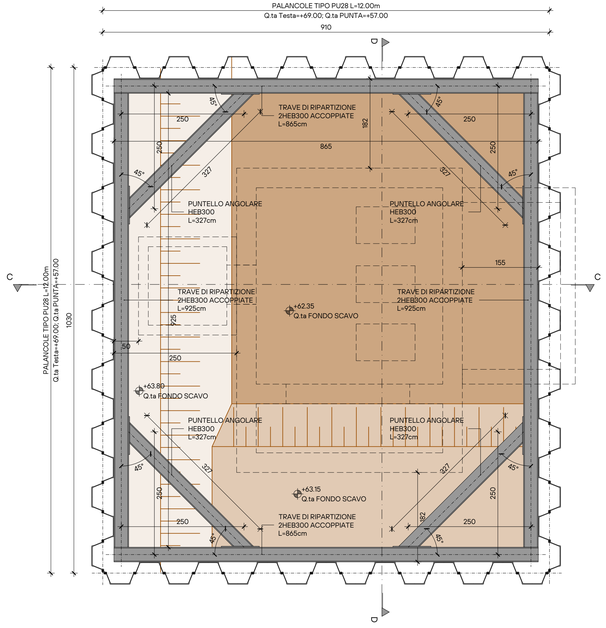


IMPIANTO DI SOLLEVAMENTO DI SAN SEVERO
SEZIONE D-D - OPERE PROVVISIONALI
SCALA 1:50

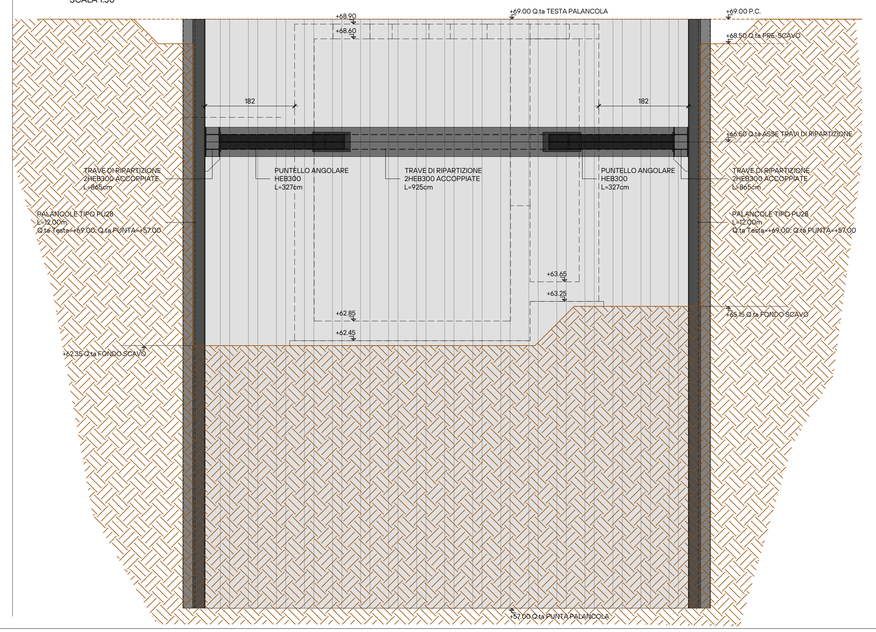


PIASTRE DI TESTA
PUNTELLI INCLINATI 700x600x20mm

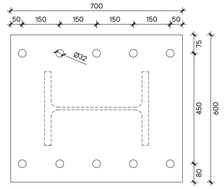

FAZZOLETTO DI SOSTEGNO
sp.=20mm

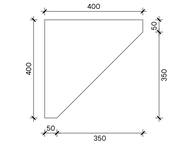

PIASTRE DI IRRIGIDIMENTO
sp.=10-15mm

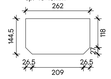

PIASTRA -TIPO 03-
sp.=20mm

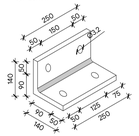


TABELLA MATERIALI

ACCIAIO

ACCIAIO PER CARPENTERIA METALLICA
(travi di ripartizione, puntelli, piastrame, etc...)

TIPO S355 (ts40mm):
- Resistenza caratteristica a snervamento: fyk > 355 MPa
- Resistenza caratteristica a rottura: ftk > 510 MPa

ACCIAIO PER PALANCOLE

TIPO S355GP (ts40mm):
- Resistenza caratteristica a snervamento: fyk > 355 MPa
- Resistenza caratteristica a rottura: ftk > 480 MPa

ACCIAIO PER C.A.
Rif. DM 17/01/2018

TIPO B450C saldabile:
- Resistenza caratteristica a snervamento: fyk > 450 MPa
- Resistenza caratteristica a rottura: ftk > 540 MPa

- Collegamento di barre d'armatura post-installate (inghisaggio): Impiegare ancorante chimico epossidico ad alte prestazioni tipo Hilti HIT-RE 500 v4 o equivalente secondo indicazioni del fornitore

CALCESTRUZZO

CALCESTRUZZO MAGRO
E GETTI DI LIVELLAMENTO

- CLASSE DI RESISTENZA MINIMA: C12/15
- CLASSE DI ESPOSIZIONE AMBIENTALE: XO

CALCESTRUZZO PER OPERE DEFINITIVE
Rif. UNI EN 206

- CLASSE DI CONSISTENZA: S5
- CLASSE DI ESPOSIZIONE AMBIENTALE: XC4+XA2
- RAPPORTO MASSIMO a/c: 0.5
- CONTENUTO DI CLORURI: Cl=0.4
- DIAMETRO MASSIMO DEGLI INERTI: D_{max}=25mm
- CEMENTO RESISTENTE AI SOLFATI
- CLASSE DI RESISTENZA MINIMA: C32/40
- COPRIFERRO NOMINALE: 40 mm

SALDATURE


- TUTTE LE SALDATURE A CORDONE D'ANGOLO DOVRANNO AVERE SPESSORE DI GOLA MAGGIORE O UGUALE A 0,7 VOLTE LO SPESSORE MINIMO DA SALDARE.
- PER LA SALDATURA AD ARCO MANUALE DEVONO ESSERE IMPIEGATI ELOTTRODI RIVESTITI OMOLOGATI SECONDO UNI EN ISO 2560, SECONDO QUANTO PREVISTO AL 11.3.4.5 DELLE NTC 2018.
- SALDATURE DI PRIMA CLASSE PER GIUNTO A T A COMPLETA PENETRAZIONE (Dove non diversamente indicato)

PER TUTTE LE FLANGE
S1≥S2
H=0.7xS2
G=1.3xS2




- SALDATURE A CORDONE D'ANGOLO (Dove non diversamente indicato)

S1≥S2
H=S2
G=0.7xS2

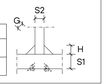


IMPIANTO DI SOLLEVAMENTO DI SAN SEVERO
SEZIONE C-C - OPERE PROVVISIONALI
SCALA 1:50

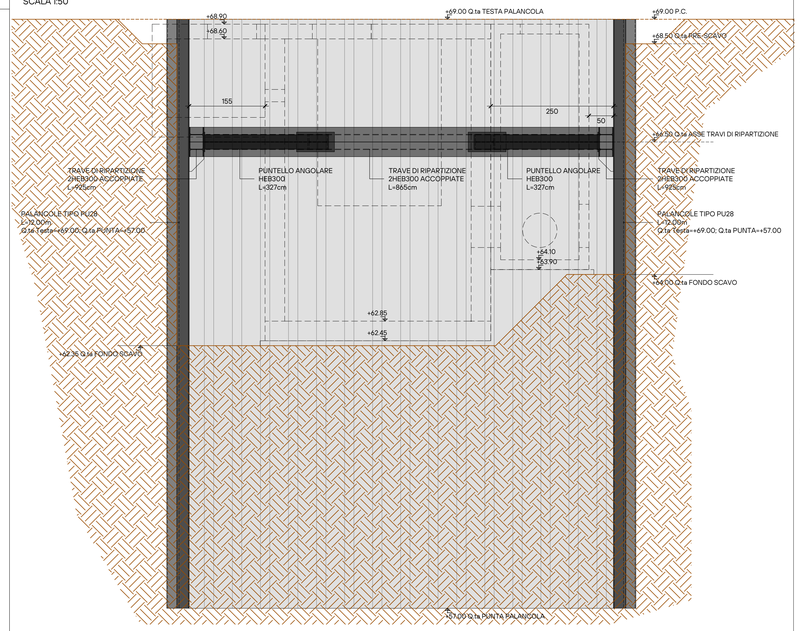


N.B: INSTALLARE OPPORTUNO SISTEMA DI AGGOTTAMENTO E CONTROLLO DELLA FALDA DA MANTENERSI ATTIVO DURANTE LE FASI DI SCAVO


IMPIANTO DI SOLLEVAMENTO DI SAN SEVERO
COLLEGAMENTO TRAVI DI RIPARTIZIONE-PALANCOLE
SCALA 1:10

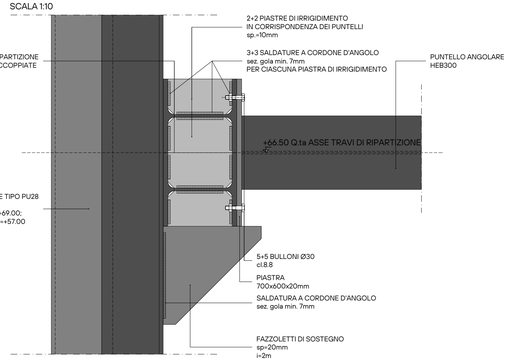


IMPIANTO DI SOLLEVAMENTO DI SAN SEVERO
COLLEGAMENTO TRA TRAVI DI RIPARTIZIONE
SCALA 1:10

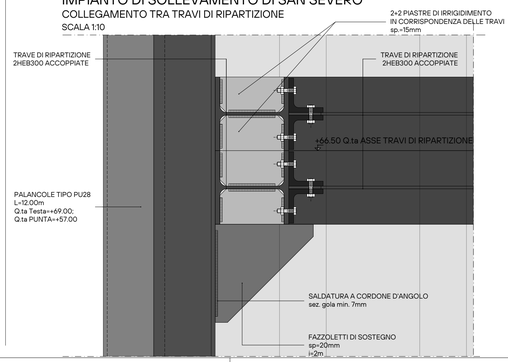

IMPIANTO DI SOLLEVAMENTO DI SAN SEVERO
COLLEGAMENTO TRAVI DI RIPARTIZIONE-PUNTELLO
SCALA 1:10

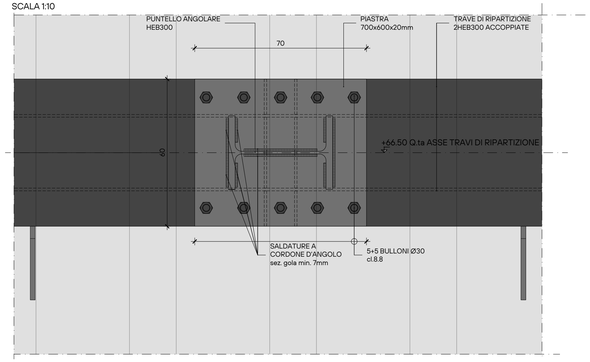


IMPIANTO DI SOLLEVAMENTO DI SAN SEVERO
COLLEGAMENTO TRA TRAVI DI RIPARTIZIONE
SCALA 1:10

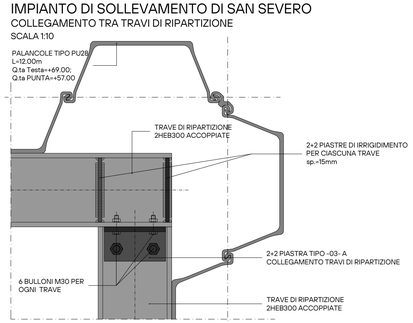

AZIENDA GARDESANA SERVIZI — ags | azienda gardesana servizi

"INTERVENTI DI RIQUALIFICAZIONE DEL SISTEMA DI RACCOLTA DEI REFLUI NEL BACINO DEL LAGO DI GARDA - SPONDA VERONESE"
Lotto 1 - Tratto 4 - 2°Stralcio
"OPERE COLLETTORE IN PRESSIONE ED OPERE COMPLEMENTARI TRATTO PERGOLANA - ROCCA VELA - COMUNE BARDOLINO"
Lotto 8 - Tratto 4_OC
CIG: B7E3B750B2 - CUP: J33F17000010002

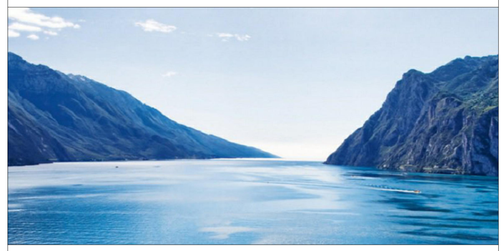

PROGETTO ESECUTIVO

PROGETTISTA E COORDINATORE SICUREZZA IN FASE DI PROGETTO:
Ing. Giovanni Battista Matteotti

COLLABORAZIONE:
Ing. Luca Petracin
Ing. Andrea Martinello
Ing. Emanuele Anderlini
Ing. Filiberto Boscolo Lisetto
Geom. Elisa Zatti

mass INGEGNERIA E ARCHITETTURA SRL
Via Sorio 35/a, 35141 PADOVA
Tel. 049-723320 - Mail: info@matteotti.com

RESPONSABILE UNICO DEL PROGETTO:
Dott. Ing. Carlo Alberto Voi

TITOLO	SCALA	CODICE ELABORATO
NUOVO IMPIANTO DI SOLLEVAMENTO DI SAN SEVERO - Opere Strutturali - Carpenterie, piante e sezioni	1:50	C-5-001

N° REV	DATA	DESCRIZIONE	ESEGUITO	VERIFICATO	APPROVATO
00	Marzo 2026	PRIMA EMISSIONE		Ing. L. Petracin	Ing. G. B. Matteotti
01	Aprile 2026	AGGIORNAMENTO A SEGUITO DI VERIFICA		Ing. L. Petracin	Ing. G. B. Matteotti
02					
03					
04					