


ATTRAVERSAMENTO MICROTUNNELING - Planimetria di inquadramento
(Scala 1:200)

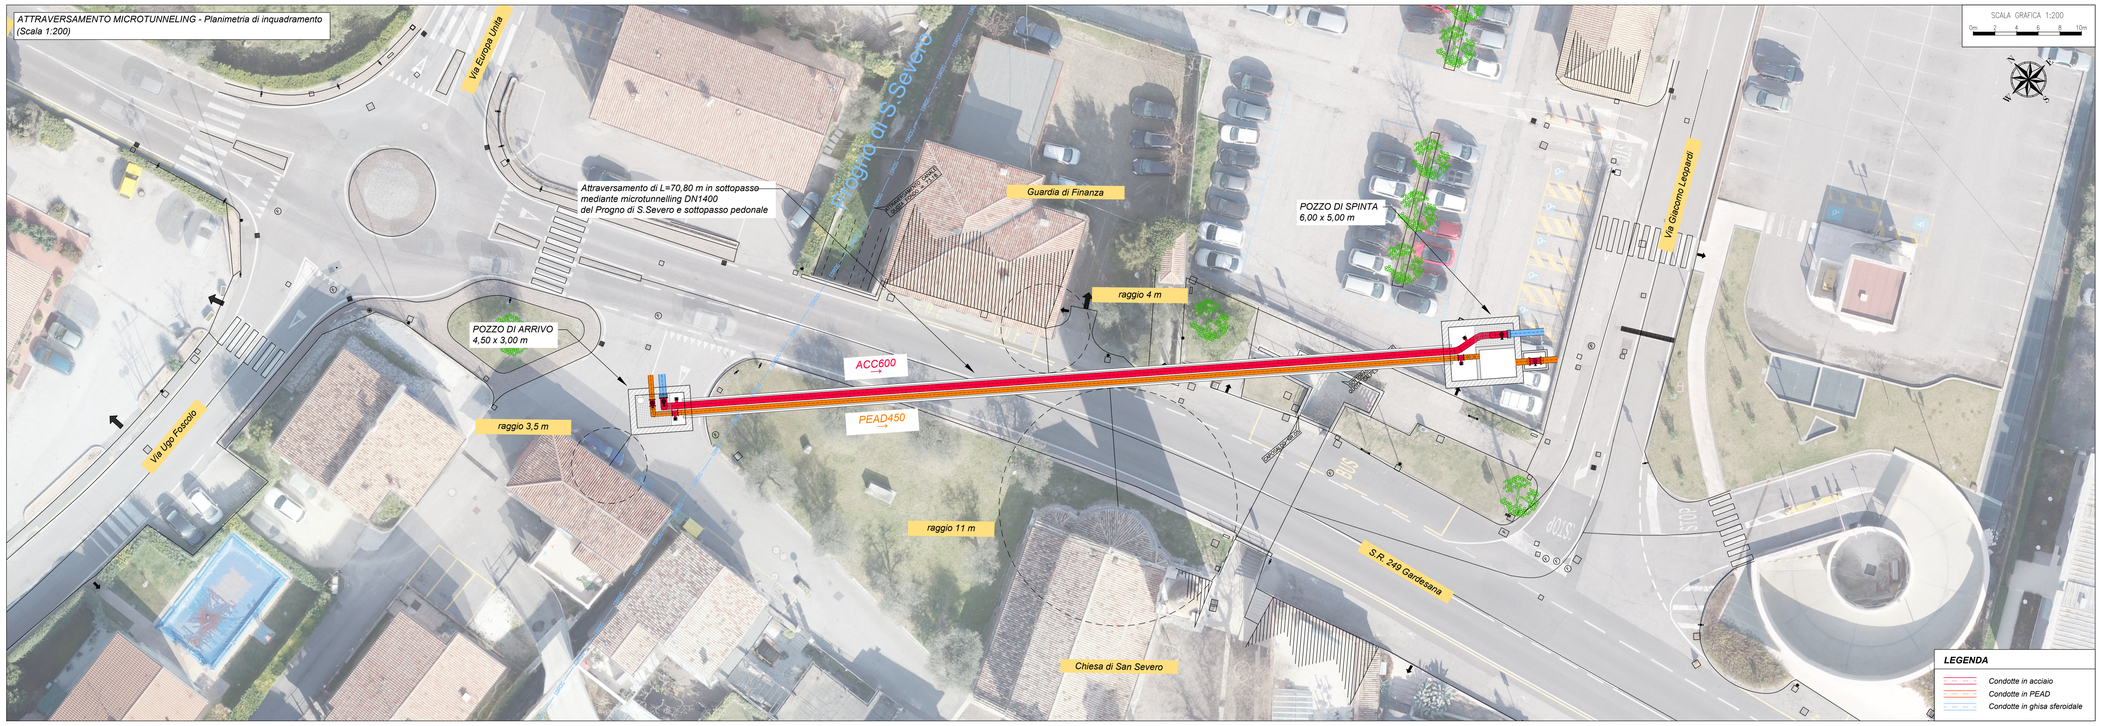

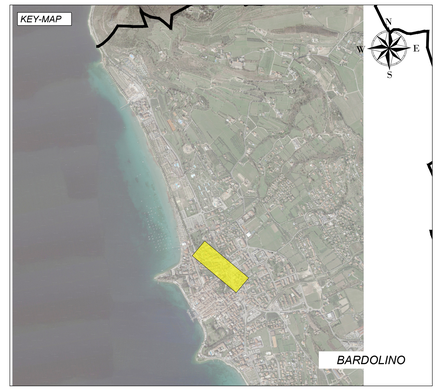


Installazione condotte all'interno del tubo camicia

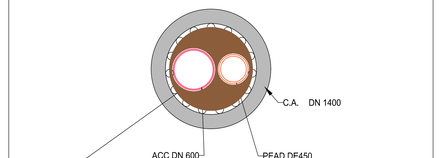


La posa delle tubazioni all'interno del tubo camicia avviene con collari distanziatori speciali, costituiti da una struttura in acciaio per tenere in formazione le due condotte e sistema di scorrimento, all'interno del tubo camicia, costituito da ruote o anelli distanziatori in materiale plastico (il cui dimensionamento sarà a cura dell'impresa esecutrice).
Questa struttura dovrà consentire, al tempo stesso, sia lo scorrimento delle condotte di progetto all'interno del tubo camicia DN1400 e sia il loro successivo sfilamento.
L'interasse dei collari distanziatori dovrà essere al massimo di 6 m.
Il sistema deve essere in grado di preservare le condotte dalle eventuali abrasioni degli strati superficiali di rivestimento durante le fasi di posa.


ATTRAVERSAMENTO MICROTUNNELING - Pianta
(Scala 1:100)

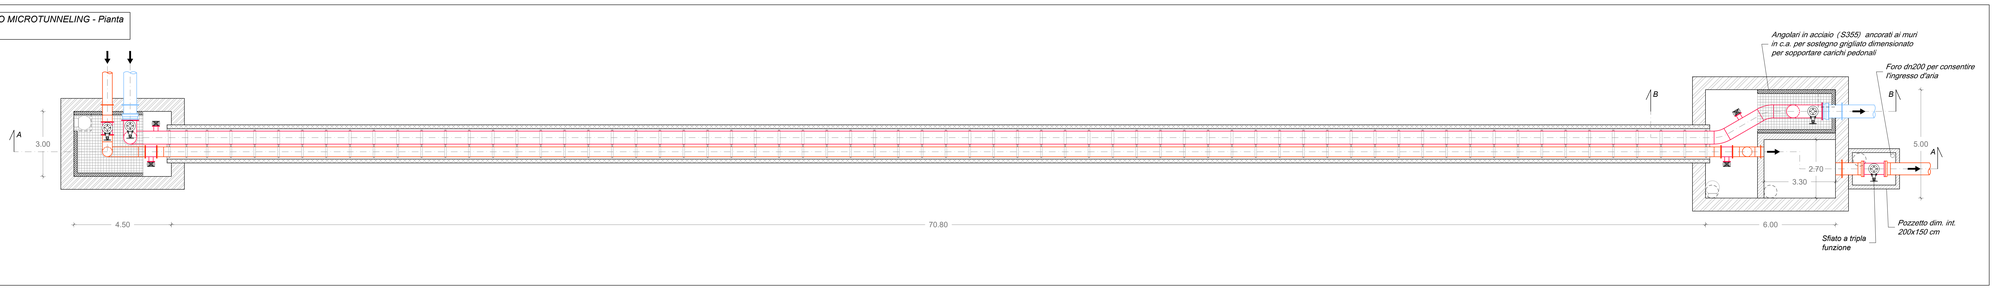

ATTRAVERSAMENTO MICROTUNNELING - Sezione longitudinale A-A
(Scala 1:100)

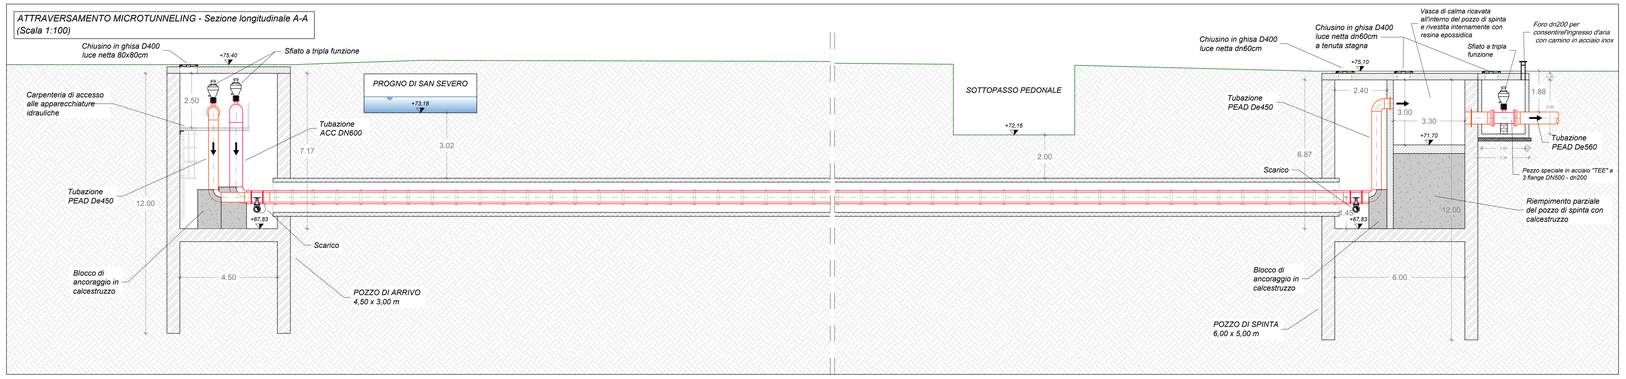

ATTRAVERSAMENTO MICROTUNNELING - Sezione longitudinale B-B
(Scala 1:100)

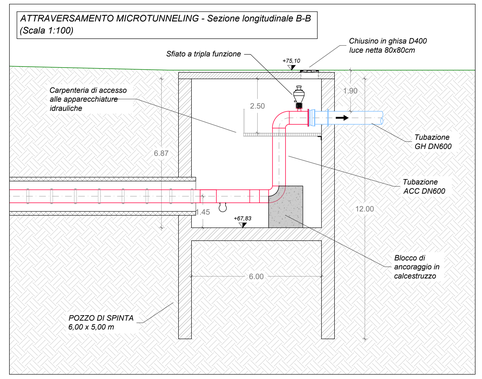

AZIENDA GARDESANA SERVIZI

"INTERVENTI DI RIQUALIFICAZIONE DEL SISTEMA DI RACCOLTA DEI REFLUI NEL BACINO DEL LAGO DI GARDA - SPONDA VERONESE"
Lotto 1 - Tratto 4 - 2°Stralcio
"OPERE COLLETTORE IN PRESSIONE ED OPERE COMPLEMENTARI TRATTO PERGOLANA - ROCCA VELA - COMUNE BARDOLINO"
Lotto 8 - Tratto 4_QC
CIG: B7E3B750B2 - CUP: J33F17000010002



PROGETTO ESECUTIVO

PROGETTISTA E COORDINATORE SICUREZZA IN FASE DI PROGETTO:
Ing. Giovanni Battista Matteotti

COLLABORAZIONE:
Ing. Luca Petracin
Ing. Andrea Martinello
Ing. Emanuele Anderlini
Ing. Filiberto Boscolo Lisetto
Geom. Elisa Zatti

mass INGEGNERIA E ARCHITETTURA SRL
Via Sorio 35/a, 35141 PADOVA
Tel. 049-723320 - Mail: info@mass4.com

RESPONSABILE UNICO DEL PROGETTO:
Dott. Ing. Carlo Alberto Voi

TITOLO	COLLETTORE FOGNARIO IN PRESSIONE - ATTRAVERSAMENTO PROGNO DI SAN SEVERO E SOTTOPASSO PEDONALE A: PIANTE, SEZIONI E PARTICOLARI COSTRUTTIVI	SCALA	CODICE ELABORATO
		varie	B-65-001

N° REV	DATA	DESCRIZIONE	ESEGUITO	VERIFICATO	APPROVATO
00	Marzo 2026	PRIMA EMISSIONE	Ing. A. Martinello	Ing. L. Petracin	Ing. G. B. Matteotti
01	Luglio 2026	AGGIORNAMENTO POST VERIFICA AGS	Ing. A. Martinello	Ing. L. Petracin	Ing. G. B. Matteotti
02					
03					
04					