
ATTRAVERSAMENTO SPINGITUBO - Planimetria di inquadramento
(Scala 1:200)

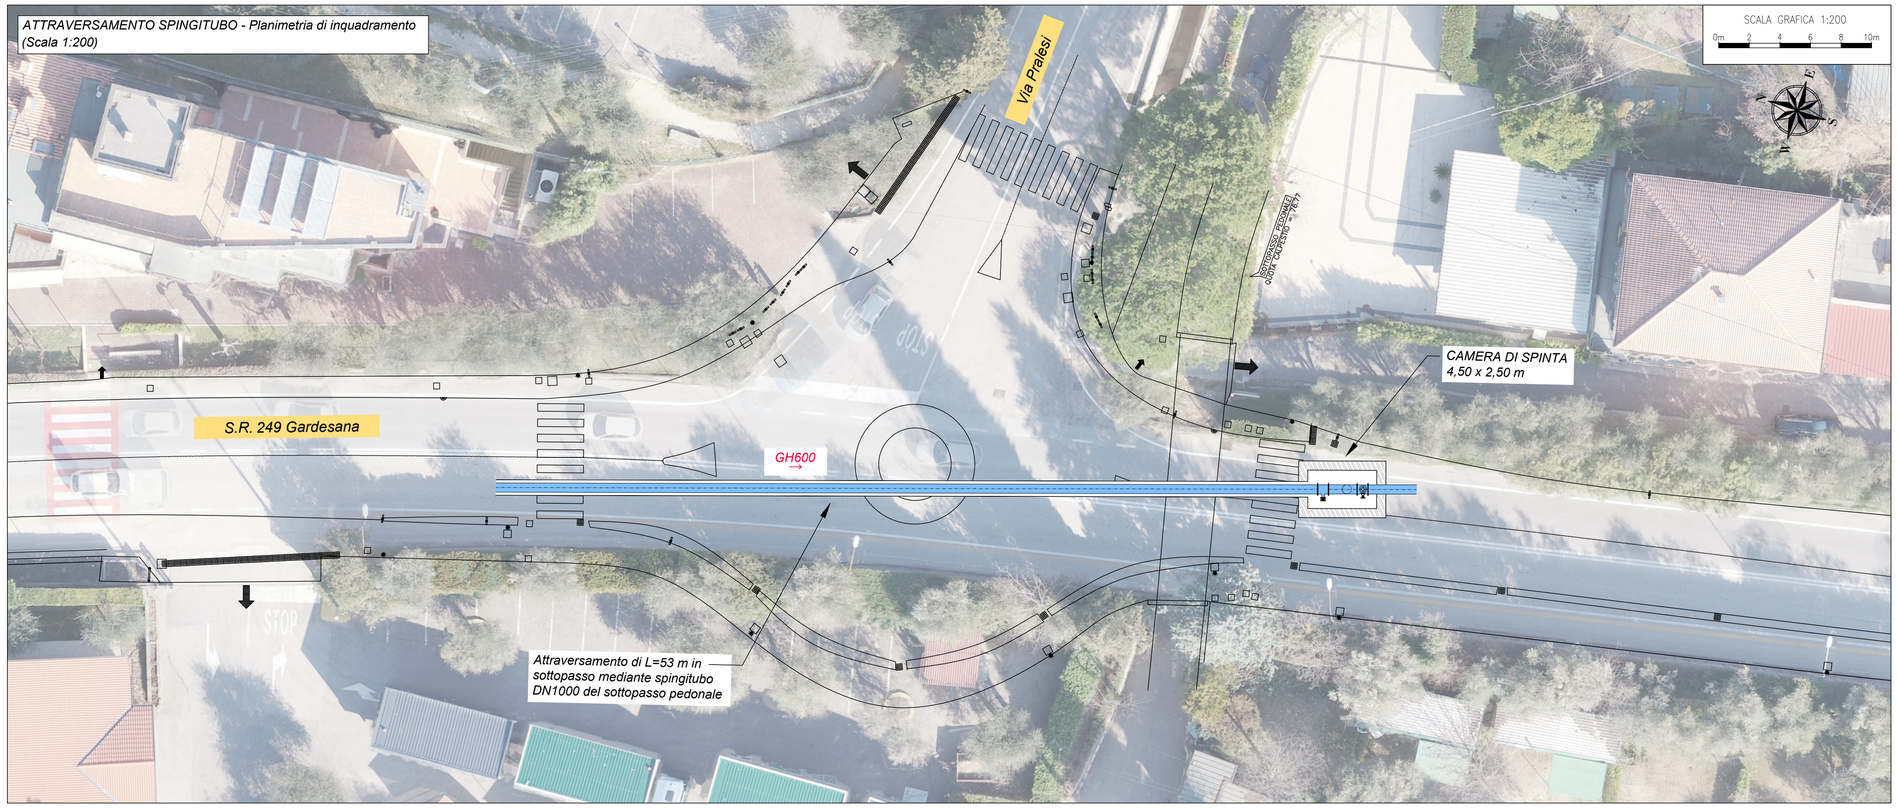


KEY-MAP



ATTRAVERSAMENTO SPINGITUBO - Pianta
(Scala 1:100)



ATTRAVERSAMENTO SPINGITUBO - Sezione longitudinale
(Scala 1:100)

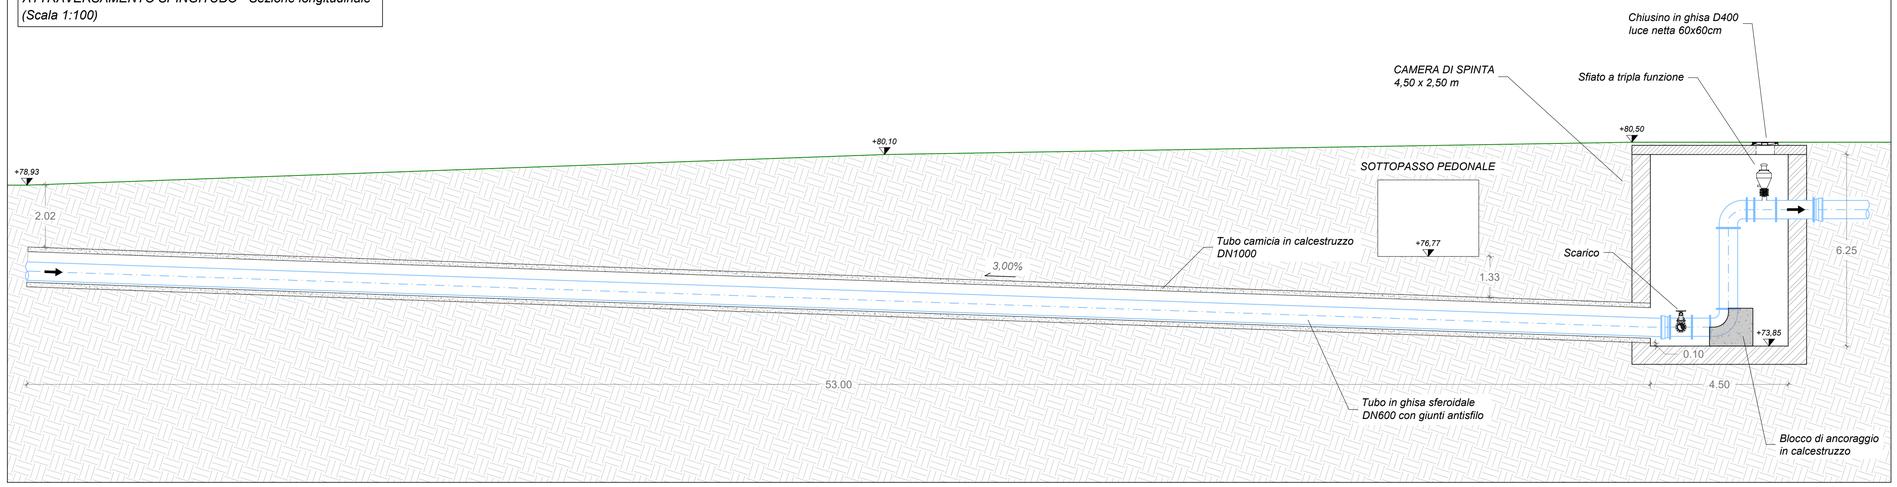

AZIENDA GARDESANA SERVIZI

ags azienda gardesana servizi

"INTERVENTI DI RIQUALIFICAZIONE DEL SISTEMA DI RACCOLTA DEI REFLUI NEL BACINO DEL LAGO DI GARDA - SPONDA VERONESE"
Lotto 1 - Tratto 4 - 2°Stralcio
"OPERE COLLETTORE IN PRESSIONE ED OPERE COMPLEMENTARI TRATTO PERGOLANA - ROCCA VELA - COMUNE BARDOLINO"
Lotto 8 - Tratto 4_OC
CIG: B7E3B750B2 - CUP: J33F17000010002



PROGETTO ESECUTIVO

PROGETTISTA E COORDINATORE SICUREZZA IN FASE DI PROGETTO:
Ing. Giovanni Battista Matteotti

COLLABORAZIONE:
Ing. Luca Petracin
Ing. Andrea Martinello
Ing. Emanuele Anderlini
Ing. Filiberto Boscolo Lisetto
Geom. Elisa Zatti

mass INGEGNERIA E ARCHITETTURA SRL
Via Sorio 33/a, 35141 PADOVA
Tel: 049-723320 - Mail: info@matteotti.com

RESPONSABILE UNICO DEL PROGETTO:
Dott. Ing. Carlo Alberto Voi

TITOLO	SCALA	CODICE ELABORATO
COLLETTORE FOGNARIO IN PRESSIONE - ATTRAVERSAMENTO SOTTOPASSO PEDONALE B: PIANTE, SEZIONI E PARTICOLARI COSTRUTTIVI	varie	B-66-001

N° REV	DATA	DESCRIZIONE	ESEGUITO	VERIFICATO	APPROVATO
00	Marzo 2026	PRIMA EMISSIONE	Ing. A. Martinello	Ing. L. Petracin	Ing. G. B. Matteotti
01	Luglio 2026	AGGIORNAMENTO POST VERIFICA AGS	Ing. A. Martinello	Ing. L. Petracin	Ing. G. B. Matteotti
02					
03					
04					